




DRAWING LIST

-
- 000 Cover Sheet
 - 001 Location Plan
 - 002 Site Hoarding & Access Plan
 - 010 Demolition Plan
 - 011 Site Roof Plan
 - 100 Floor Plan - Canopy 1
 - 101 Floor Plan - Canopy 2, 3 & 4
 - 102 Roof Plan - Canopy 1
 - 103 Roof Plan - Canopy 2, 3 & 4
 - 200 Reflected Ceiling Plan
 - 300 Elevations & Section - Canopy 1
 - 301 Typical Elevations & Section - Canopy 2, 3 & 4
 - 302 Stair & Handrail Details
 - 500 Typical Canopy Details
 - 600 Lower Ground Plan - Marks Pavilion Amenities
 - 700 Existing & Proposed Phipps Field Amenities
 - 701 Interior Elevations - Phipps Field Amenities
 - 702 Wall Types & Screen Concept - Phipps Field Amenities

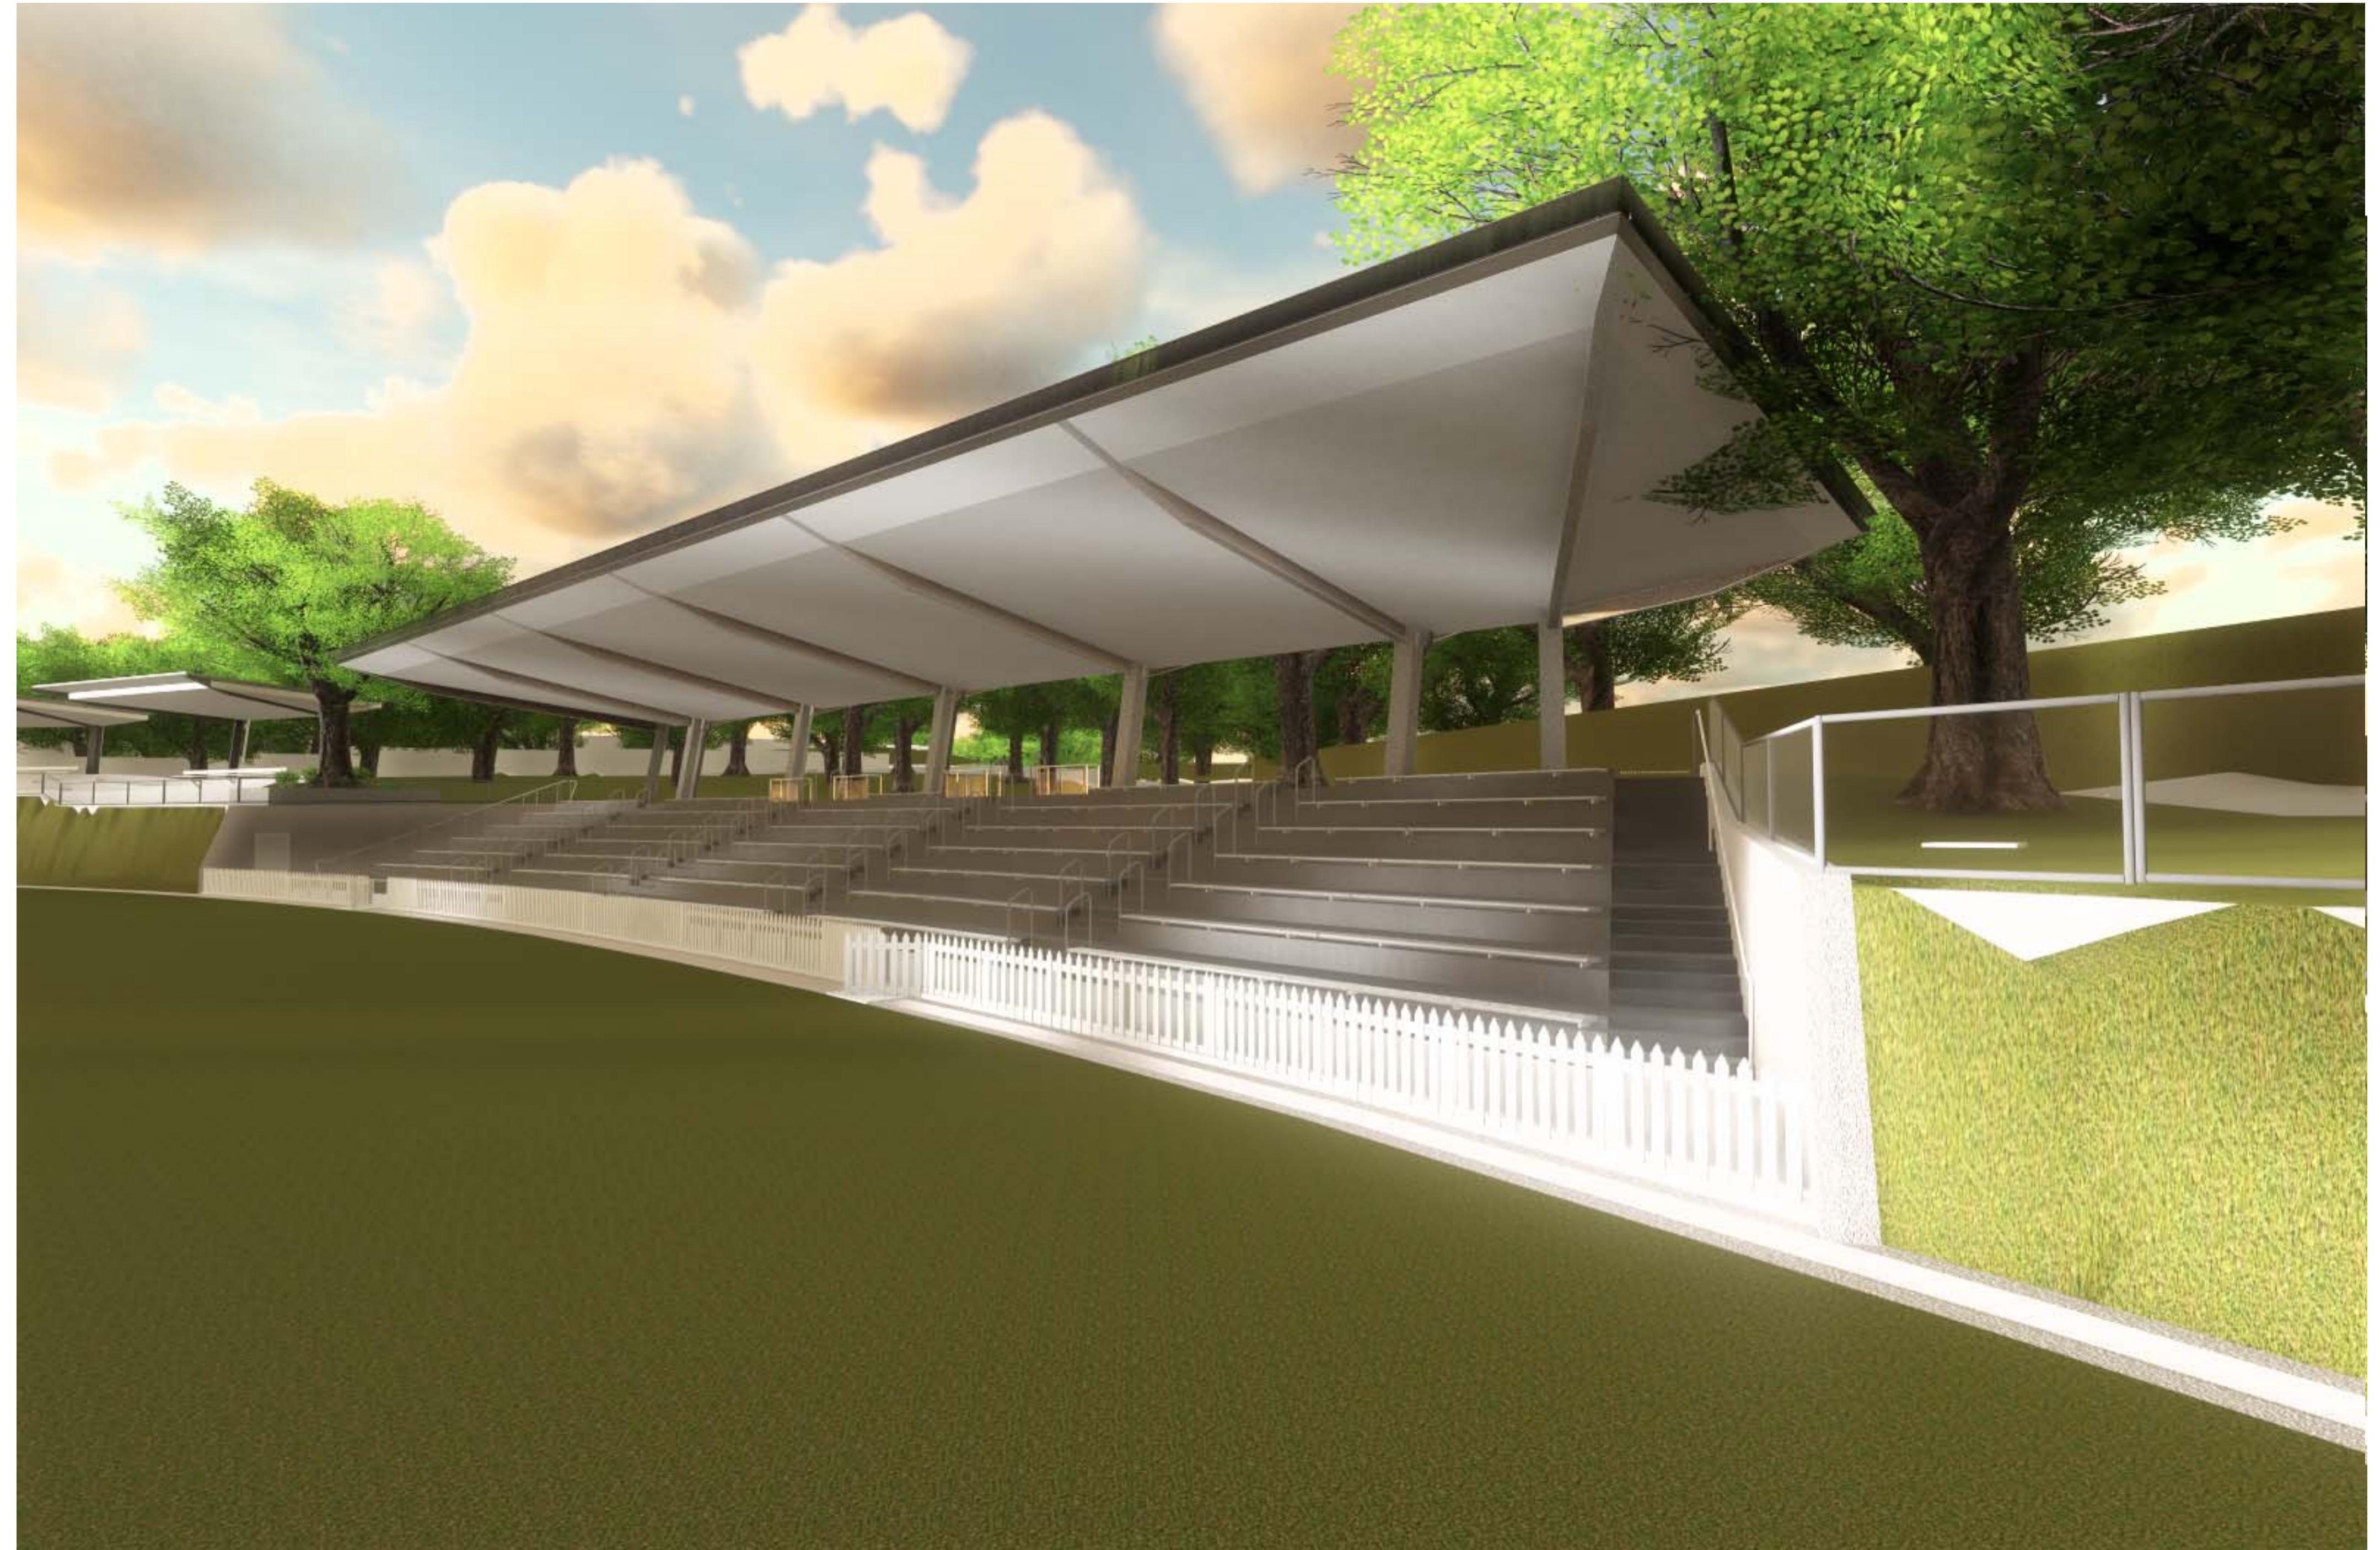

BARKER COLLEGE COVERED OUTDOOR SEATING AND AMENITIES UPGRADE

TENDER ISSUE AUGUST 2016



Issue No. A Date 31/08/16 Description TENDER ISSUE Chkd AT

TENDER ISSUE

Electrical Engineer
Ken Offord
601/80 George St, Hornsby, NSW
T: +61 2 9477 4300 F: 612 xxxx xxxx
E: ken@kroanda.com.au

Hydraulic Engineer
Sparks + Partners Consulting Engineers
Level 1, 91 George Street, Parramatta NSW
T: 0401 803 330 F: 612 xxxx xxxx
E: Leon@sparksandpartners.com.au

Project Manager
Barker College
91 Pacific Highway, Hornsby, NSW, 2077
T: 02 9647 8318 F: 612 xxxx xxxx
E: georgina_rogers@barker.nsw.edu.au

Drawing Title
Location Plan

Project & Client
BARKER OVAL C.O.L.A &
AMENITIES UPGRADE
at 91 Pacific Hwy, Hornsby, NSW, 2077
for BARKER COLLEGE

Architect
NBRS ARCHITECTURE.
Sydney 612 9922 2344 Melbourne 613 8676 0427
nbsarchitecture.com.au


Any form of replication of this drawing in full or in part without the written permission of
NBRS+PARTNERS Pty Ltd constitutes an infringement of the copyright
ABN 16 003 247 365 © 2016
Nominated Architects: Geoffrey Deane 3766; Andrew Duffin 5602; Garry Hoddnett 5286

Date 31/08/2016 5:36:26 PM
Scale 1 : 1500 @ A1
0 1m 2m 3m 4m 5m 6m

Drawing Reference
15494-WD 001 - A



- TRUCK SITE ACCESS ROUTE AND FLOW
- SITE HOARDING AND TEMPORARY FENCING
- EXTENT OF WORKS

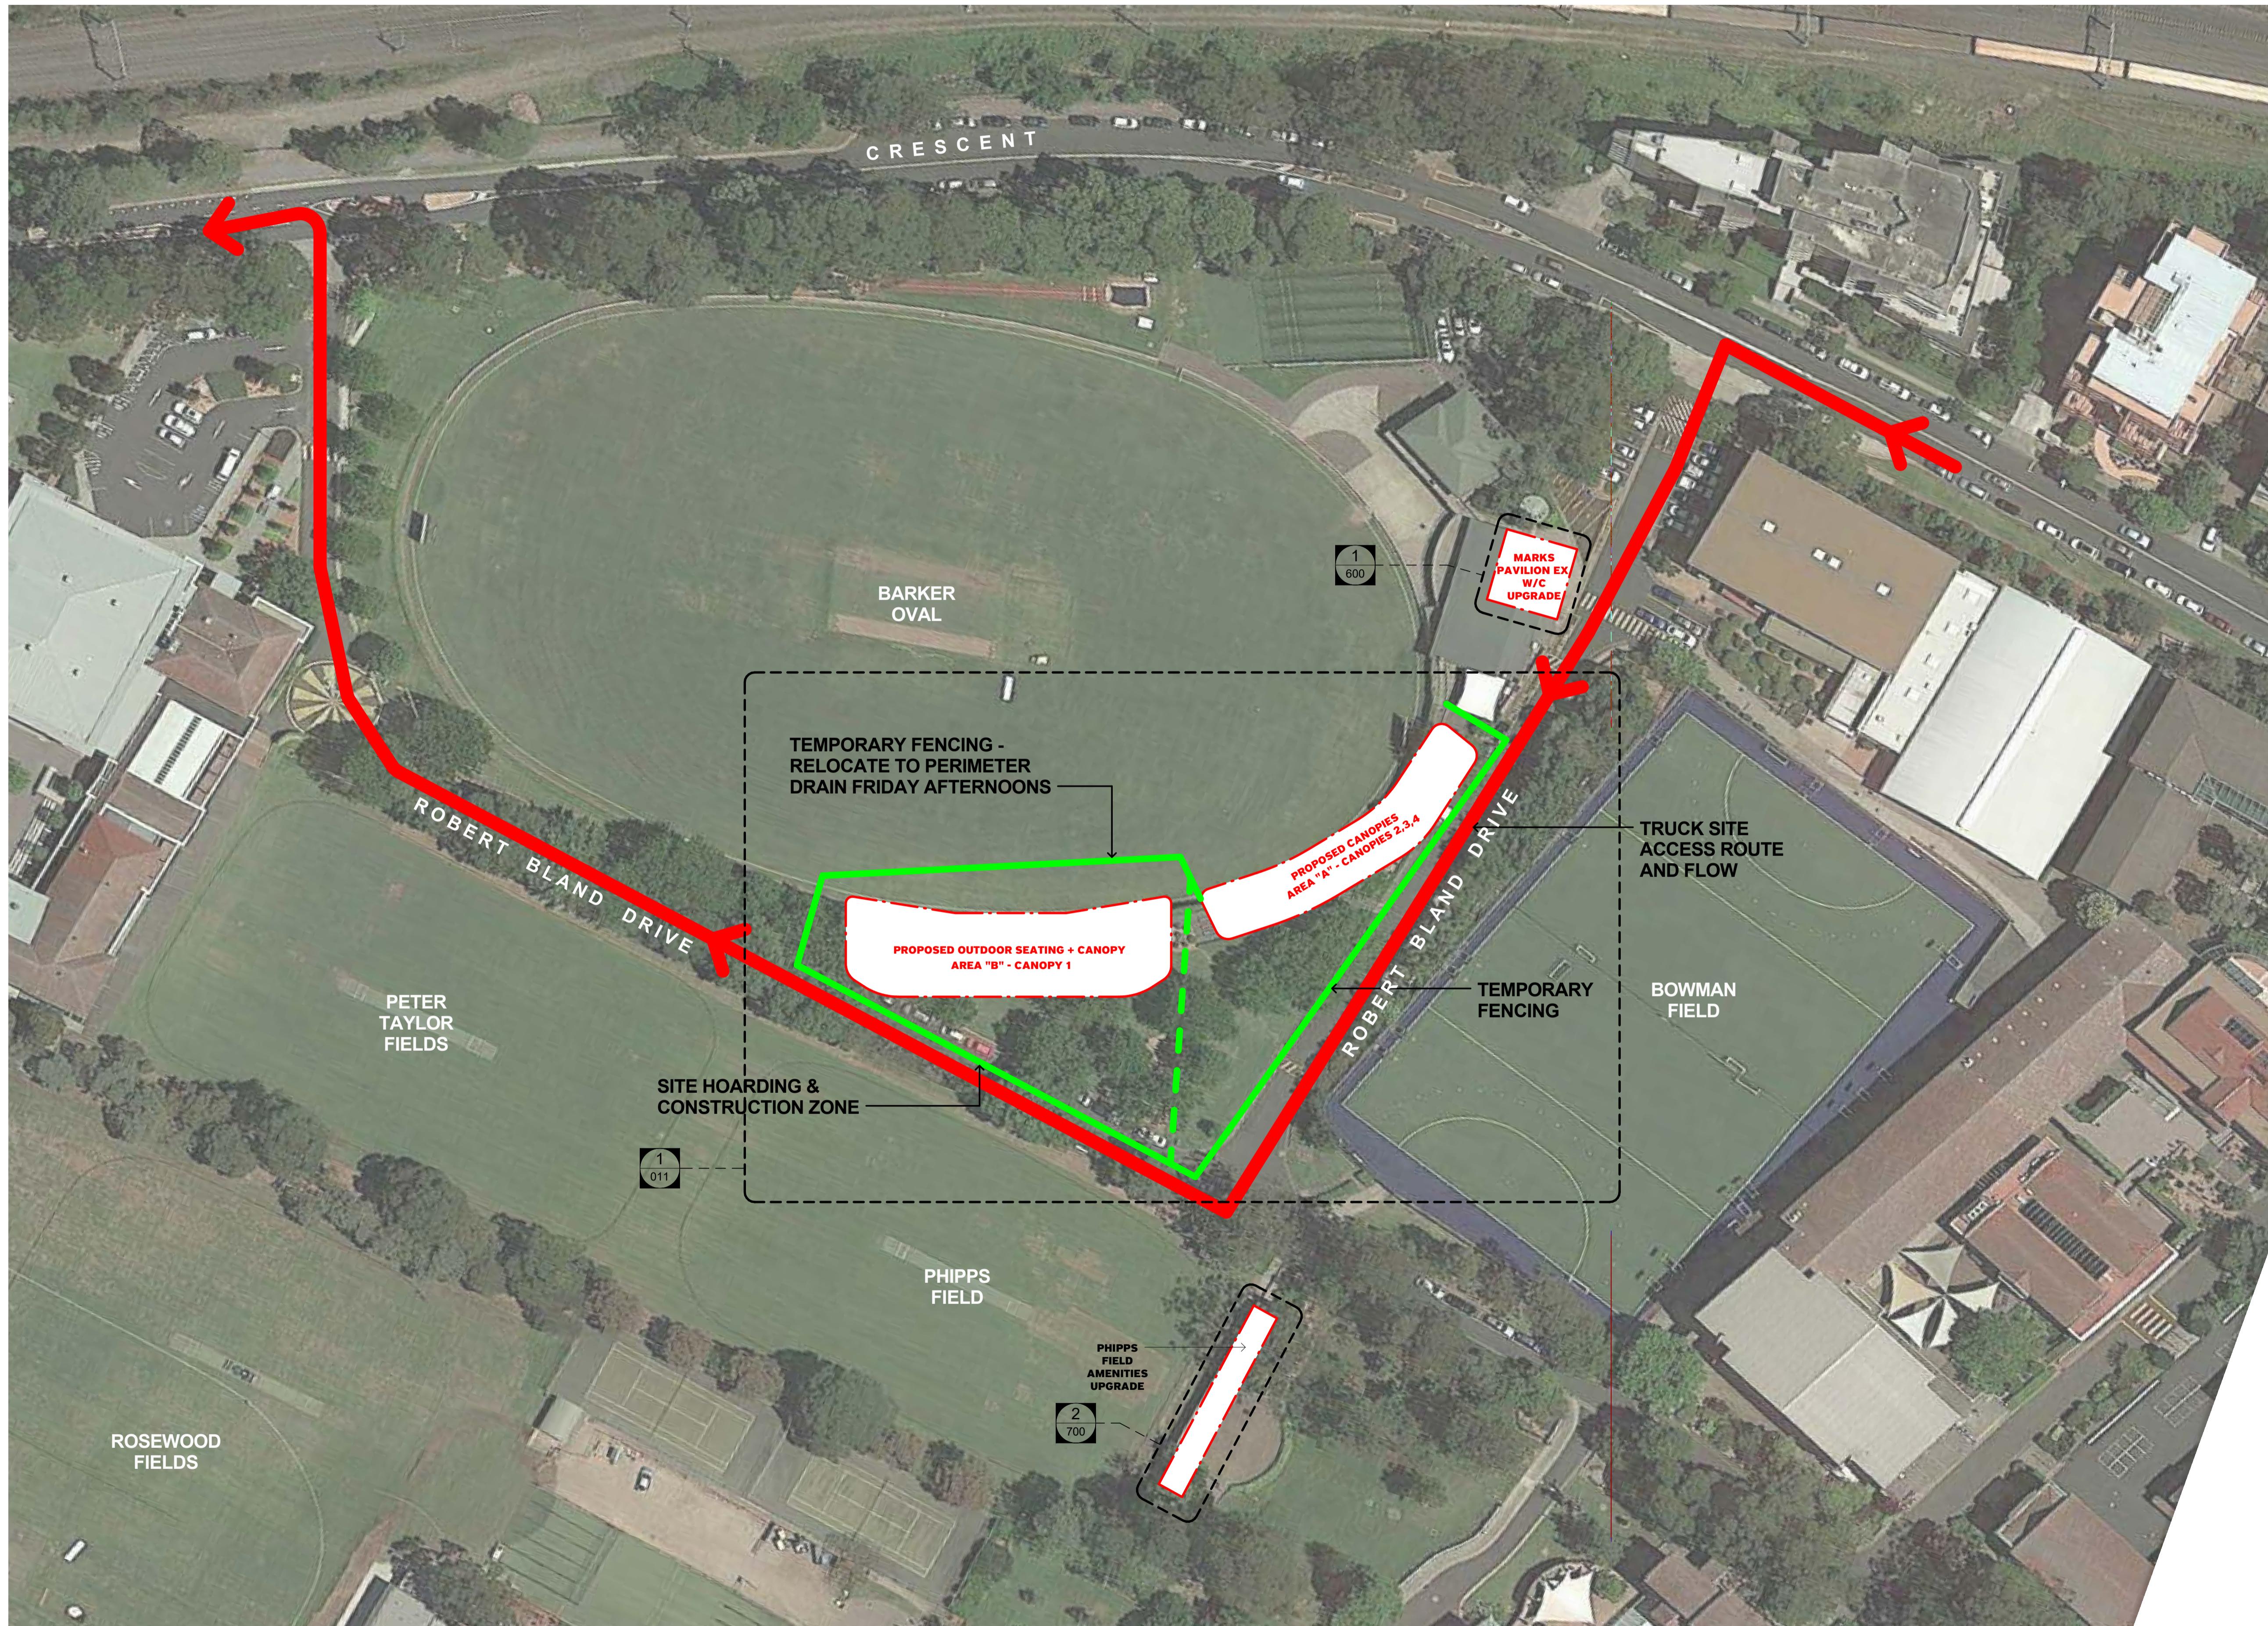

Issue No. Date 31/08/16 Description TENDER ISSUE Chkd AT

TENDER ISSUE

Electrical Engineer
Ken Offord
601/80 George St, Hornsby, NSW
T: +61 2 9477 4300 F: 612 xxxx xxxx
E: ken@kroanda.com.au

Hydraulic Engineer
Sparks + Partners Consulting Engineers
Level 1, 91 George Street, Parramatta NSW
T: 0401 803 330 F: 612 xxxx xxxx
E: Leon@sparksandpartners.com.au

Project Manager
Barker College
91 Pacific Highway, Hornsby, NSW, 2077
T: 02 9647 8318 F: 612 xxxx xxxx
E: georgina_rogers@barker.nsw.edu.au

Structural Engineer
Birzulis Associates
583 Darling Street Rozelle NSW 2039
T: 612 9555 7230 F: 612 xxxx xxxx
E: mgrogan@birzulisassociates.com

Drawing Title
Site Hoarding & Access Plan

Project & Client
BARKER OVAL C.O.L.A &
AMENITIES UPGRADE
at
91 Pacific Hwy, Hornsby, NSW, 2077
for
BARKER COLLEGE

Architect
NBRSArchitecture.
Sydney 612 9922 2344 Melbourne 613 8676 0427
nbsarchitecture.com.au
Any form of replication of this drawing in full or in part without the written permission of
NBRSA+PARTNERS Pty Ltd constitutes an infringement of the copyright
ABN 16 003 247 365 © 2016
Nominated Architects: Geoffrey Deane 3766; Andrew Duffin 5602; Garry Hoddinott 5286

Date 31/08/2016 5:36:27 PM
Scale As indicated @ A1
0 1m 2m 3m 4m 5m 6m
Drawing Reference
15494-WD 002-A




EXISTING DEMOLISHED TREE

EXISTING RETAINED TREE

NOTE: REFER TO LANDSCAPE DRAWINGS

EXTENT OF BULK EXCAVATION

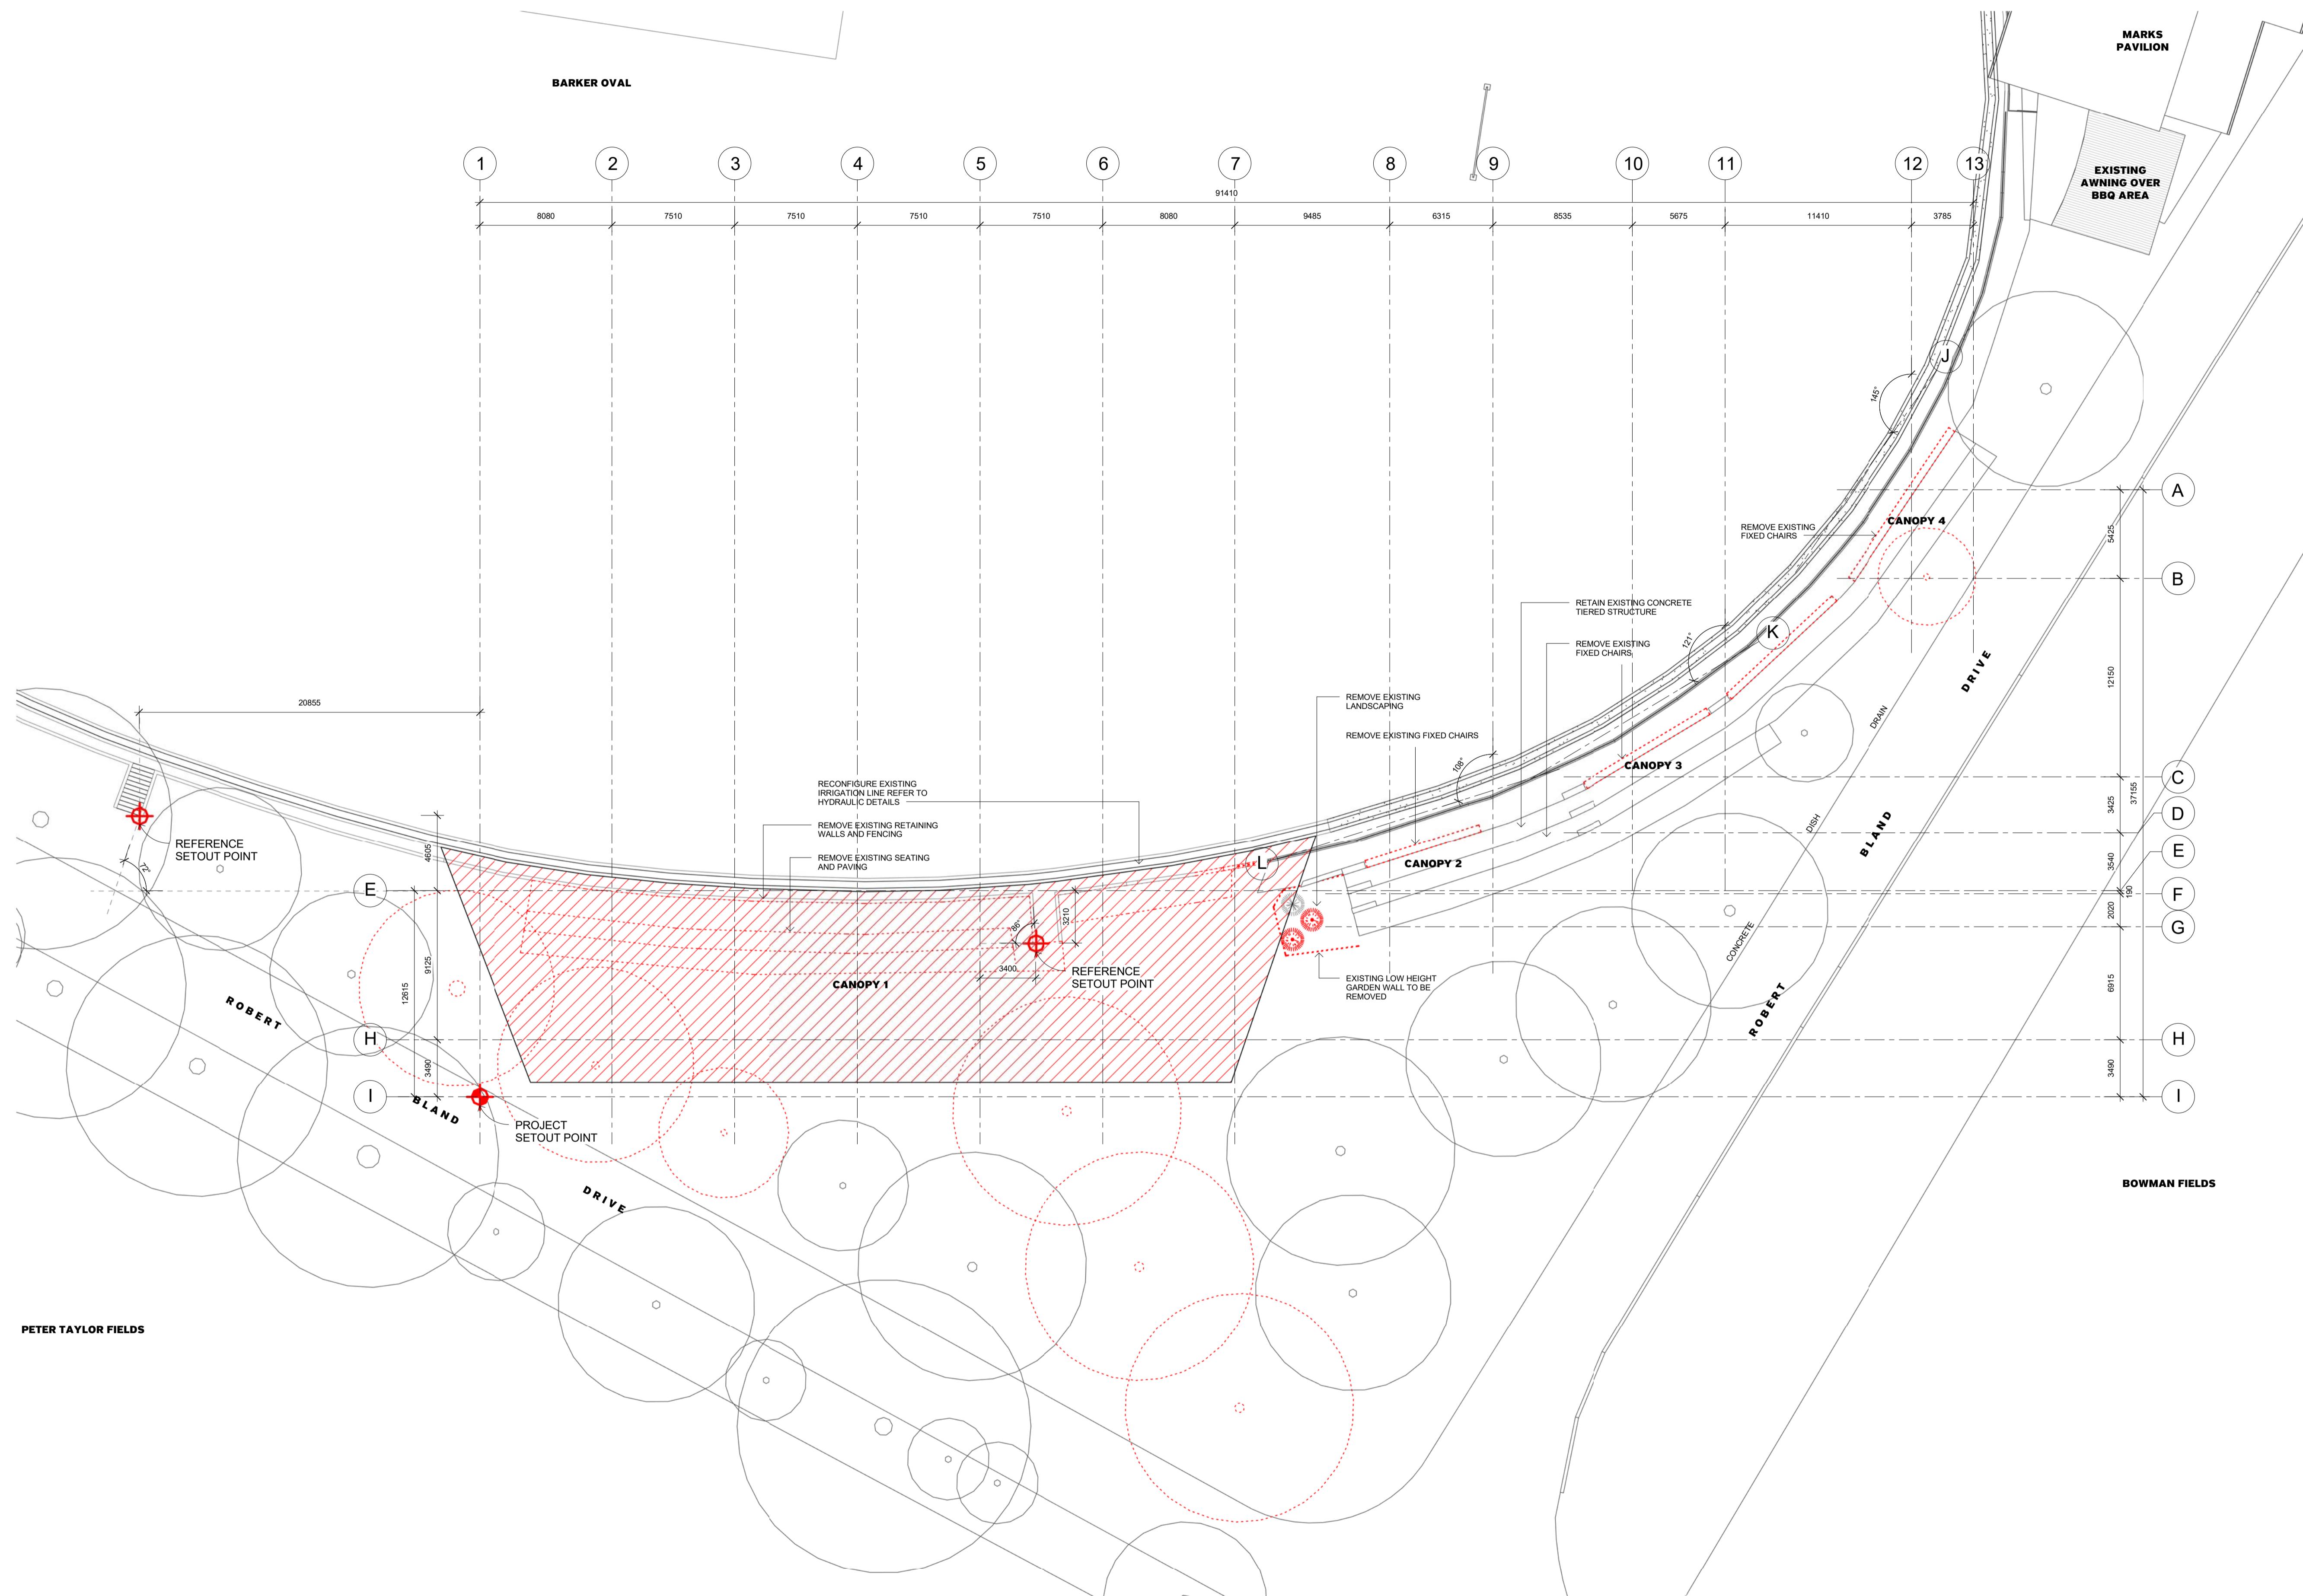

PETER TAYLOR FIELDS

Issue No. A Date 31/08/16 Description TENDER ISSUE Chkd AT

TENDER ISSUE

Electrical Engineer
Ken Offord
601/80 George St, Hornsby, NSW
T: +61 2 9477 4300 F: 612 xxxx xxxx
E: ken@kroanda.com.au

Hydraulic Engineer
Sparks+Partners Consulting Engineers
Level 1, 91 George Street, Parramatta NSW
T: 0401 803 330 F: 612 xxxx xxxx
E: Leon@sparksandpartners.com.au

Project Manager
Barker College
91 Pacific Highway, Hornsby, NSW, 2077
T: 02 9647 8318 F: 612 xxxx xxxx
E: georgina_rogers@barker.nsw.edu.au

Drawing Title
Demolition Plan

Project & Client
BARKER OVAL C.O.L.A & AMENITIES UPGRADE
at 91 Pacific Hwy, Hornsby, NSW, 2077
for **BARKER COLLEGE**

Architect
NBRSArchitecture.
Sydney 612 9922 2344 Melbourne 613 8676 0427
nbrsarchitecture.com.au


Any form of replication of this drawing in full or in part without the written permission of NBRSA+PARTNERS Pty Ltd constitutes an infringement of the copyright
ABN 16 003 247 365 © 2016
Nominated Architects: Geoffrey Deane 3766; Andrew Duffin 5602; Garry Hodnett 5286

Date 31/08/2016 5:36:32 PM
Scale 1 : 200 (@ A1)
0 1m 2m 3m 4m 5m 6m

Drawing Reference
15494-WD 010 - A




Legend

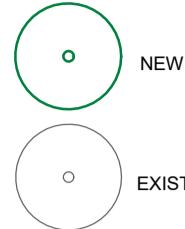

NOTE: REFER TO LANDSCAPE DRAWINGS

NOTE: REFER TO LANDSCAPE DRAWINGS

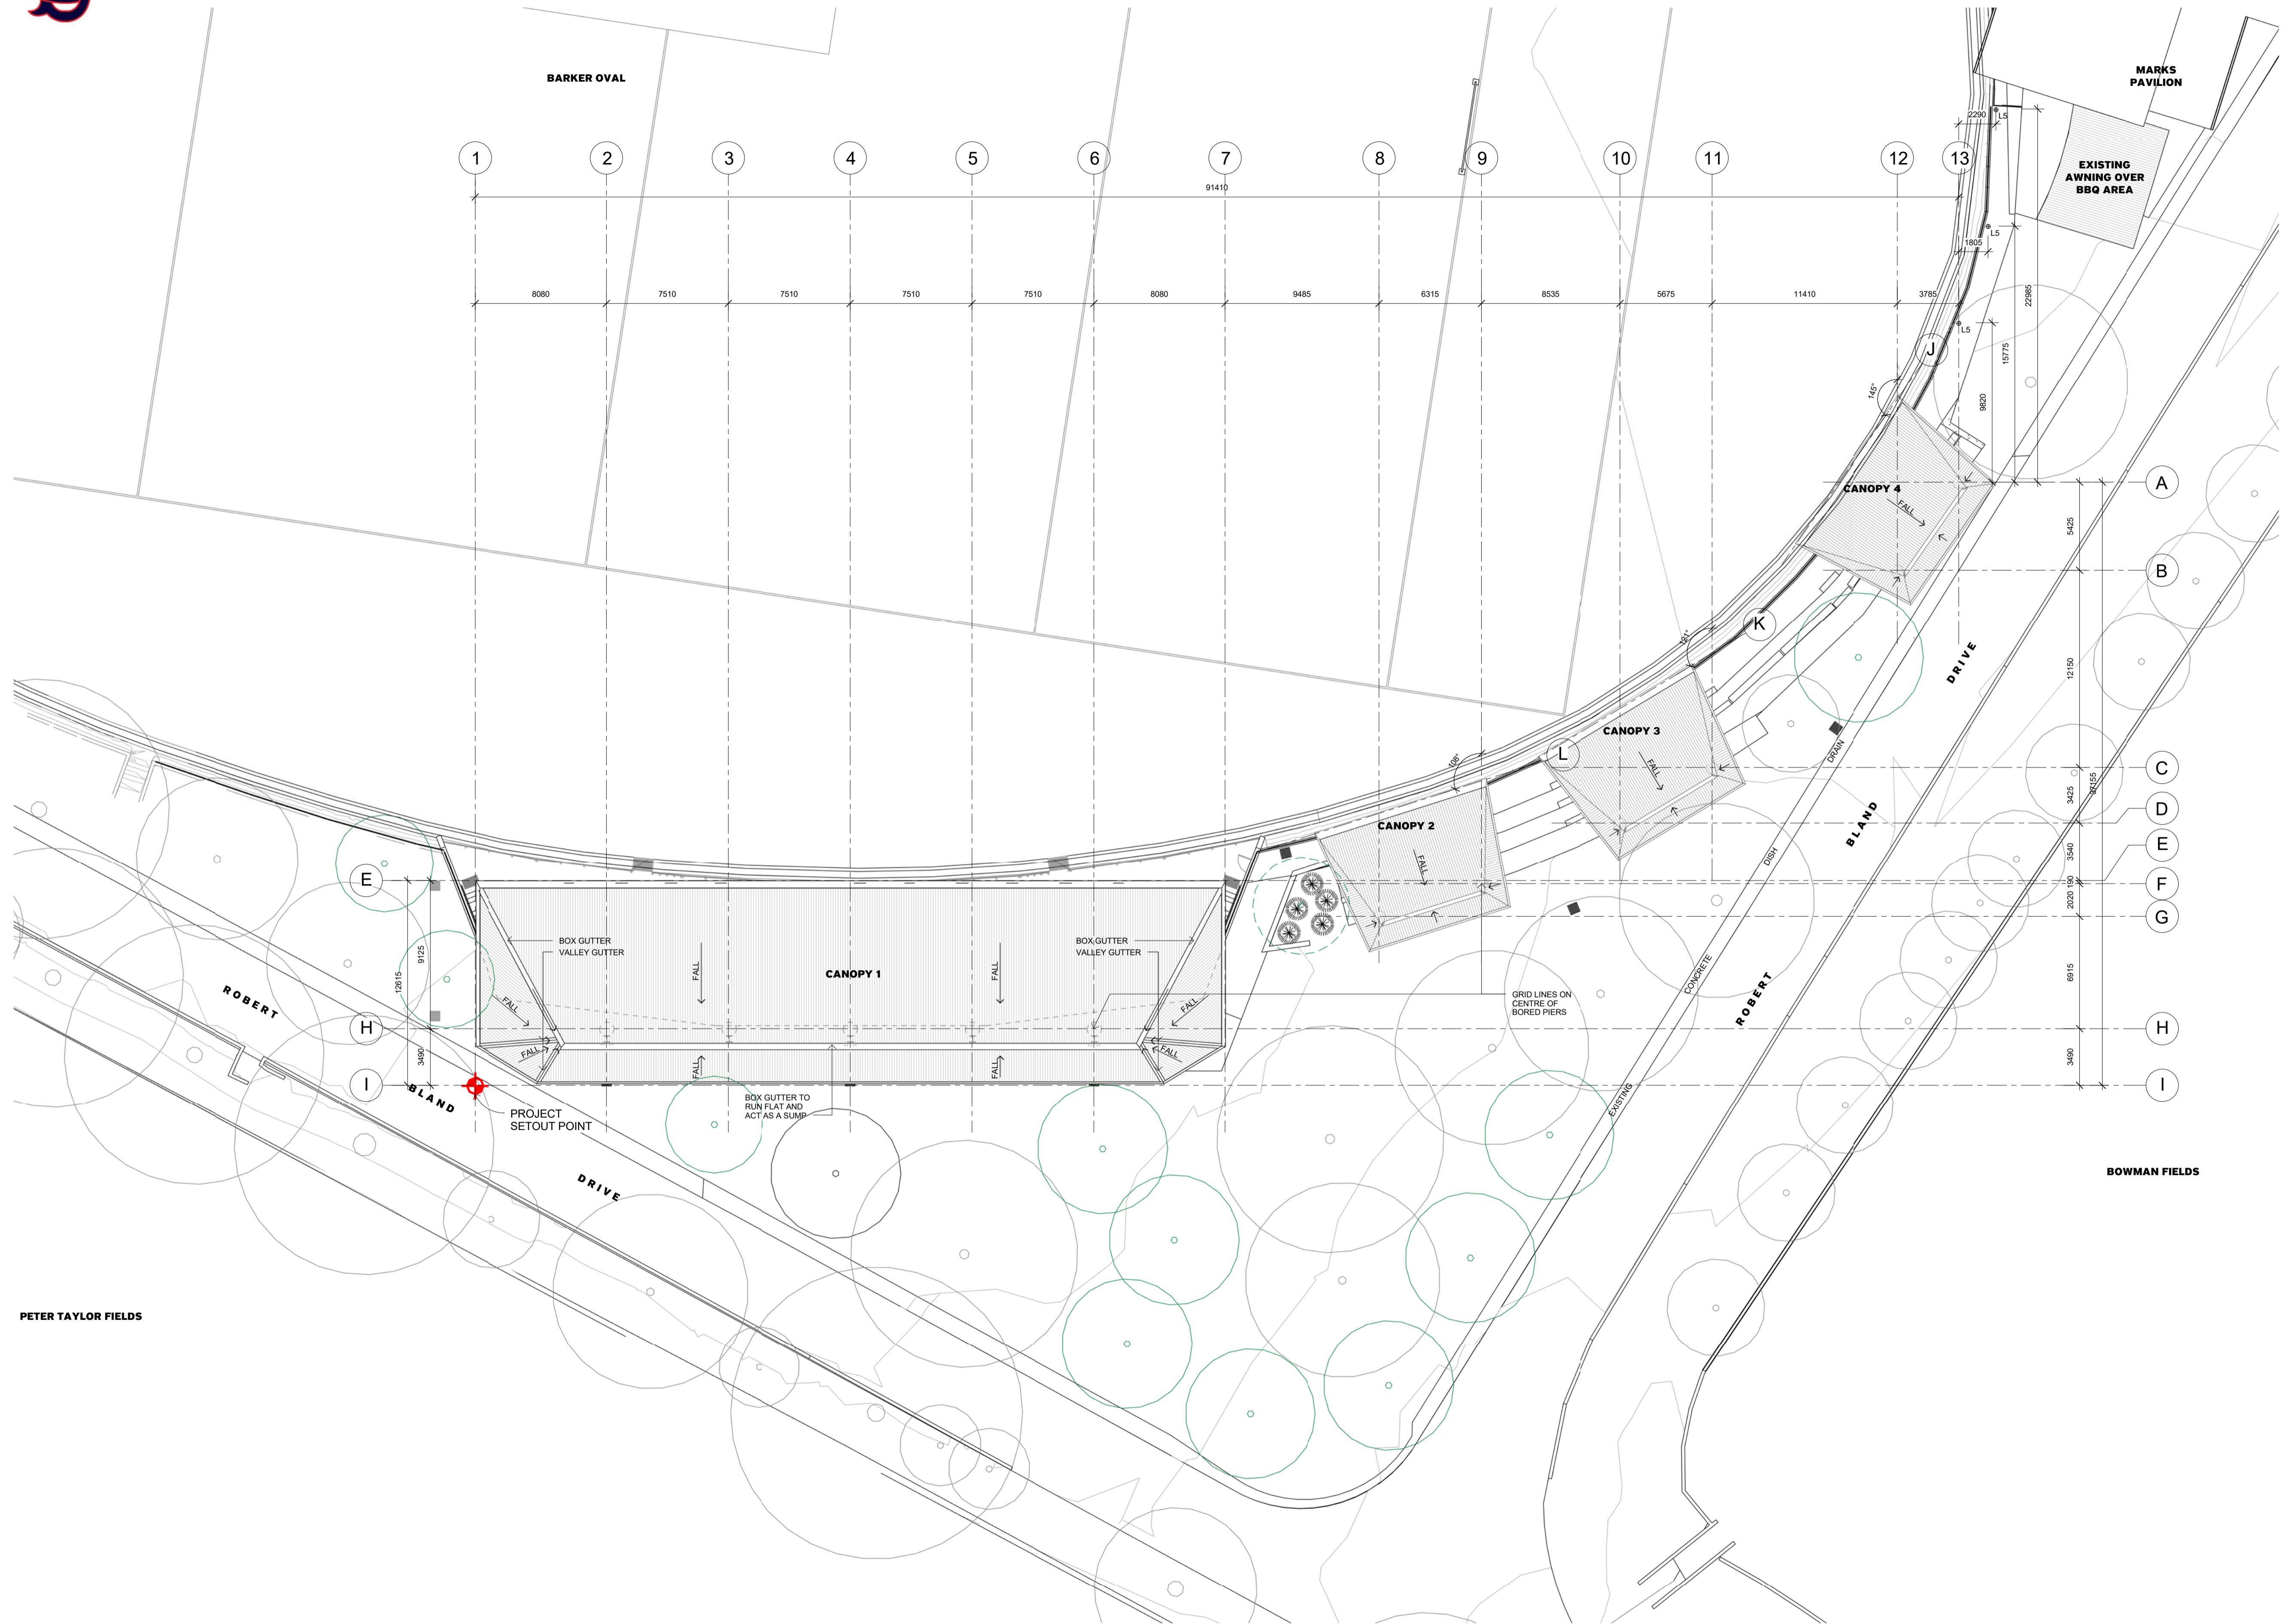

Issue	No.	Date	Description
	A	31/08/16	TENDER ISSUE

Electrical Engineer
Ken Offord
601/90 George St, Hornsby, NSW
T: + 61 2 9477 4300 F: 61 2 xx
E: ken@kroanda.com.au

Hydraulic Engineer
Sparks+Partners Consulting Engineers
Level 1, 91 George Street, Parramatta NSW 2121
T: 0401 803 330 **F:** 61 2 xxxx xx
E: Leon@sparksandpartners.com.au

Project Manager
Barker College
91 Pacific Highway, Hornsby, NSW, 2077
T: 02 9847 8318 **F:** 612 xxxx
E: georgina Rogers@barker.nsw.edu.au

Drawing Title
Site Roof Plan

Project & Client

BARKER OVAL C.O.L.A & AMENITIES UPGRADE

at

91 Pacific Hwy, Hornsby, NSW, 2077

for



BARKER COLLEGE

Date 31/08/2016 5:36:42 PM
Scale 1 : 200 @ A1

Drawing Reference
15494 - WD 011 - A



NOTE: REFER TO LANDSCAPE DRAWINGS

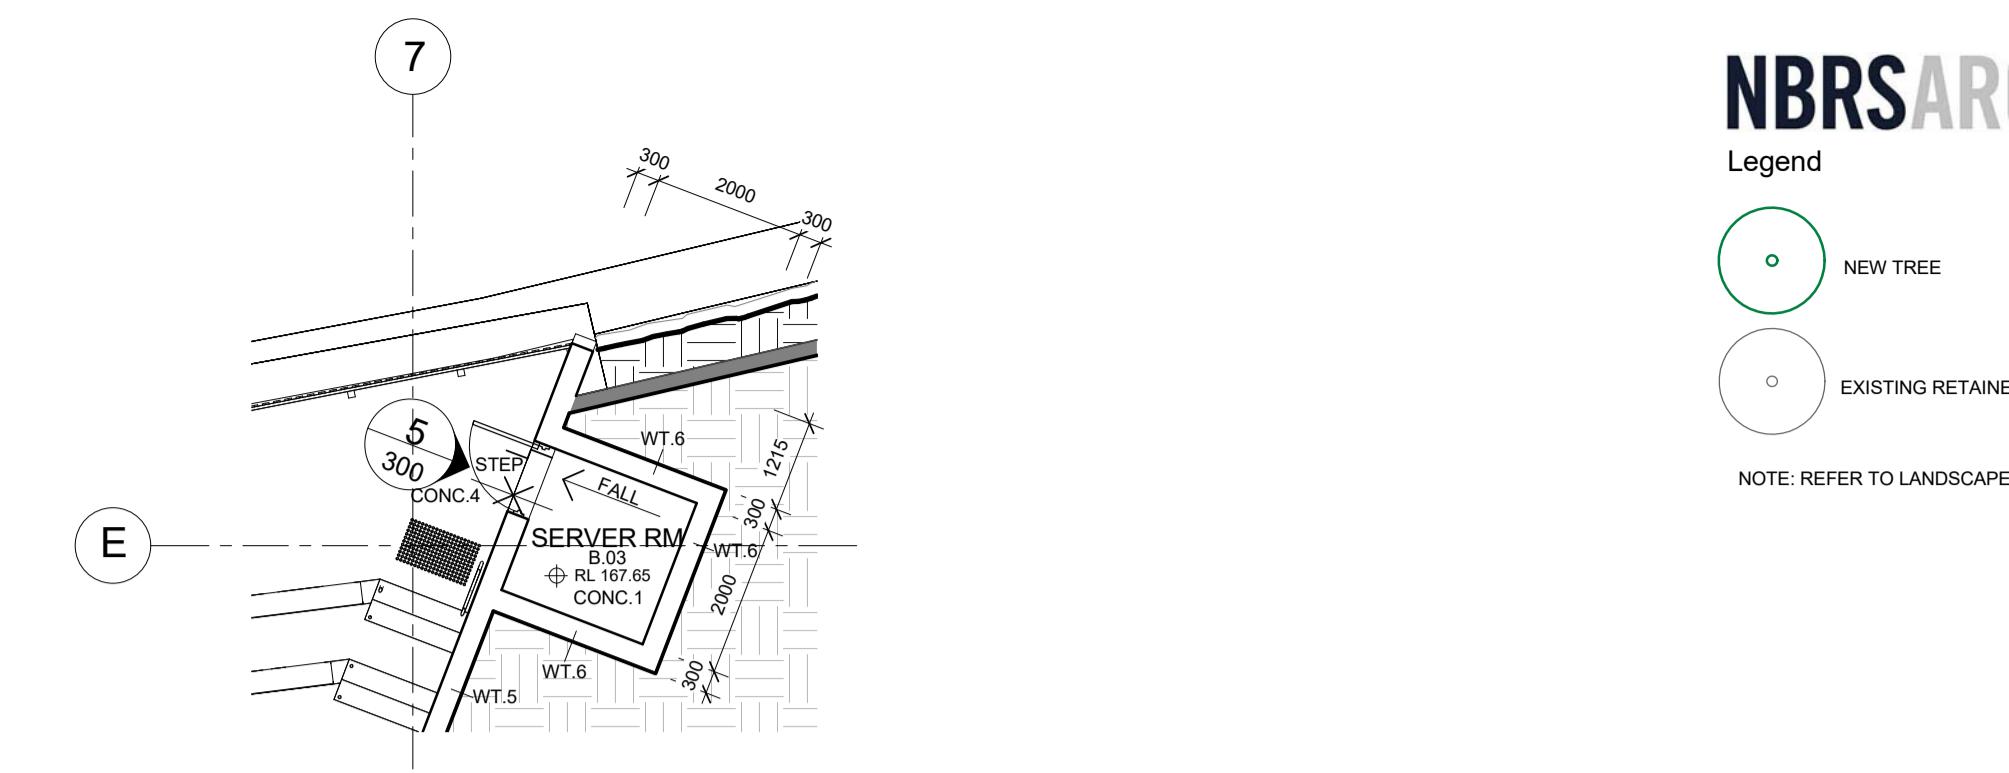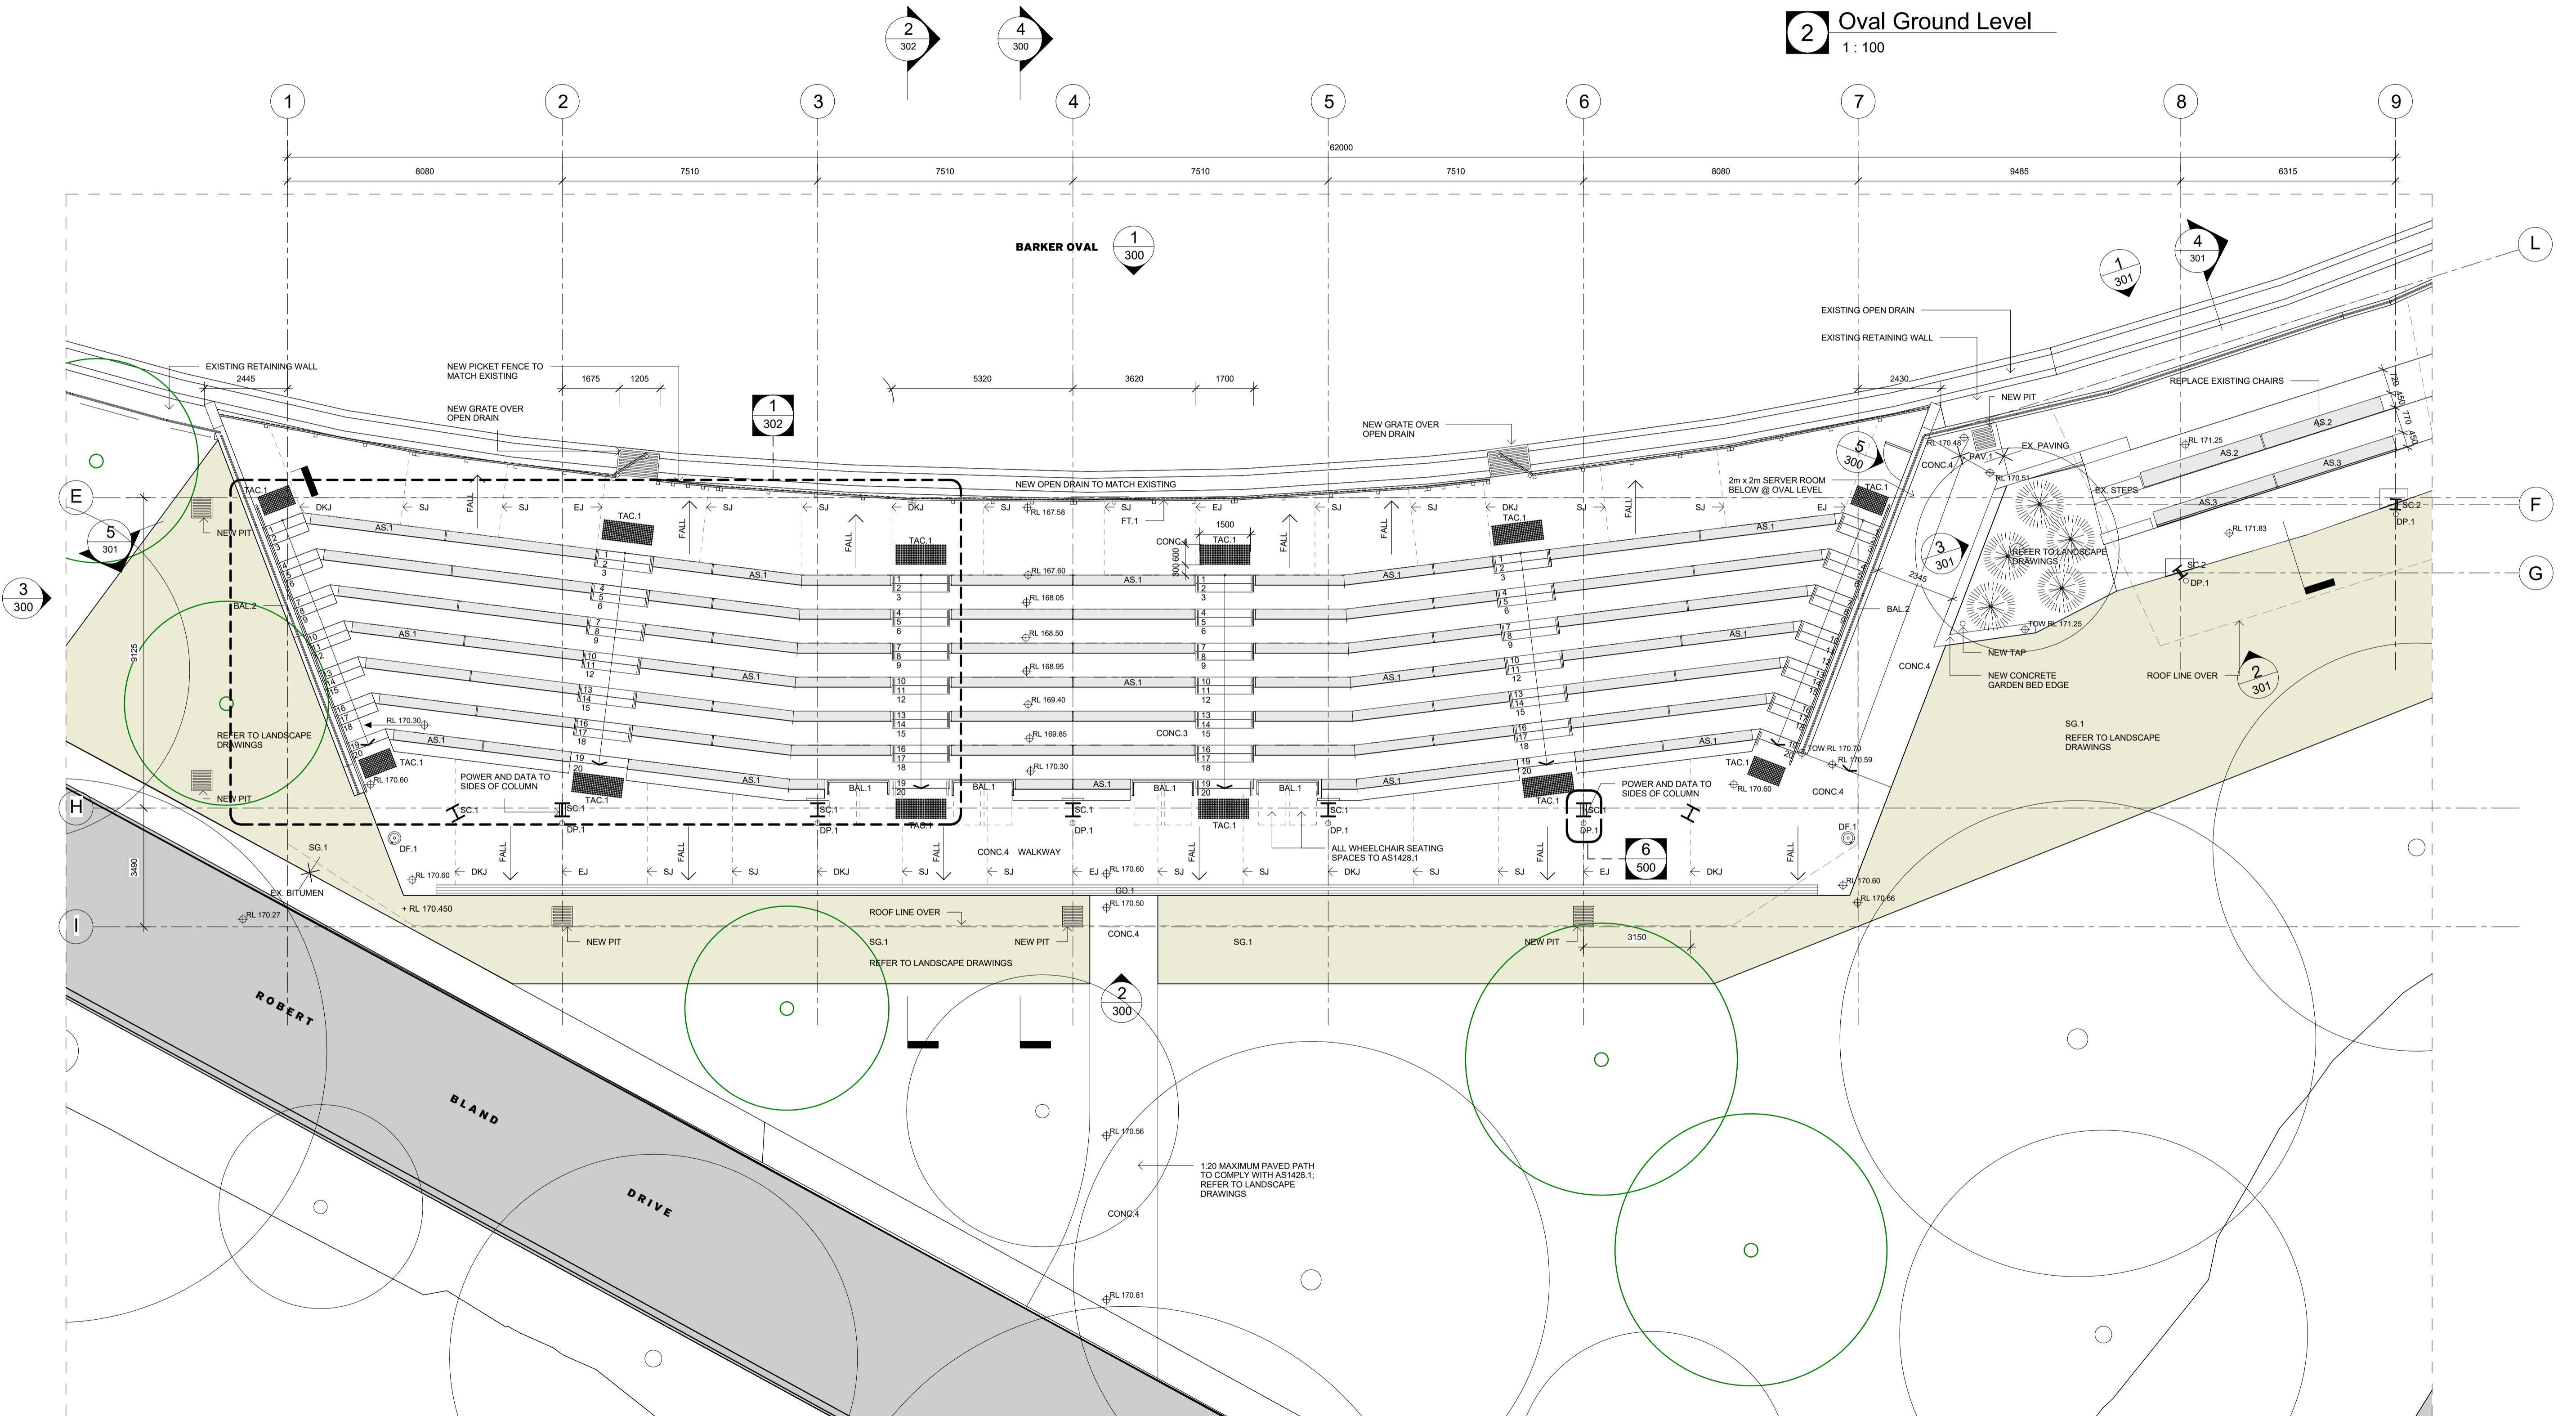2 Oval Ground Level
1 : 100

Issue No. Date 31/08/16 Description TENDER ISSUE Chkd AT

TENDER ISSUE

Electrical Engineer
Ken Offord
601/80 George St, Hornsby, NSW
T: +61 2 9477 4300 F: 612 xxxx xxxx
E: ken@kroanda.com.au

Hydraulic Engineer
Sparks+Partners Consulting Engineers
Level 1, 91 George Street, Parramatta NSW
T: 0401 803 330 F: 612 xxxx xxxx
E: Leon@sparksandpartners.com.au

Project Manager
Barker College
91 Pacific Highway, Hornsby, NSW, 2077
T: 02 9647 8318 F: 612 xxxx xxxx
E: georgina_rogers@barker.nsw.edu.au

Drawing Title

Floor Plan - Canopy 1

Project & Client
BARKER OVAL C.O.L.A & AMENITIES UPGRADE
at 91 Pacific Hwy, Hornsby, NSW, 2077
for **BARKER COLLEGE**

Architect
NBRSArchitecture.
Sydney 612 9922 2344 Melbourne 613 8676 0427
nbrsarchitecture.com.au
Any form of replication of this drawing in full or in part without the written permission of NBRSA+PARTNERS Pty Ltd constitutes an infringement of the copyright
ABN 16 003 247 365 © 2016
Nominated Architects: Geoffrey Deane 3766; Andrew Duffin 5602; Garry Hodnett 5286

Date 31/08/2016 5:37:20 PM
Scale As indicated @ A1

0 1m 2m 3m 4m 5m 6m

Drawing Reference


15494-WD 100 -A



Legend

- NEW TREE** (Green circle)
- EXISTING RETAINED TREE** (Grey circle)

NOTE: REFER TO LANDSCAPE DRAWINGS

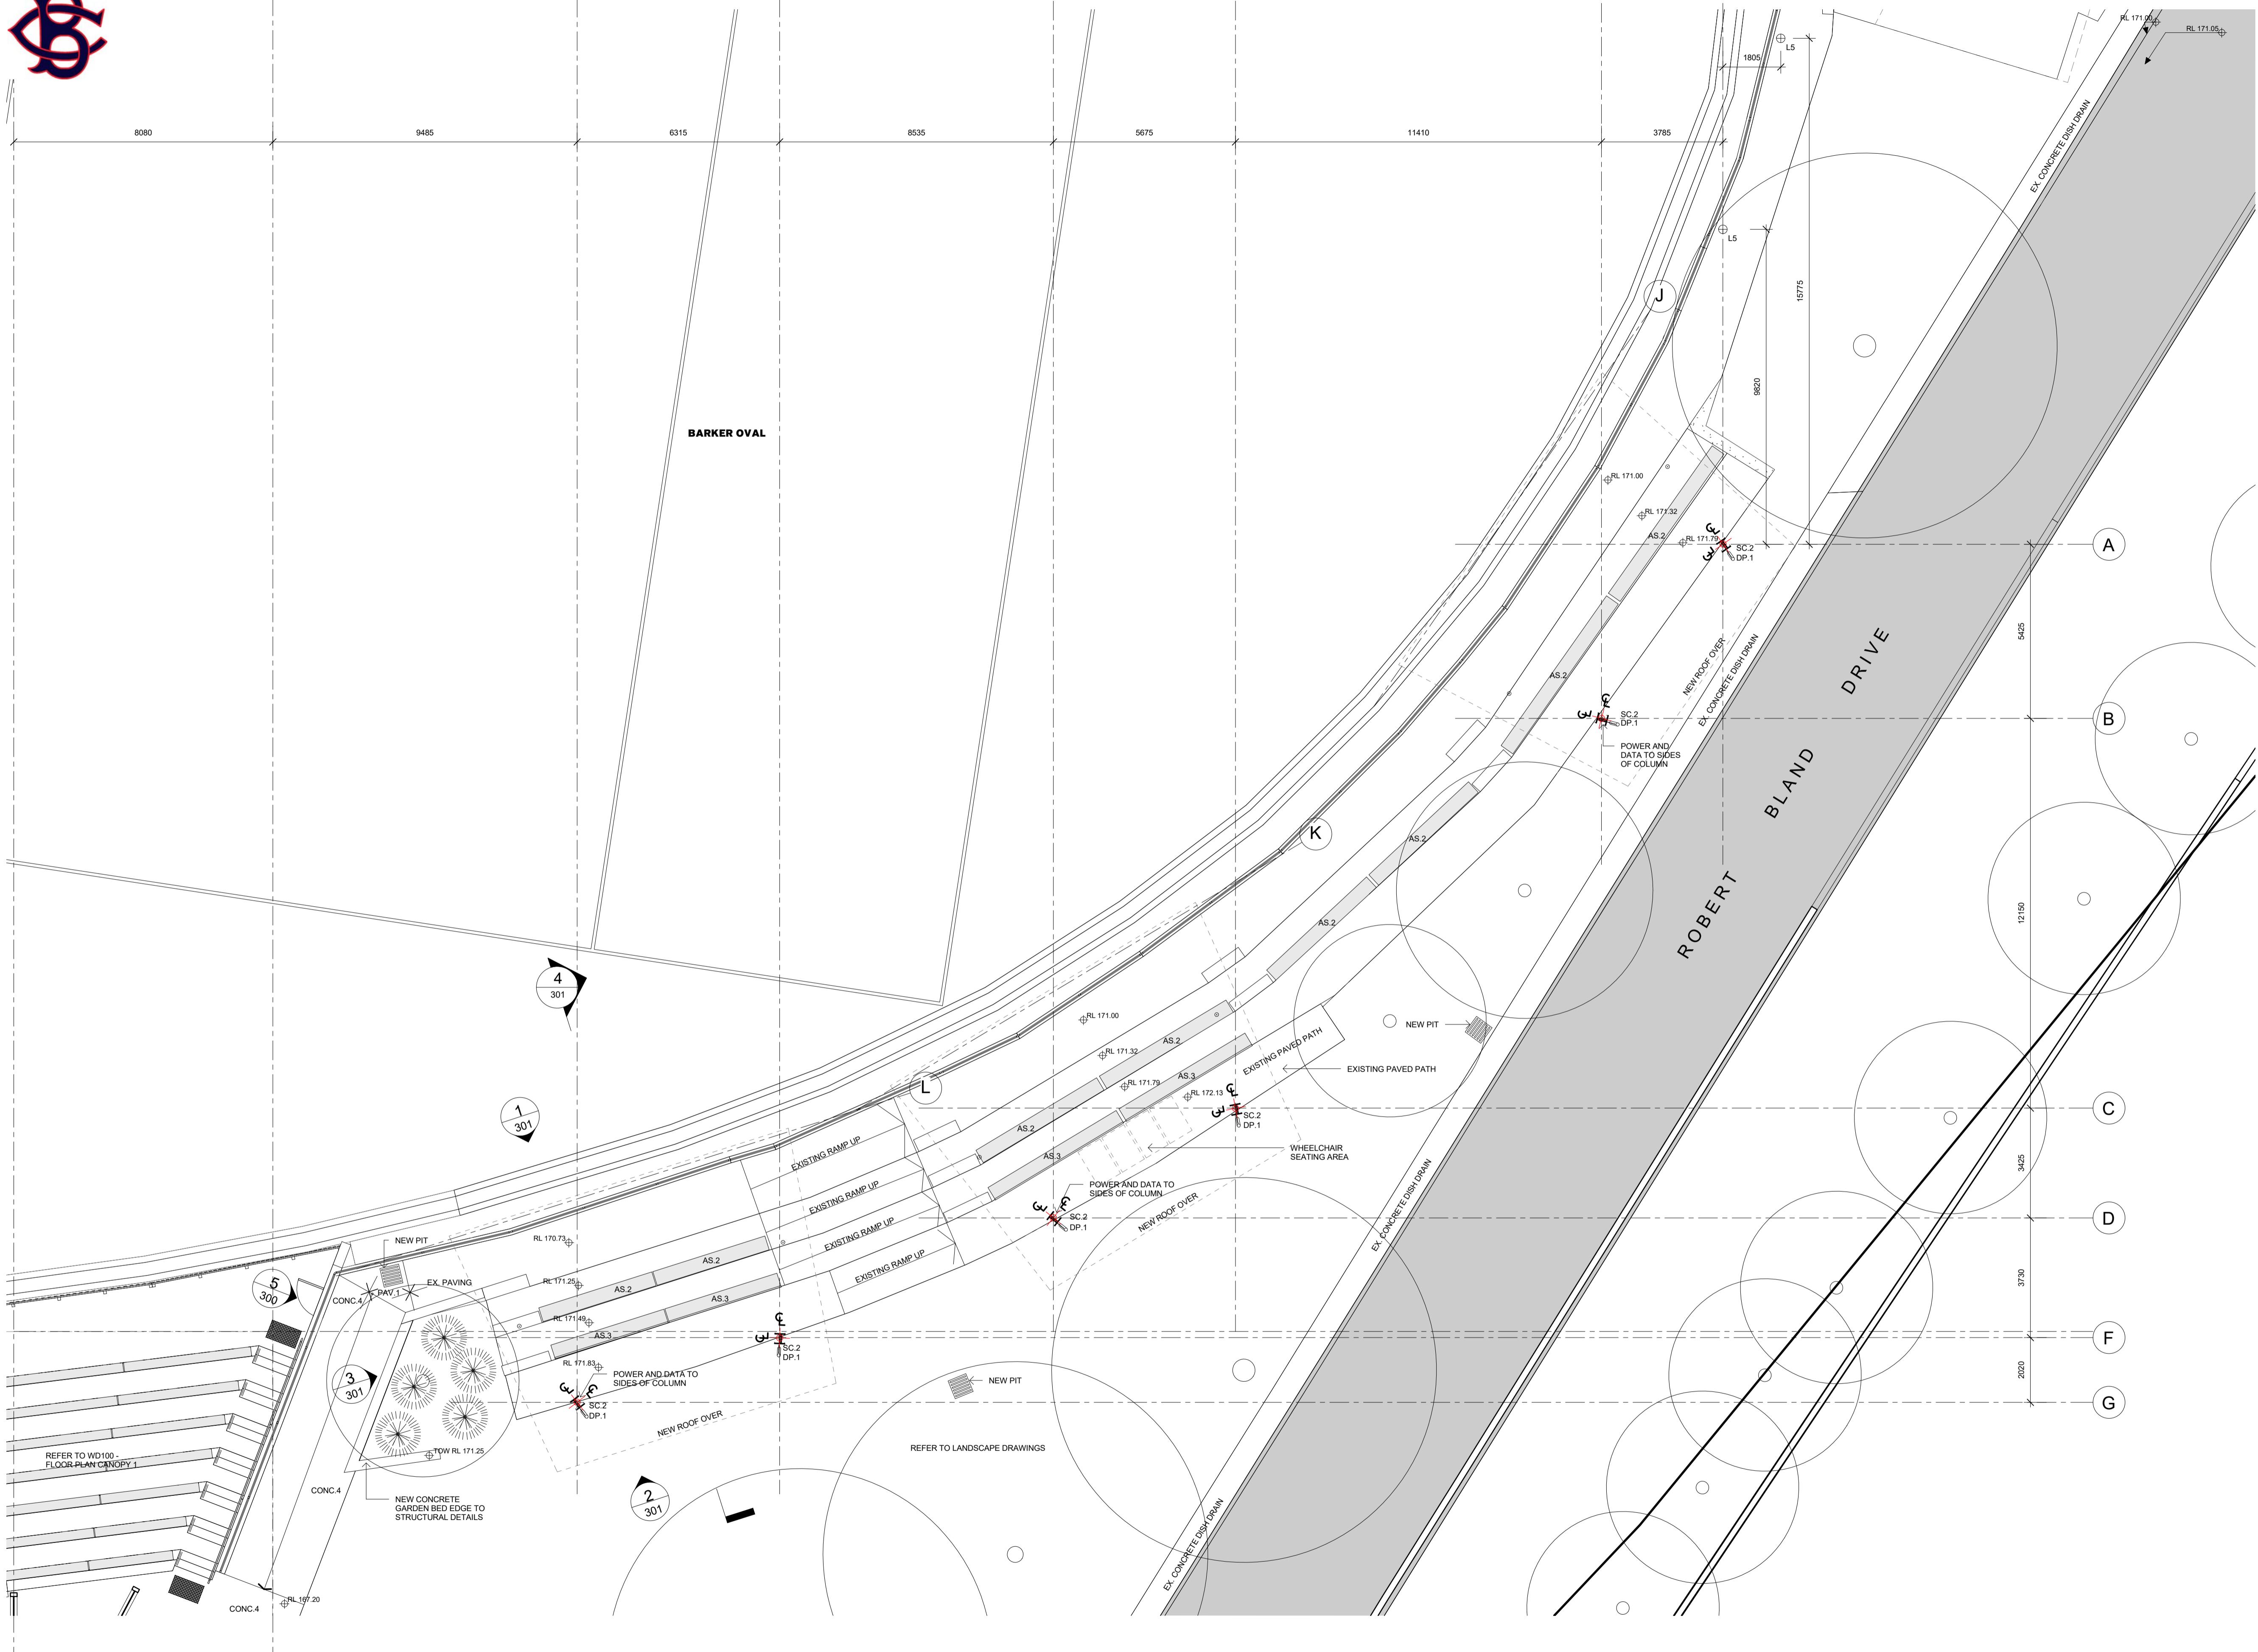

Issue No. Date Description Chkd AT
A 31/08/16 TENDER ISSUE AT

TENDER ISSUE

Electrical Engineer
Ken Offord
601/80 George St, Hornsby, NSW
T: +61 2 9477 4300 F: 612 xxxx xxxx
E: ken@kroanda.com.au

Hydraulic Engineer
Sparks+Partners Consulting Engineers
Level 1, 91 George Street, Parramatta NSW
T: 0401 803 330 F: 612 xxxx xxxx
E: Leon@sparksandpartners.com.au

Project Manager
Barker College
91 Pacific Highway, Hornsby, NSW, 2077
T: 02 9647 8318 F: 612 xxxx xxxx
E: georgina_rogers@barker.nsw.edu.au

Drawing Title
Floor Plan - Canopy 2, 3 & 4

Project & Client
BARKER OVAL C.O.L.A & AMENITIES UPGRADE
at 91 Pacific Hwy, Hornsby, NSW, 2077
for **BARKER COLLEGE**

Architect
NBRSArchitecture.
Sydney 612 9922 2344 Melbourne 613 8676 0427
nbrsarchitecture.com.au



Any form of replication of this drawing in full or in part without the written permission of NBRSA+PARTNERS Pty Ltd constitutes an infringement of the copyright
ABN 16 003 247 365 © 2016
Nominated Architects: Geoffrey Deane 3766; Andrew Duffin 5602; Garry Hodnett 5286

Date 31/08/2016 5:37:46 PM
Scale As indicated @ A1
0 1m 2m 3m 4m 5m 6m

Drawing Reference
15494-WD 101-A



- NEW TREE
 - EXISTING RETAINED TREE
- NOTE: REFER TO LANDSCAPE DRAWINGS

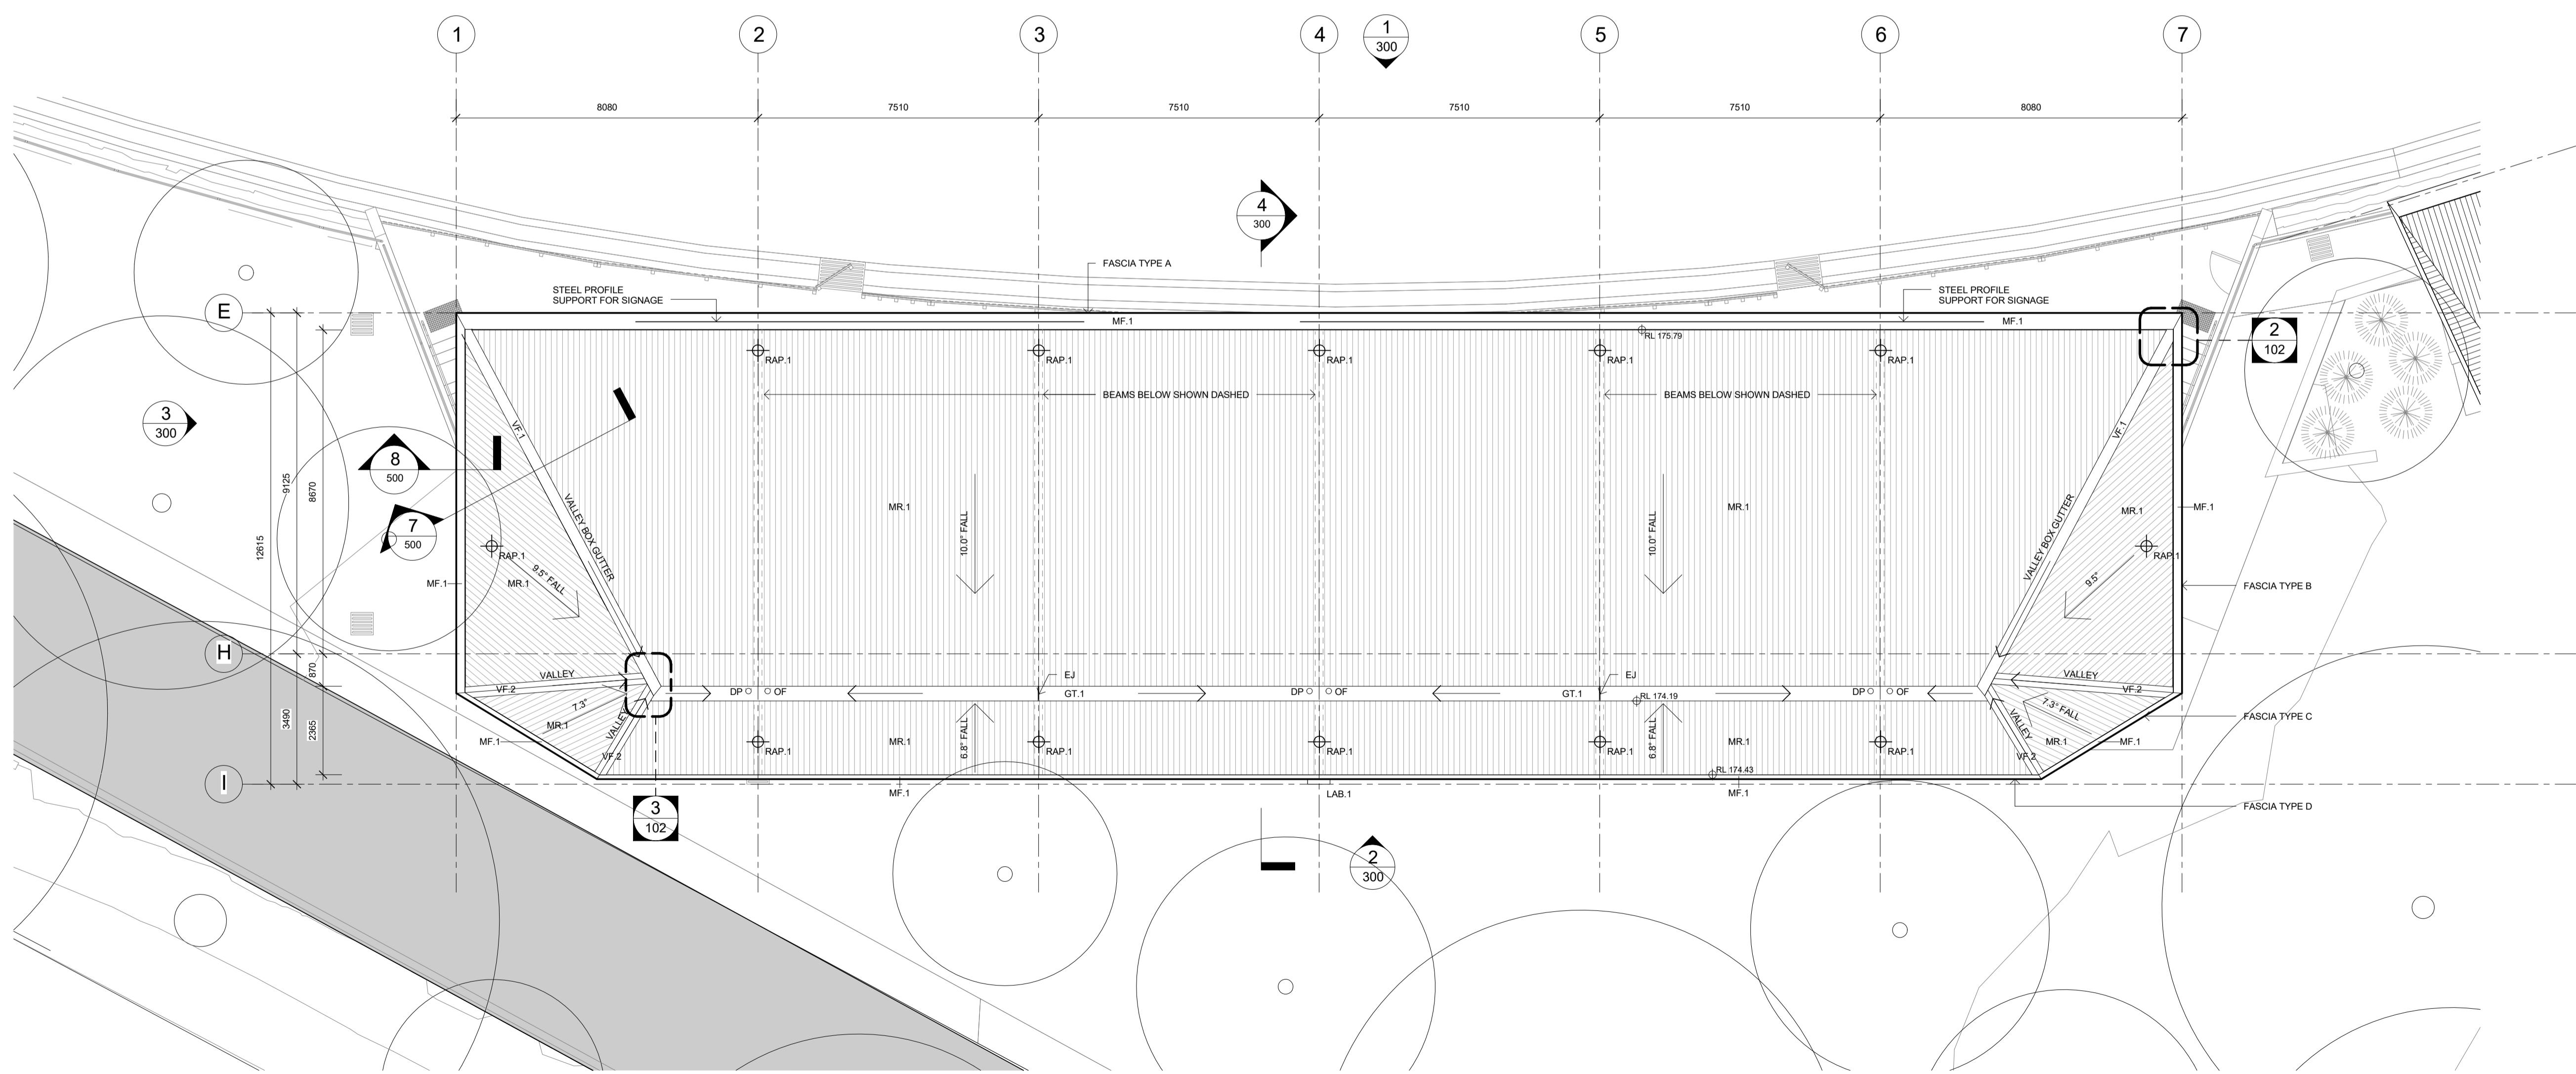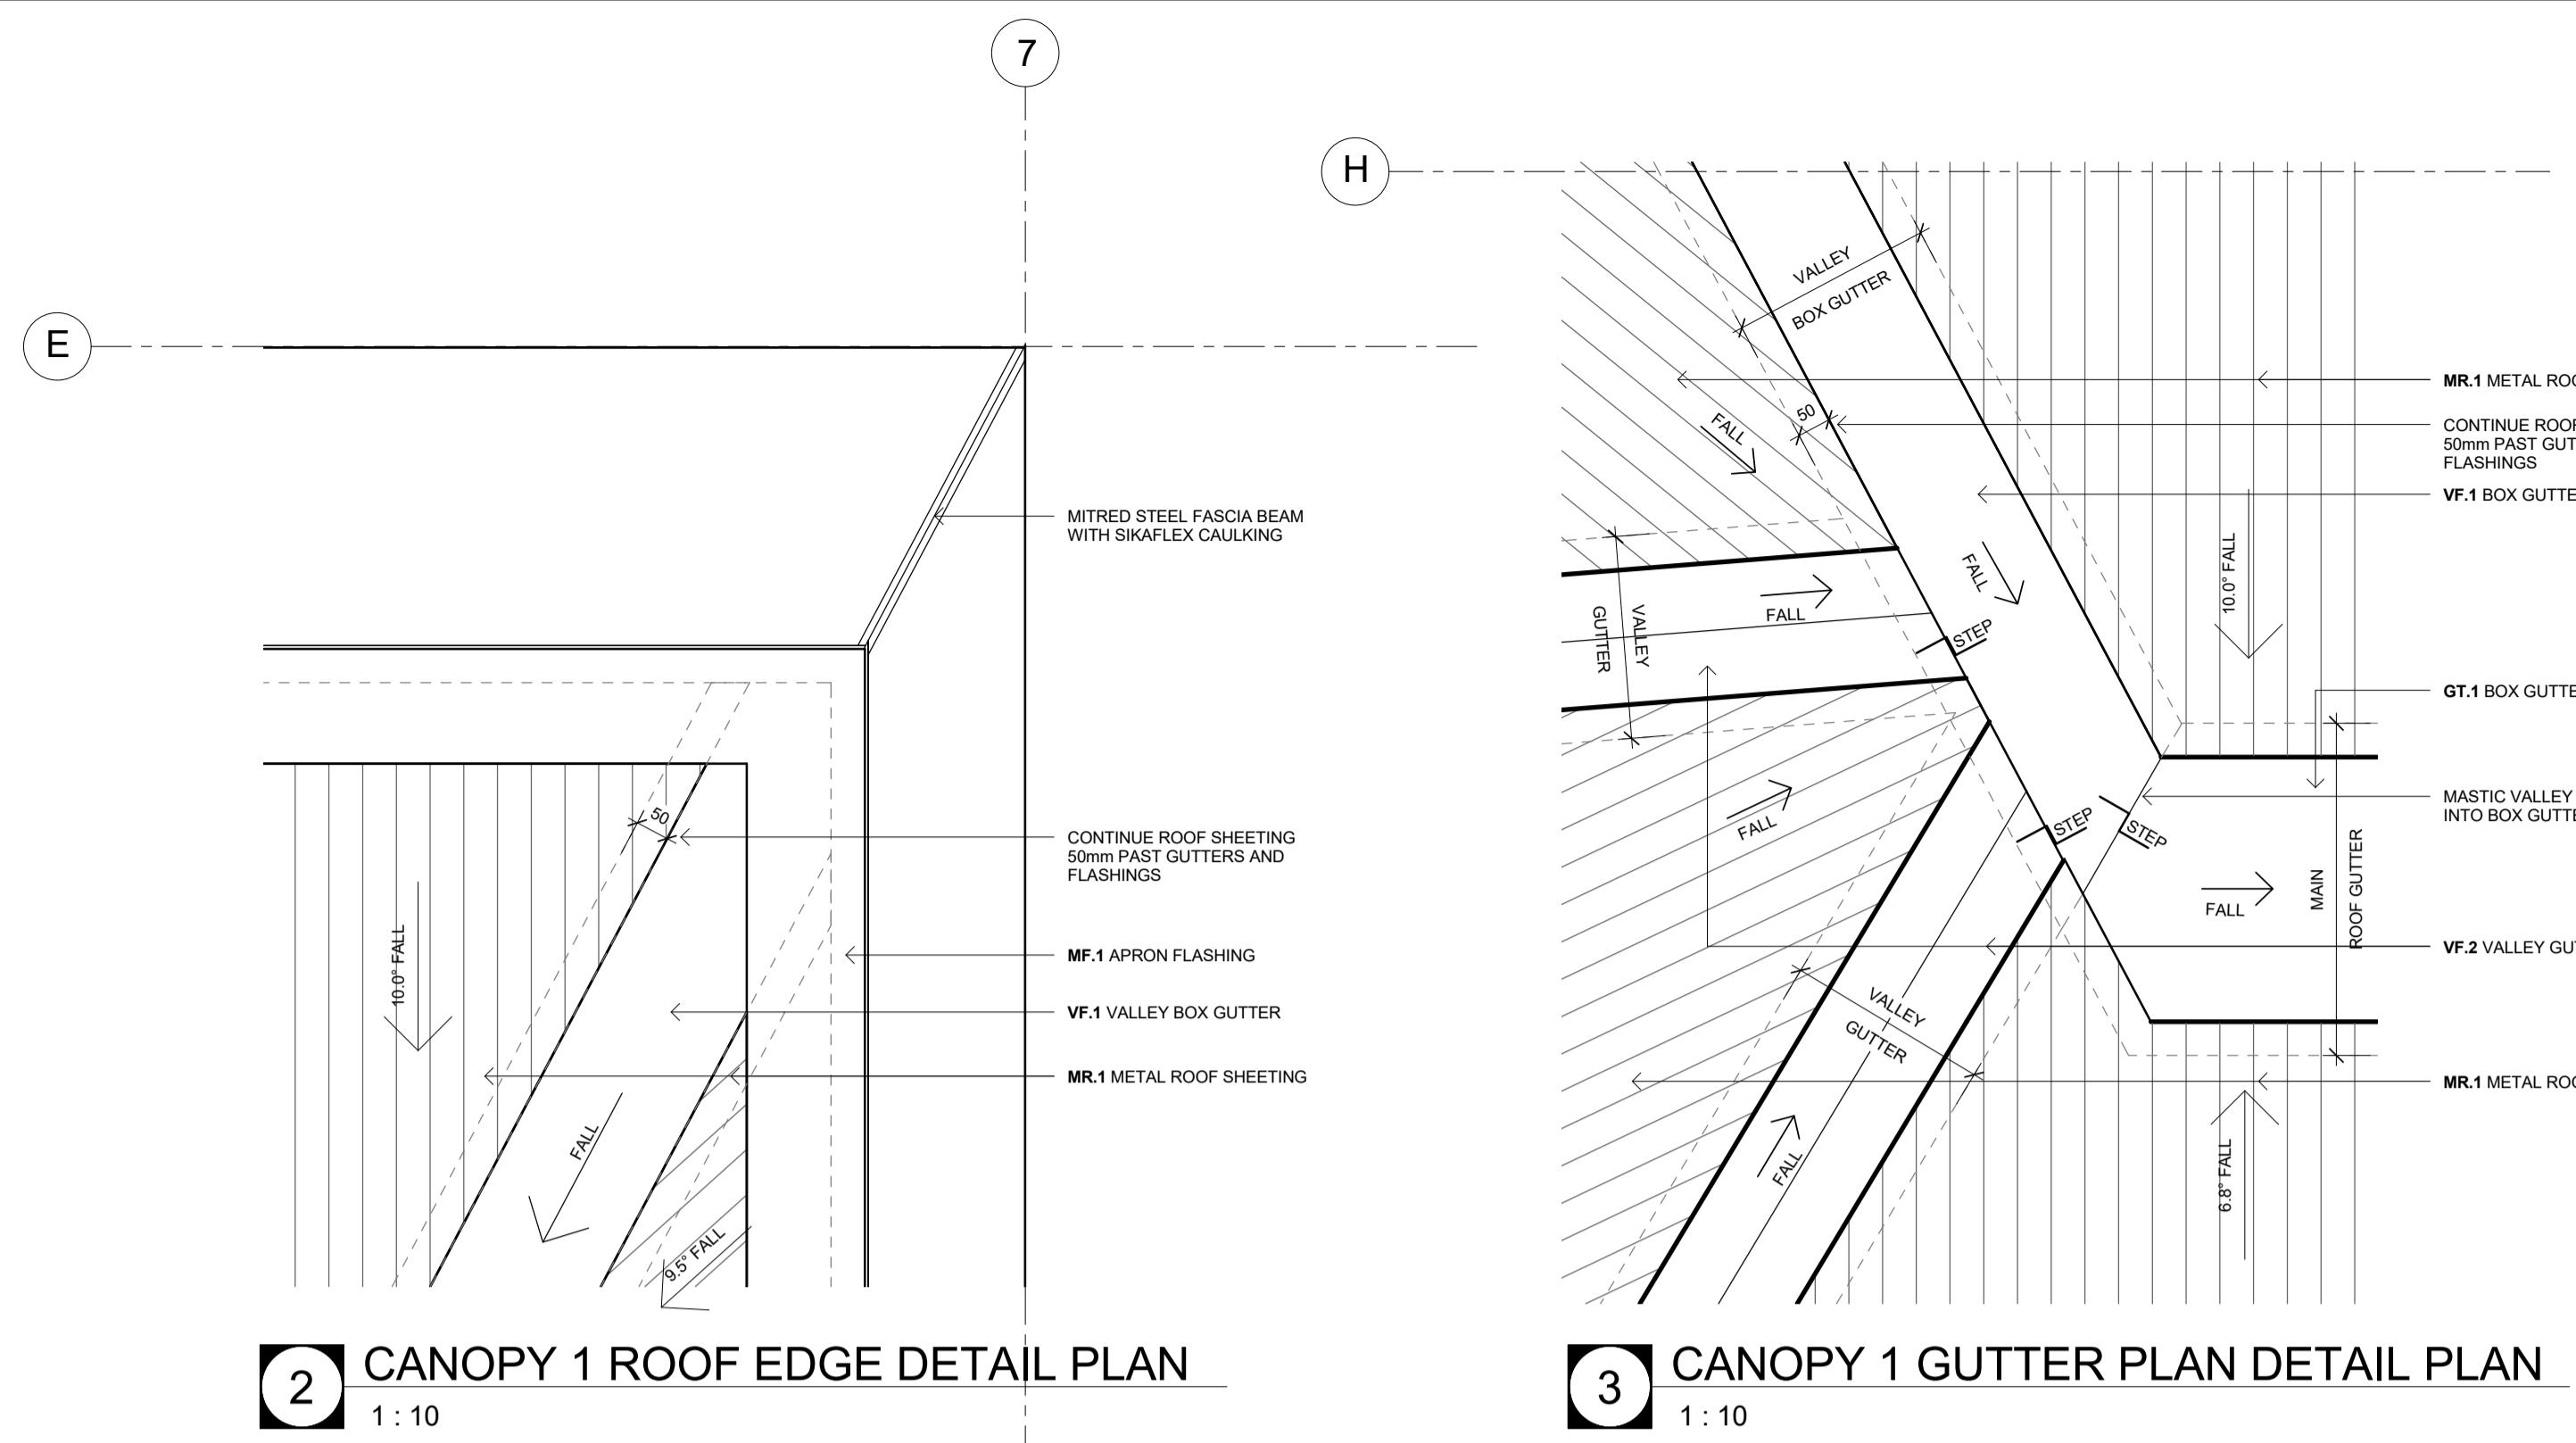

Issue No. Date 31/08/16 Description TENDER ISSUE Chkd AT

TENDER ISSUE

Electrical Engineer
Ken Offord
601/80 George St, Hornsby, NSW
T: +61 2 9477 4300 F: 612 xxxx xxxx
E: ken@kroanda.com.au

Hydraulic Engineer
Sparks+Partners Consulting Engineers
Level 1, 91 George Street, Parramatta NSW
T: 0401 803 330 F: 612 xxxx xxxx
E: leon@sparksandpartners.com.au

Project Manager
Barker College
91 Pacific Highway, Hornsby, NSW, 2077
T: 02 9647 8318 F: 612 xxxx xxxx
E: georgina_rogers@barker.nsw.edu.au

Structural Engineer
Birzulis Associates
583 Darling Street Rozelle NSW 2039
T: 612 9555 7230 F: 612 xxxx xxxx
E: mgrogan@birzulisassociates.com

Drawing Title
Roof Plan - Canopy 1

Project & Client
BARKER OVAL C.O.L.A & AMENITIES UPGRADE
at 91 Pacific Hwy, Hornsby, NSW, 2077
for **BARKER COLLEGE**

Architect
NBRSArchitecture.
Sydney 612 9922 2344 Melbourne 613 8676 0427
nbrsarchitecture.com.au

Any form of replication of this drawing in full or in part without the written permission of NBRSA+PARTNERS Pty Ltd constitutes an infringement of the copyright
ABN 16 003 247 365 © 2016
Nominated Architects: Geoffrey Deane 3766; Andrew Duffin 5602; Garry Hodnett 5286

Date 31/08/2016 5:37:53 PM
Scale As indicated @ A1
0 1m 2m 3m 4m 5m 6m

Drawing Reference
15494-WD 102 -A



Legend









NEW TREE



EXISTING RETAINED TREE

NOTE: REFER TO LANDSCAPE DRAWINGS

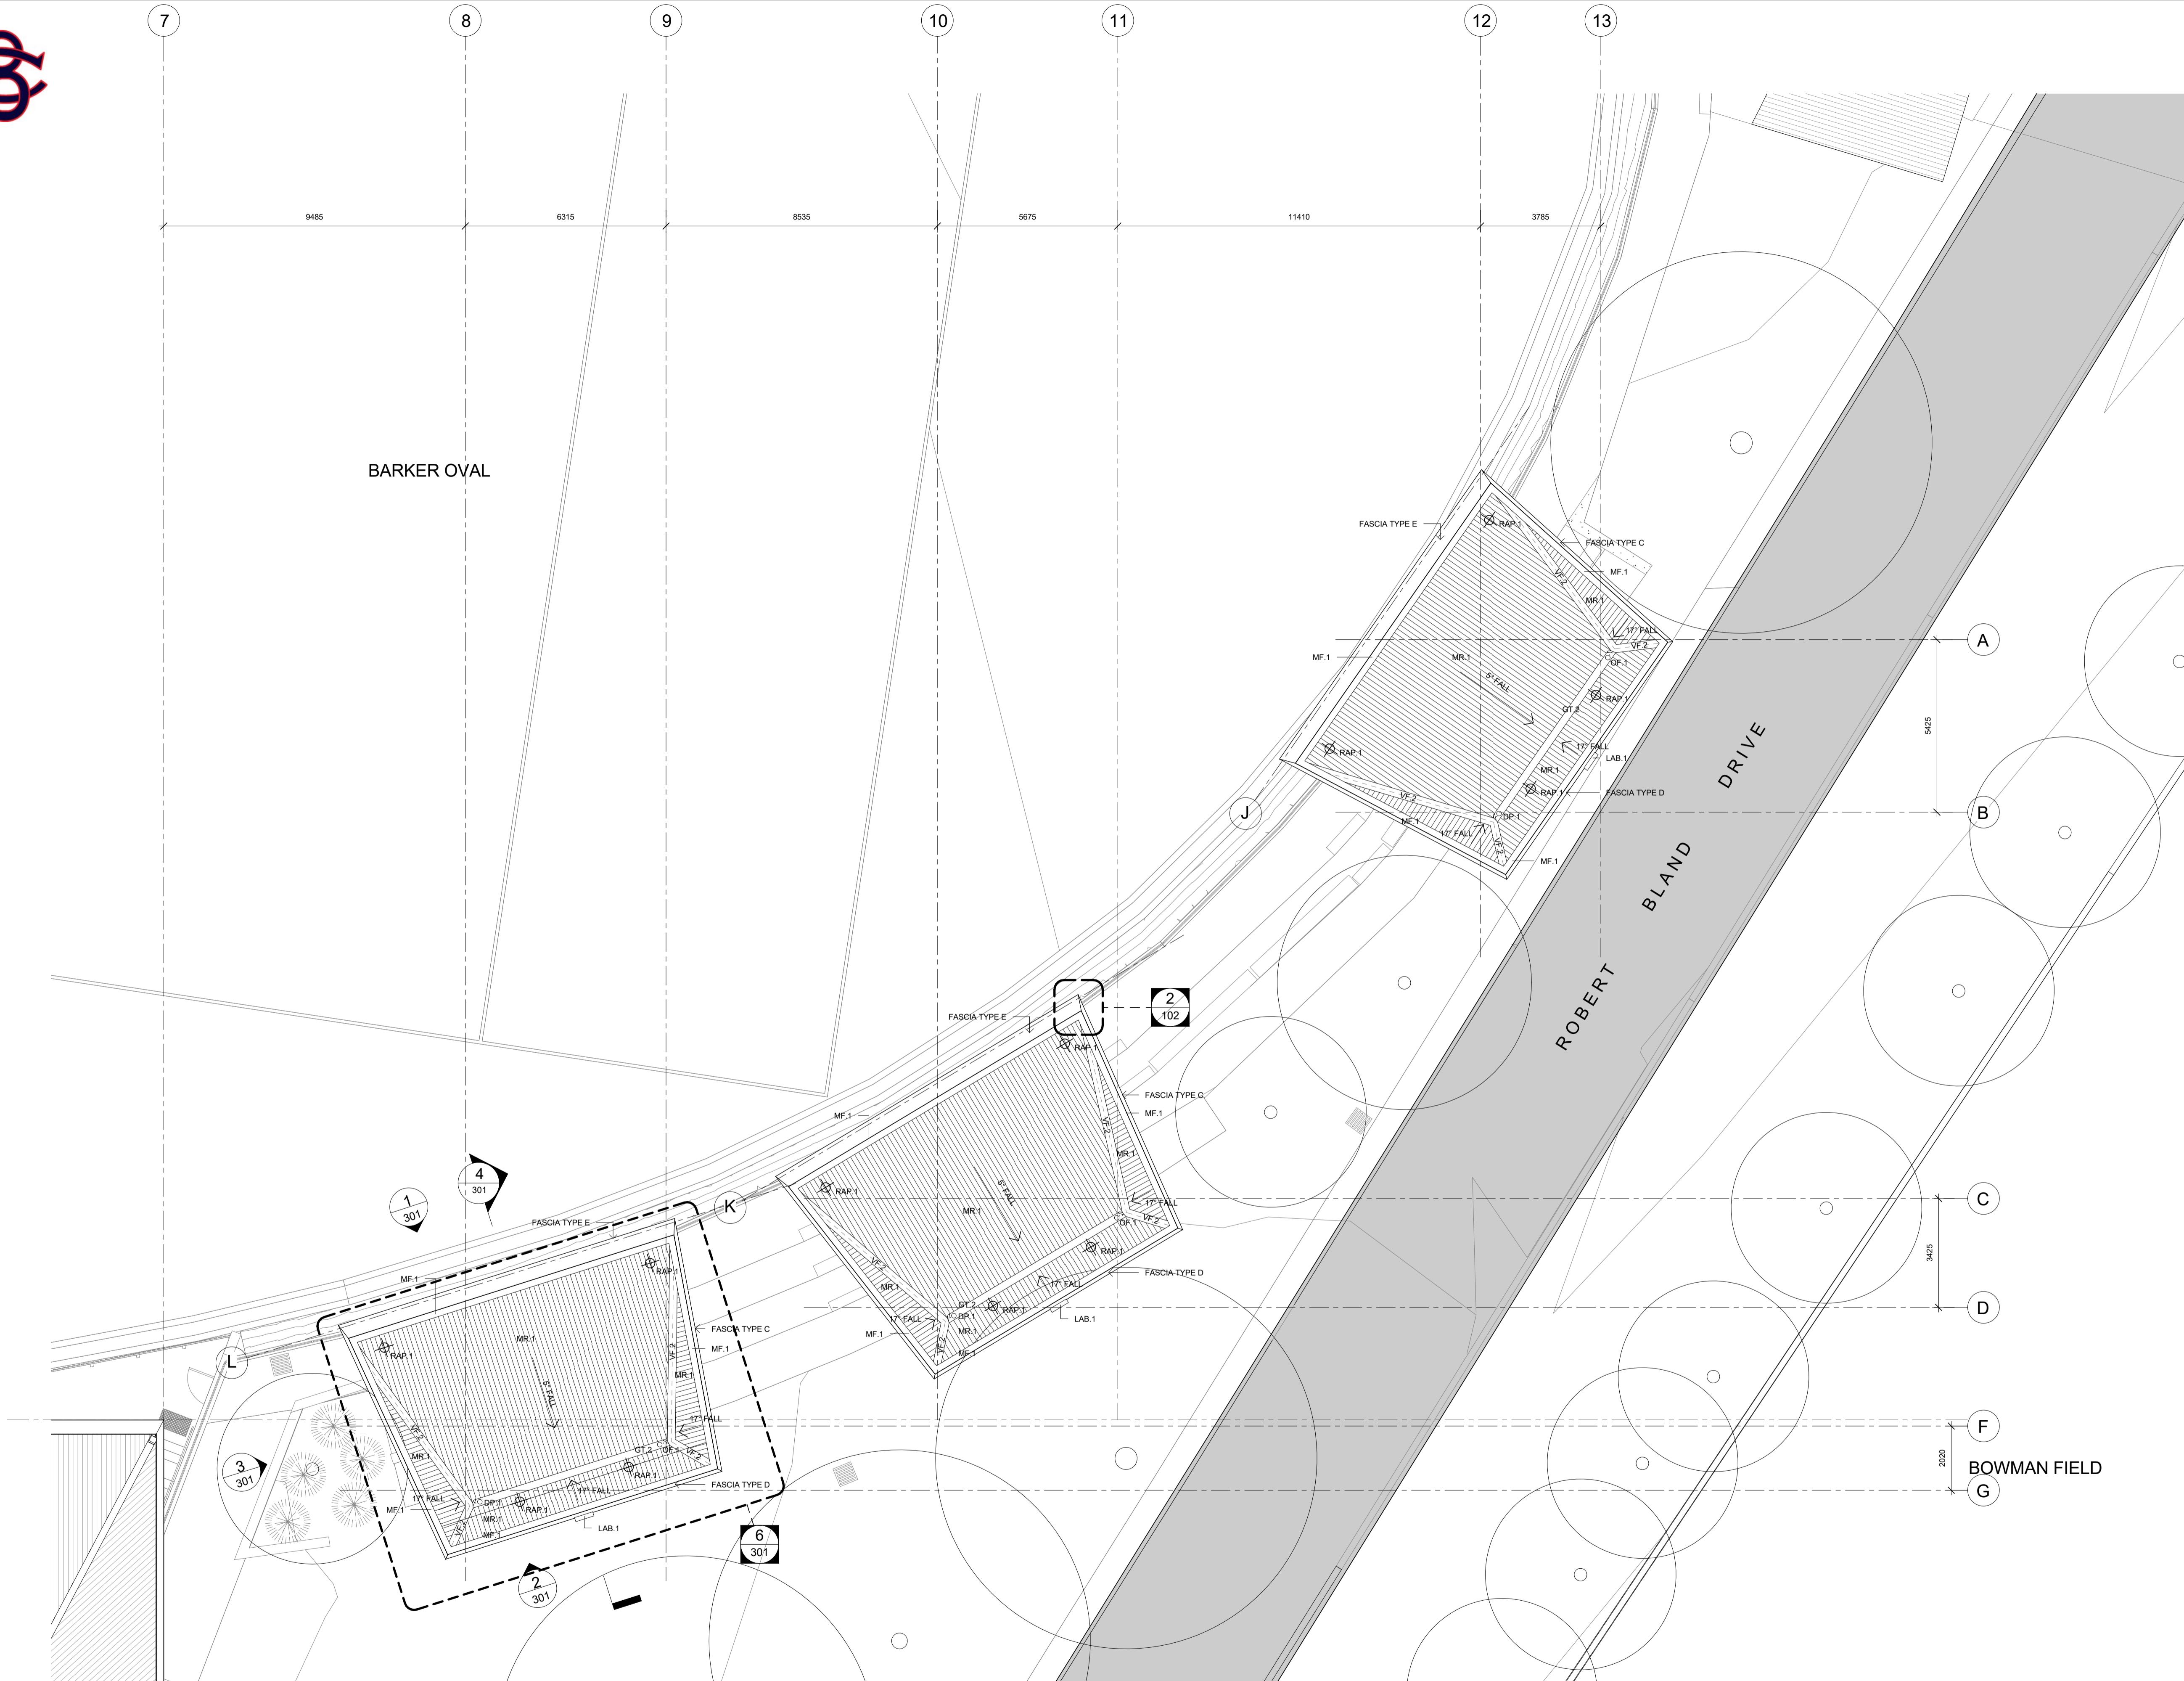

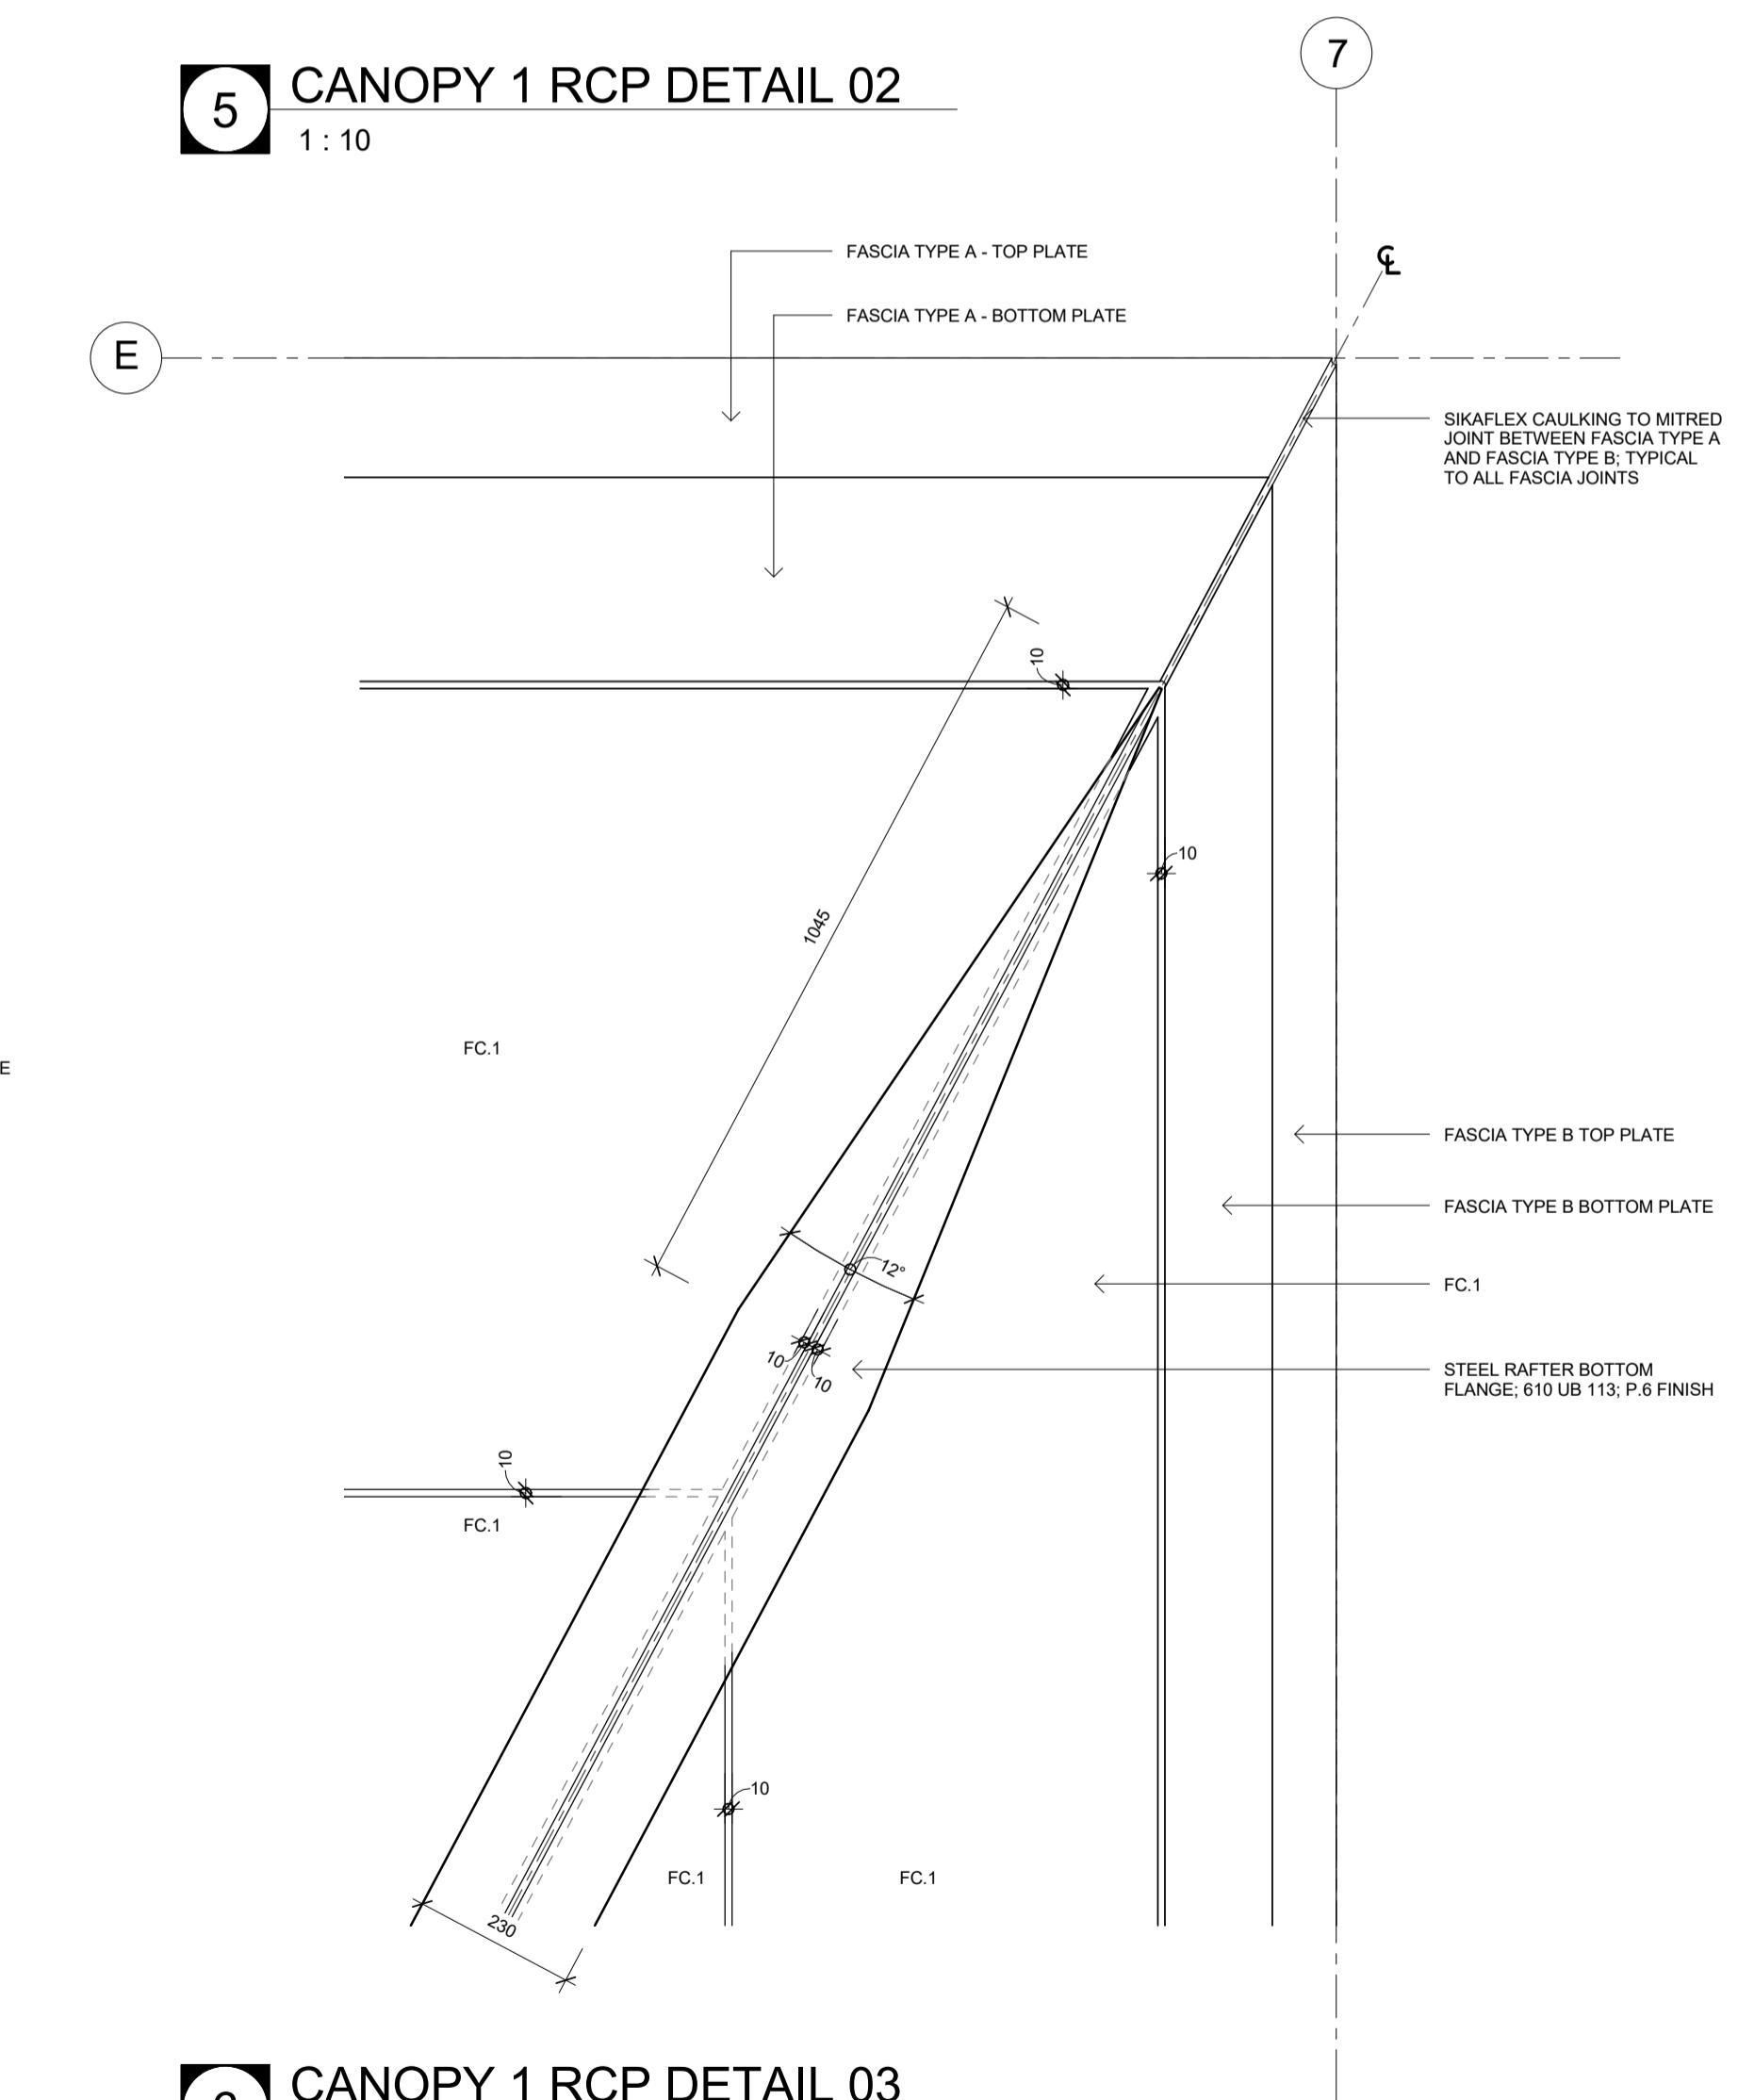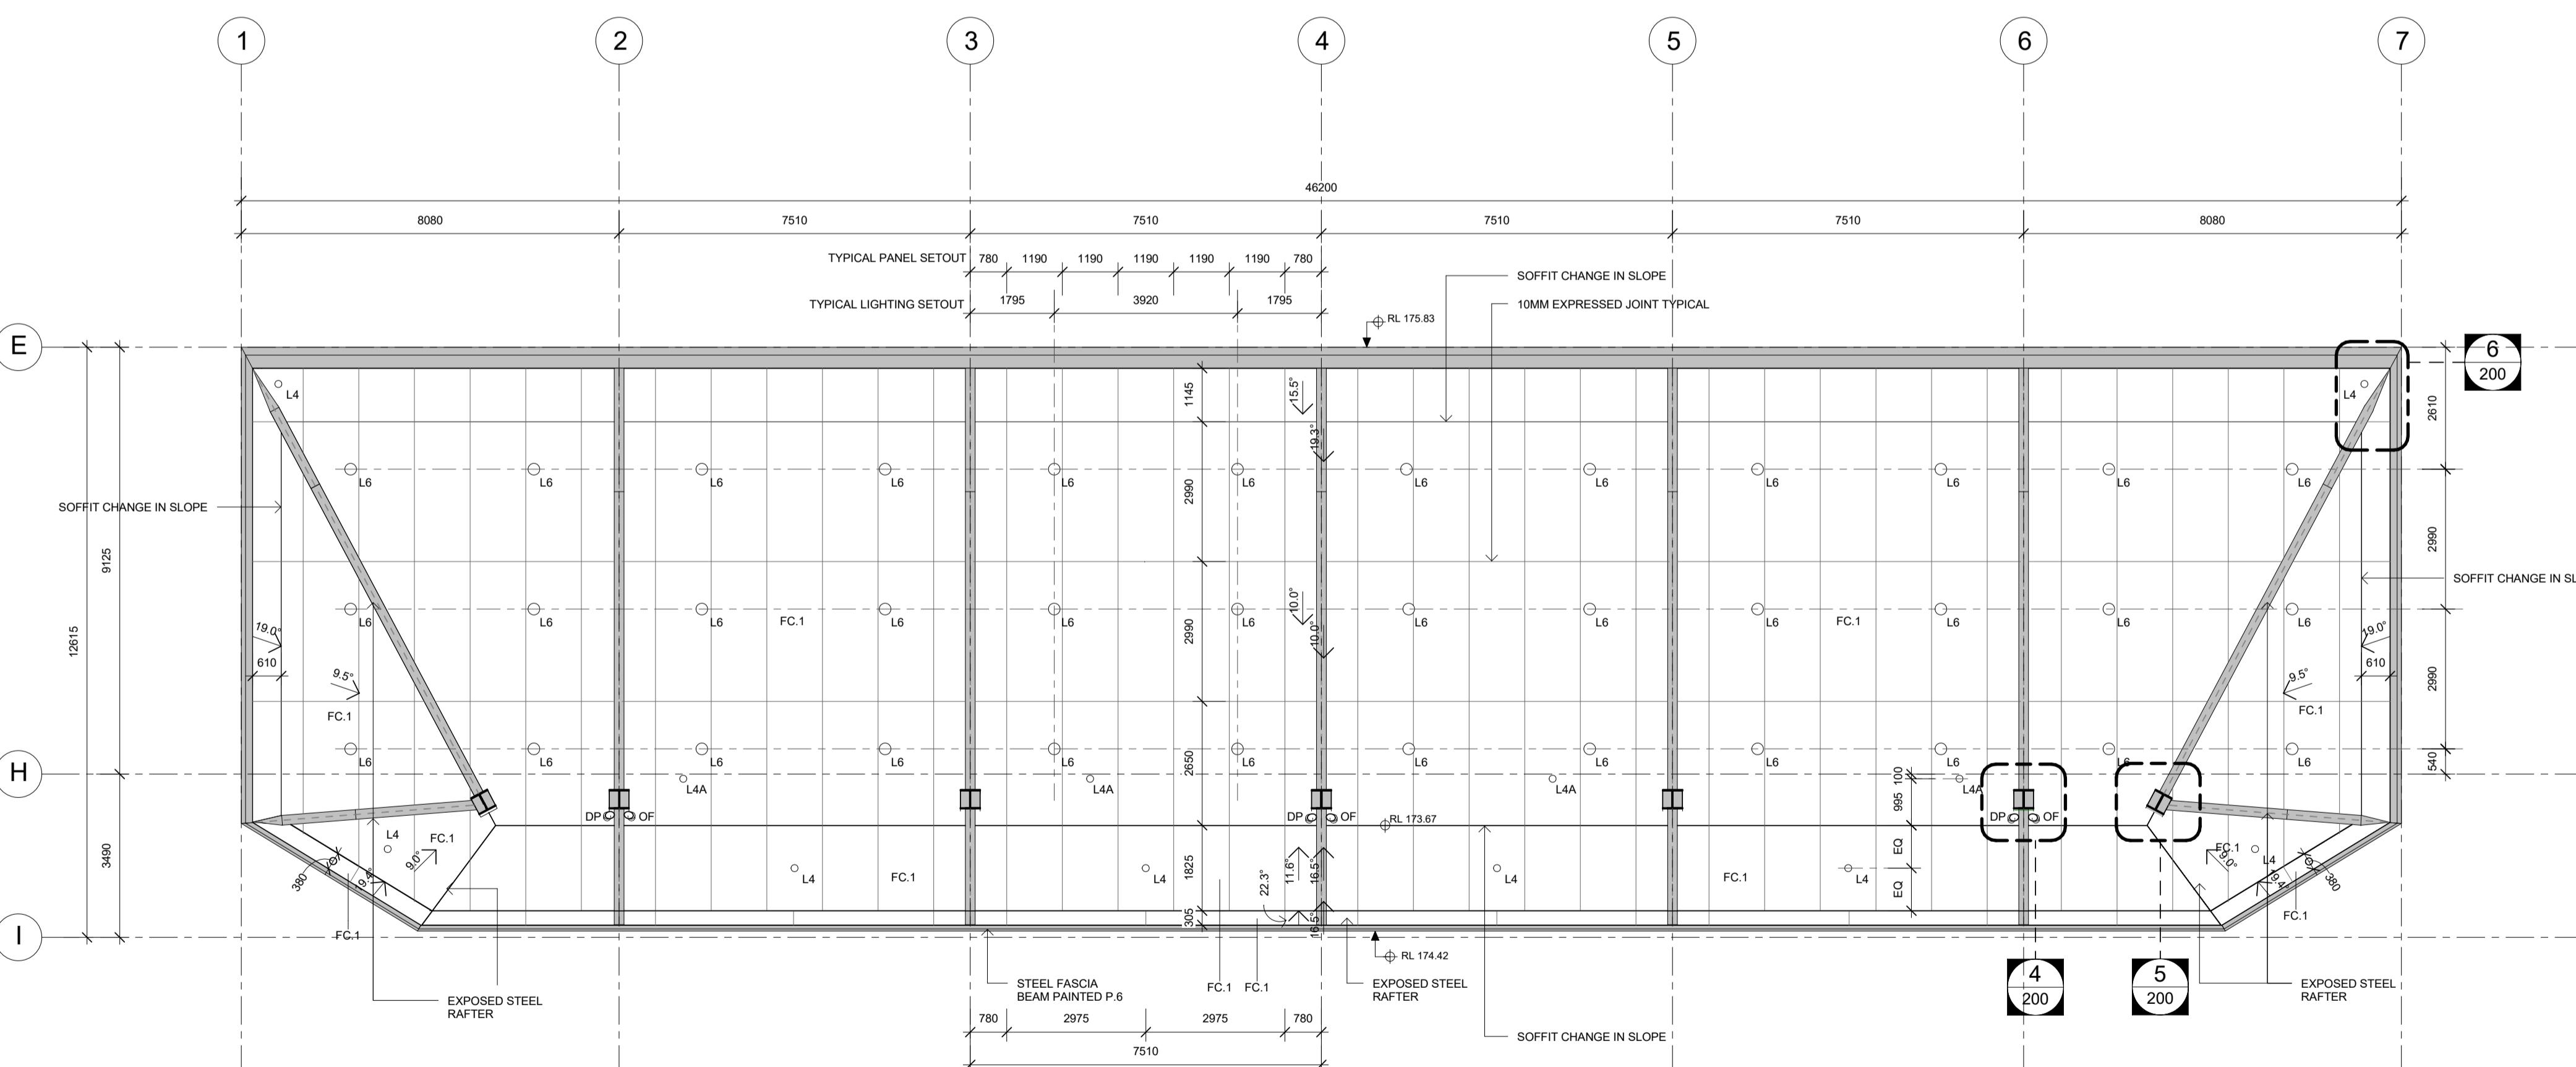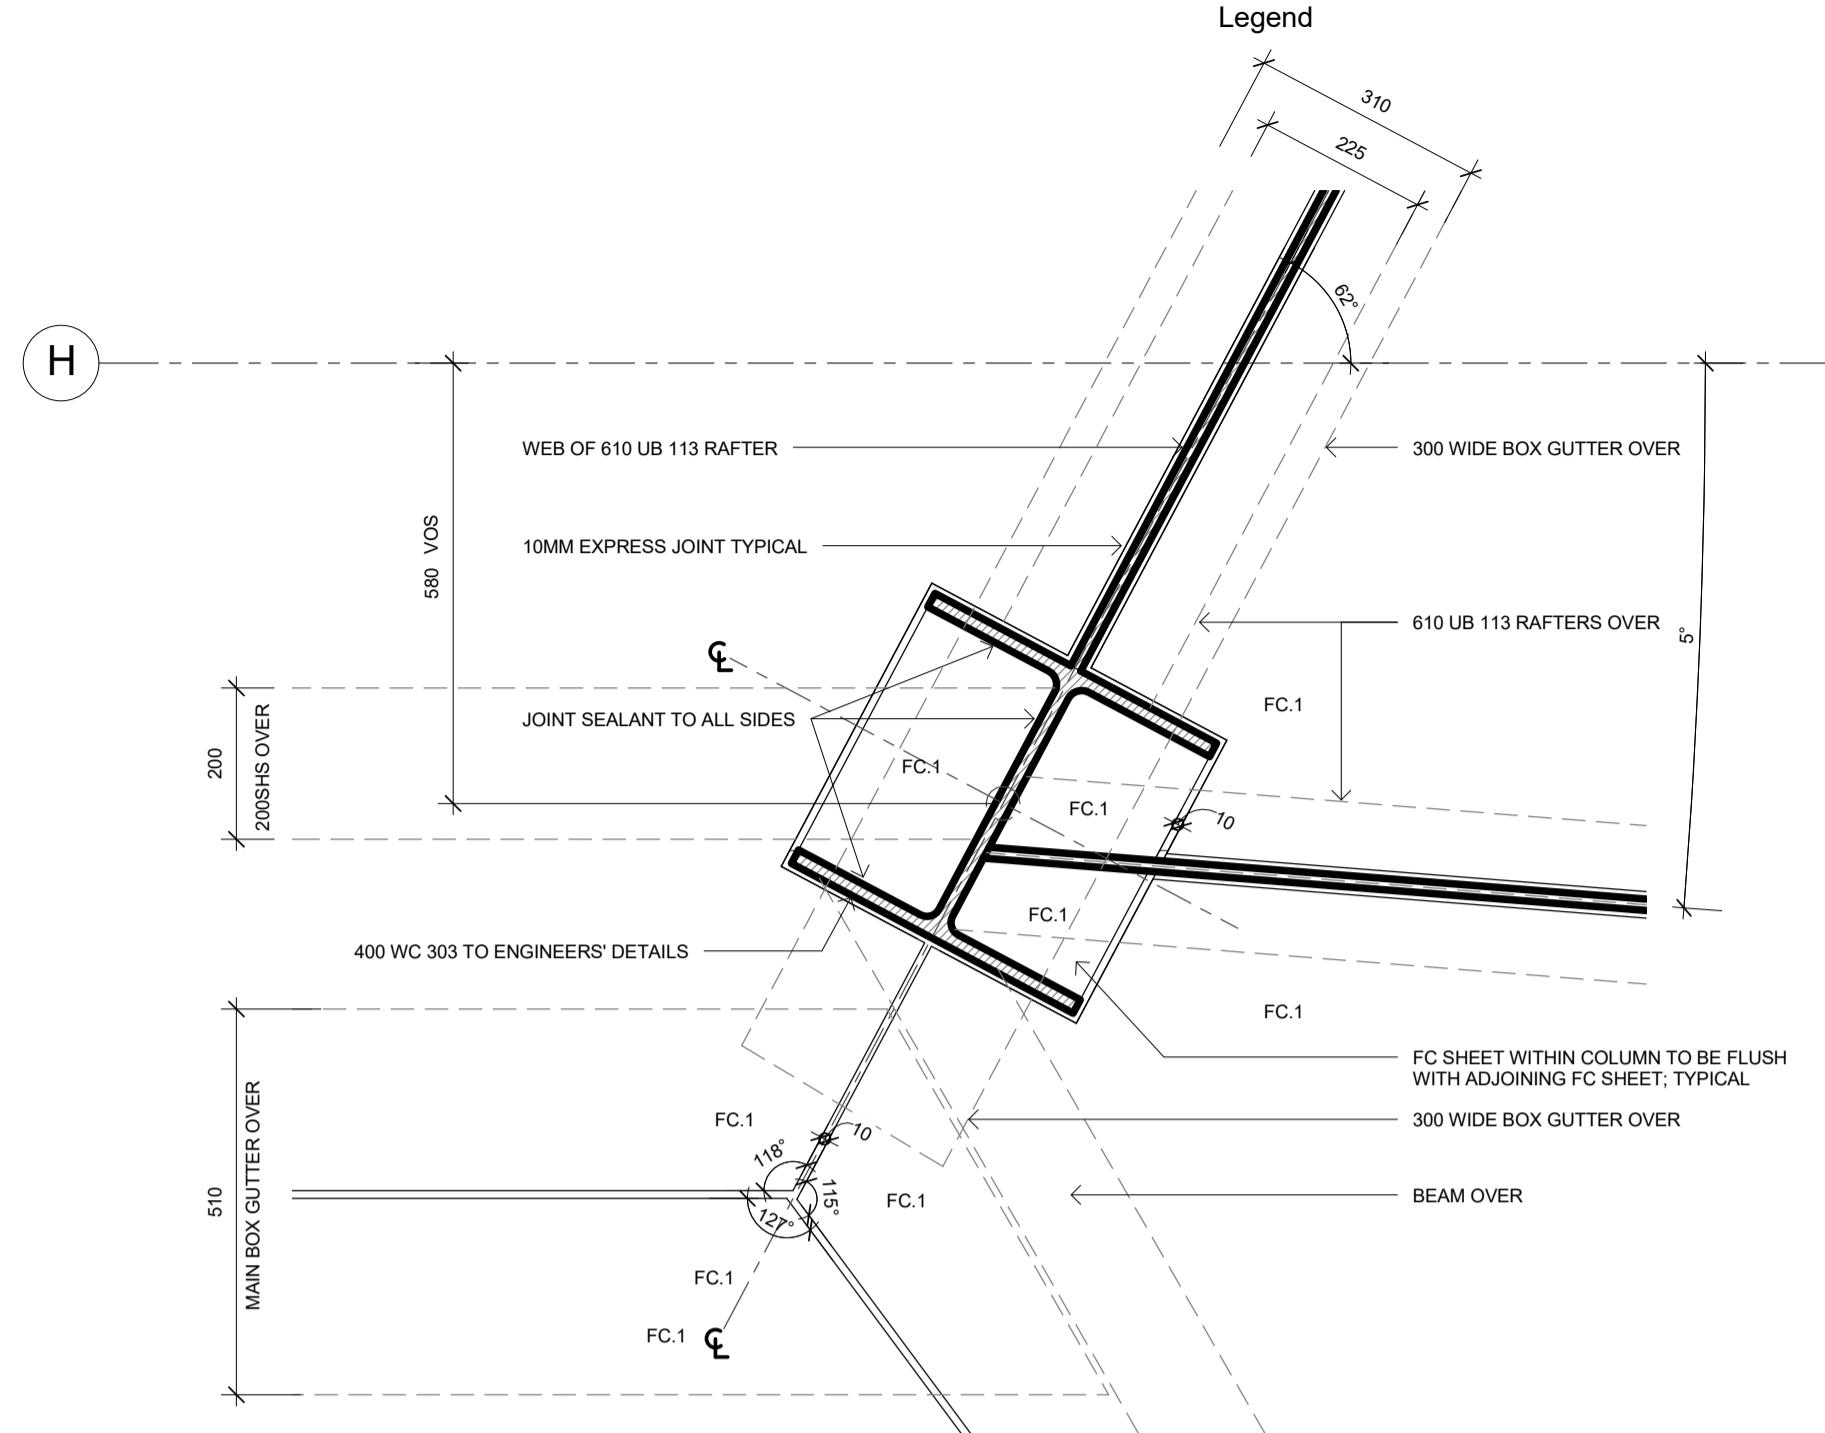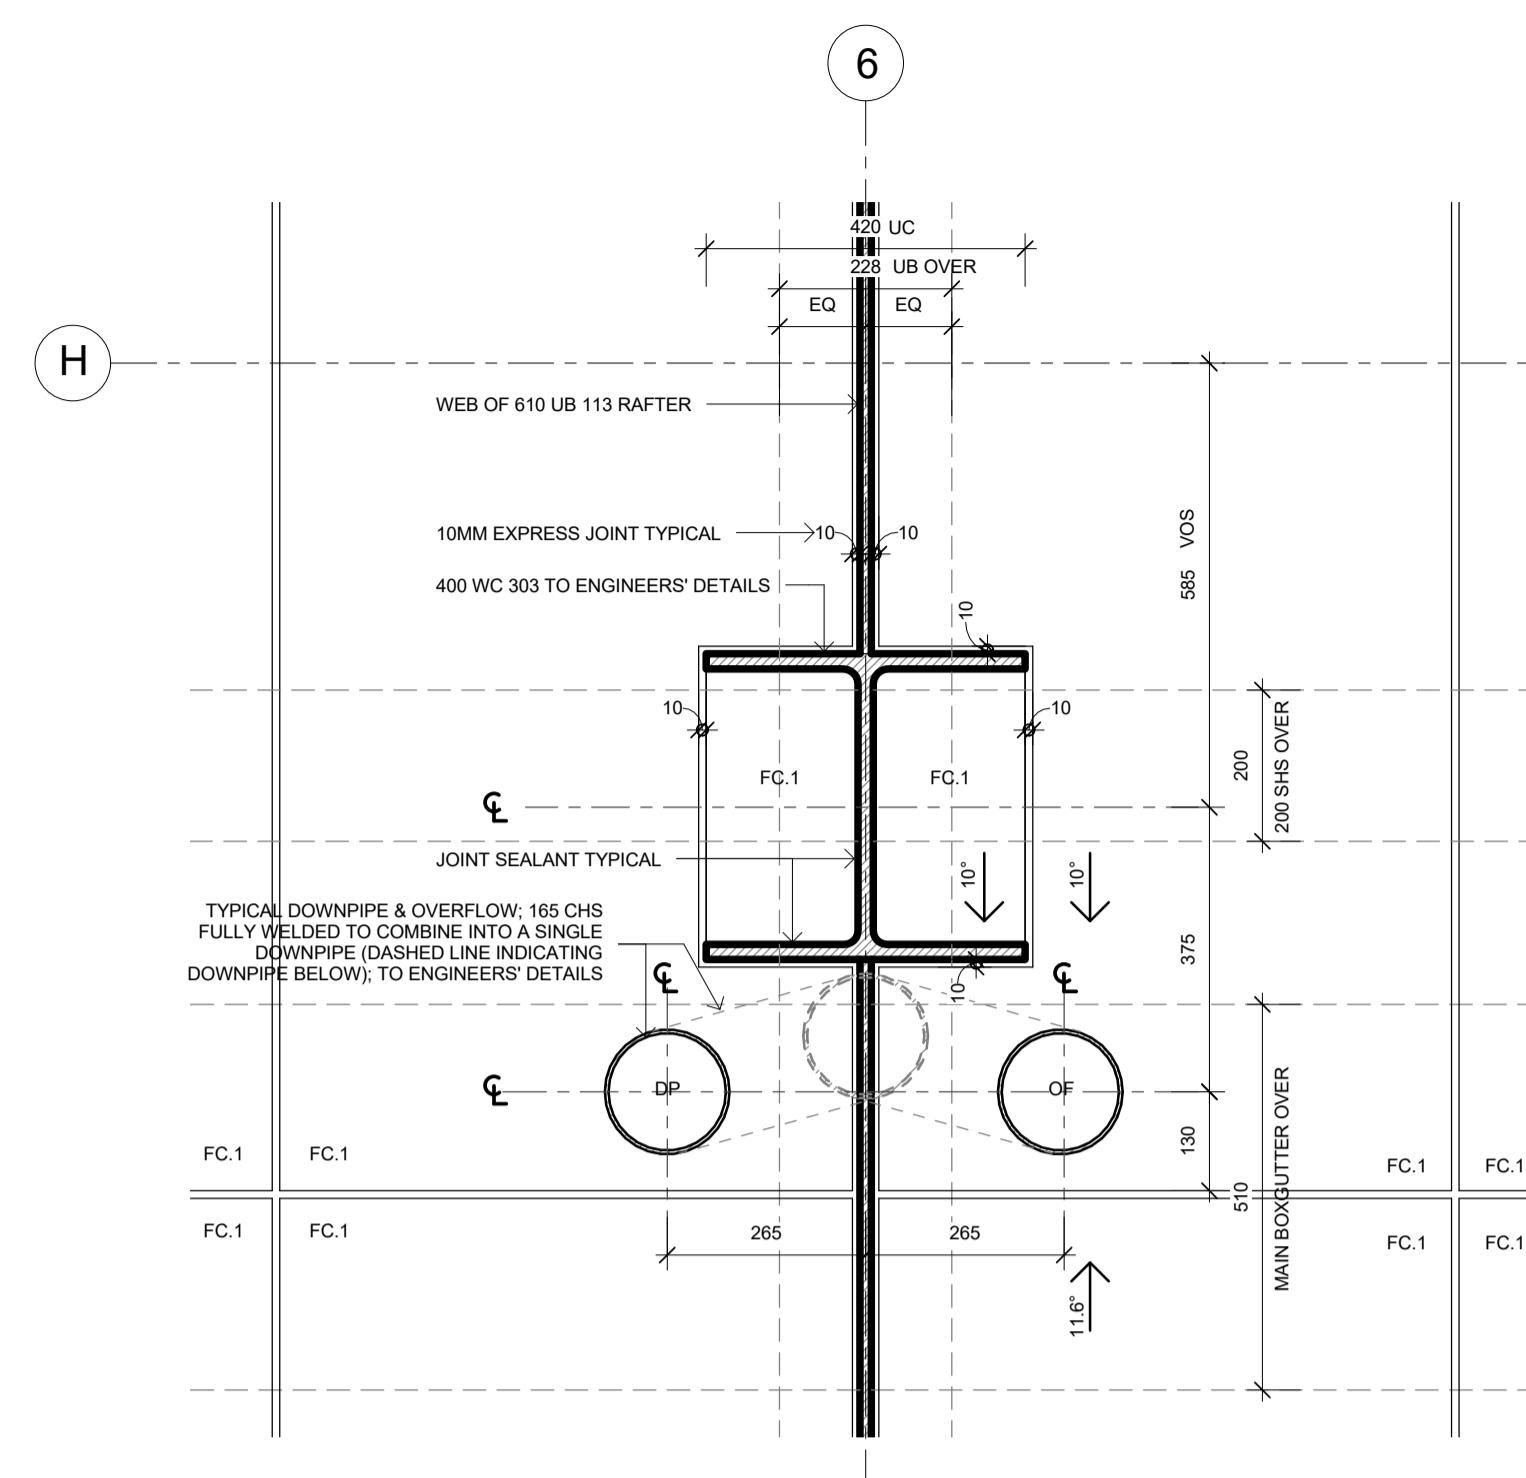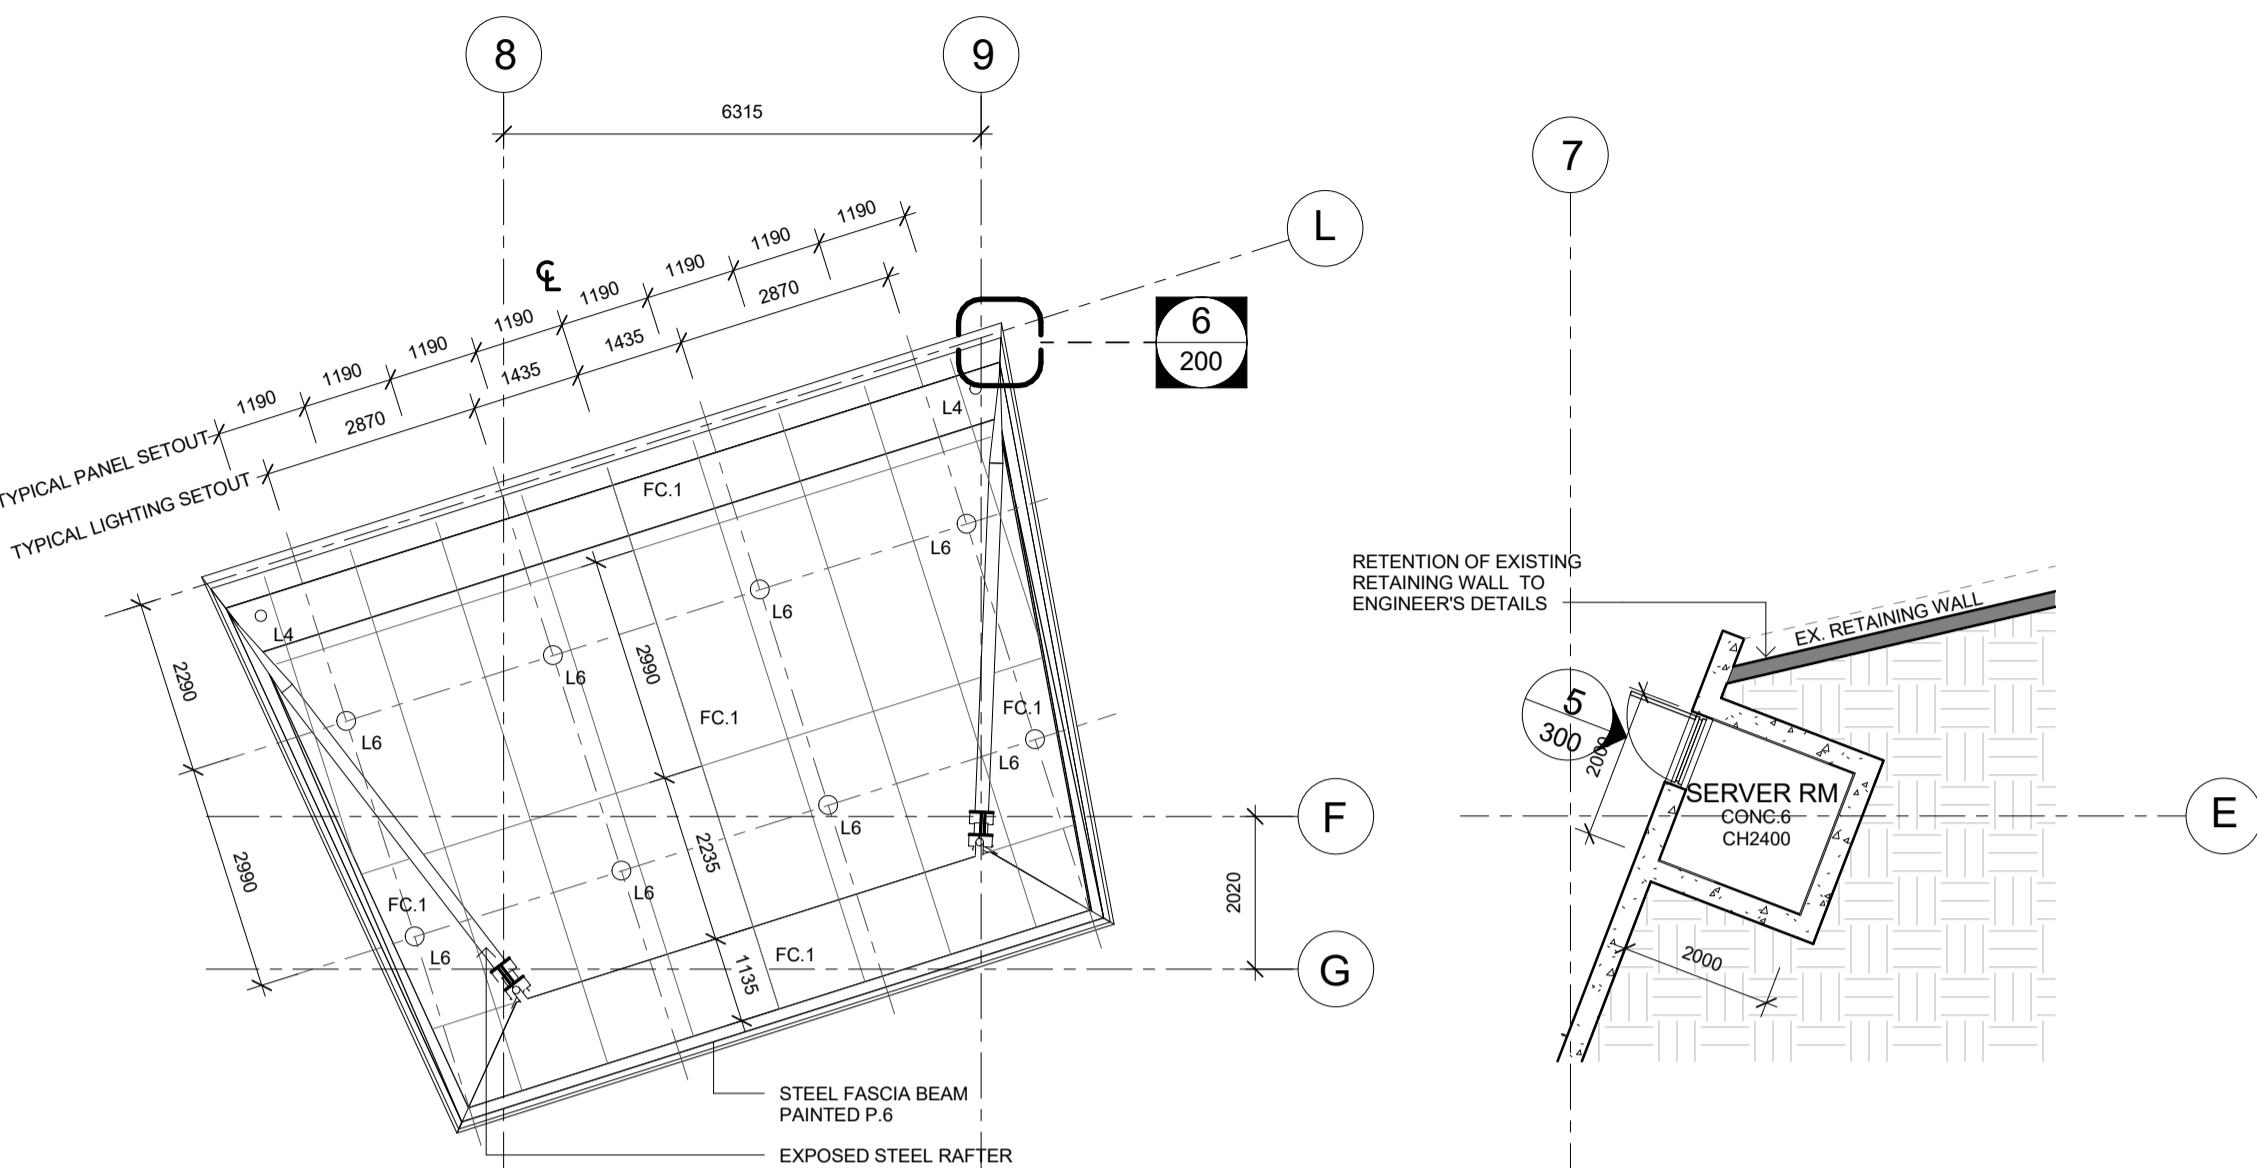

Issue No. Date 31/08/16 Description TENDER ISSUE Chkd AT

TENDER ISSUE

Electrical Engineer
Ken Offord
601/80 George St, Hornsby, NSW
T: +61 2 9477 4300 F: 612 xxxx xxxx
E: ken@kroanda.com.au

Hydraulic Engineer
Sparks+Partners Consulting Engineers
Level 1, 91 George Street, Parramatta NSW
T: 0401 803 330 F: 612 xxxx xxxx
E: Leon@sparksandpartners.com.au

Project Manager
Barker College
91 Pacific Highway, Hornsby, NSW, 2077
T: 02 9647 8318 F: 612 xxxx xxxx
E: georgina_rogers@barker.nsw.edu.au


Structural Engineer
Birzulis Associates
583 Darling Street Rozelle NSW 2039
T: 612 9555 7230 F: 612 xxxx xxxx
E: mgrogan@birzulisassociates.com

Drawing Title
Reflected Ceiling Plan


Project & Client
BARKER OVAL C.O.L.A & AMENITIES UPGRADE
at 91 Pacific Hwy, Hornsby, NSW, 2077
for **BARKER COLLEGE**

Architect
NBRSArchitecture.
Sydney 612 9922 2344 Melbourne 613 8676 0427
nbrsarchitecture.com.au
Any form of replication of this drawing in full or in part without the written permission of NBRSA+PARTNERS Pty Ltd constitutes an infringement of the copyright ABN 16 003 247 365 © 2016 Nominated Architects: Geoffrey Deane 3766; Andrew Duffin 5602; Garry Hodnett 5286


Date 31/08/2016 5:38:12 PM
Scale As indicated @ A1
0 1m 2m 3m 4m 5m 6m
Drawing Reference 15494-WD 200 -A

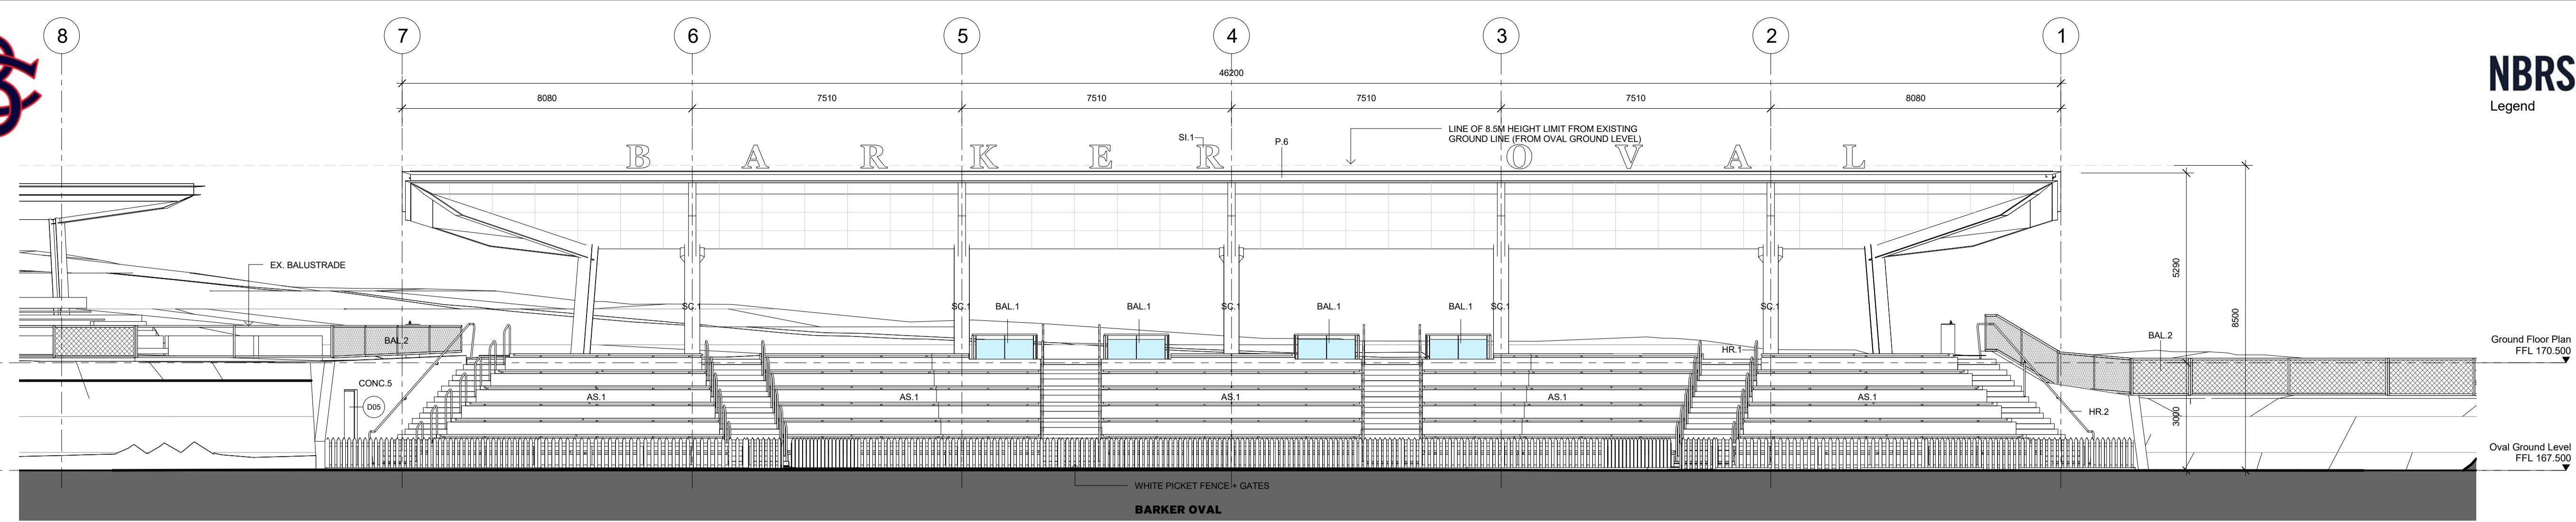


1 Front Elevation - Canopy 1 Covered Seating

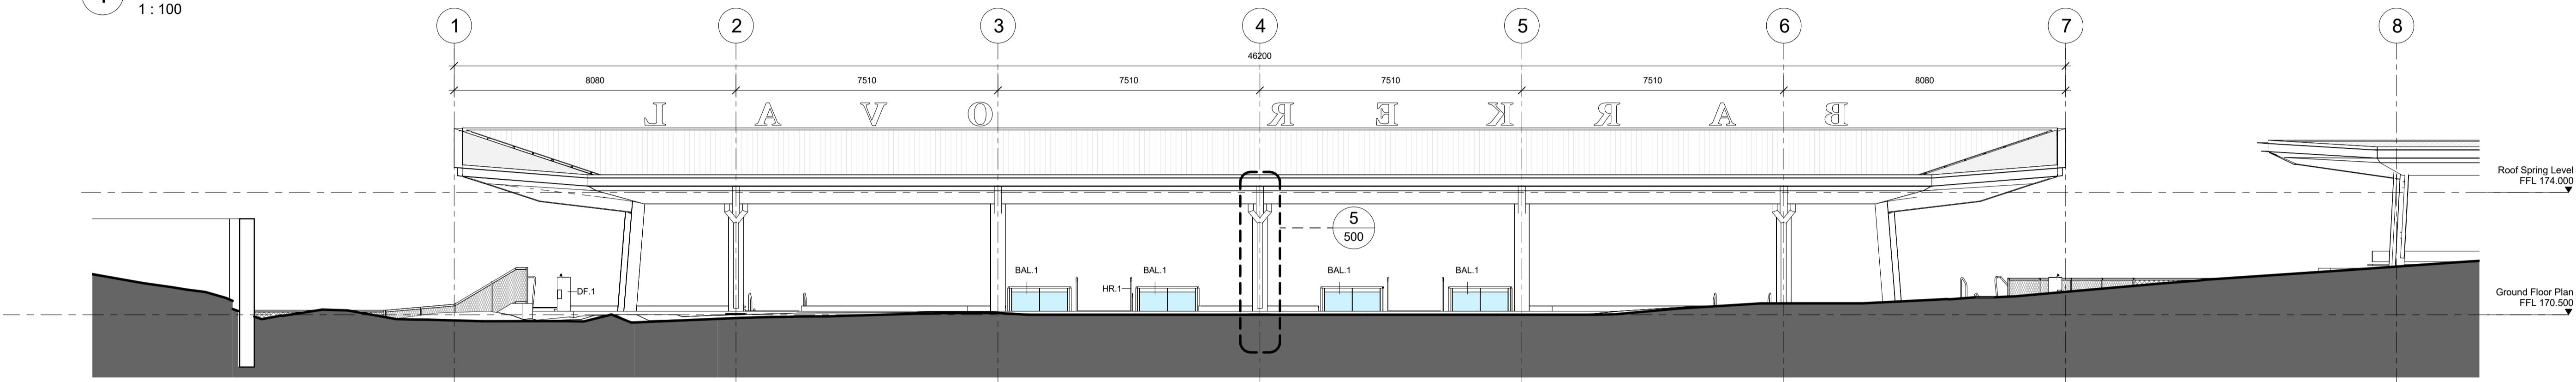

2 Back Elevation - Canopy 1 Covered Seating

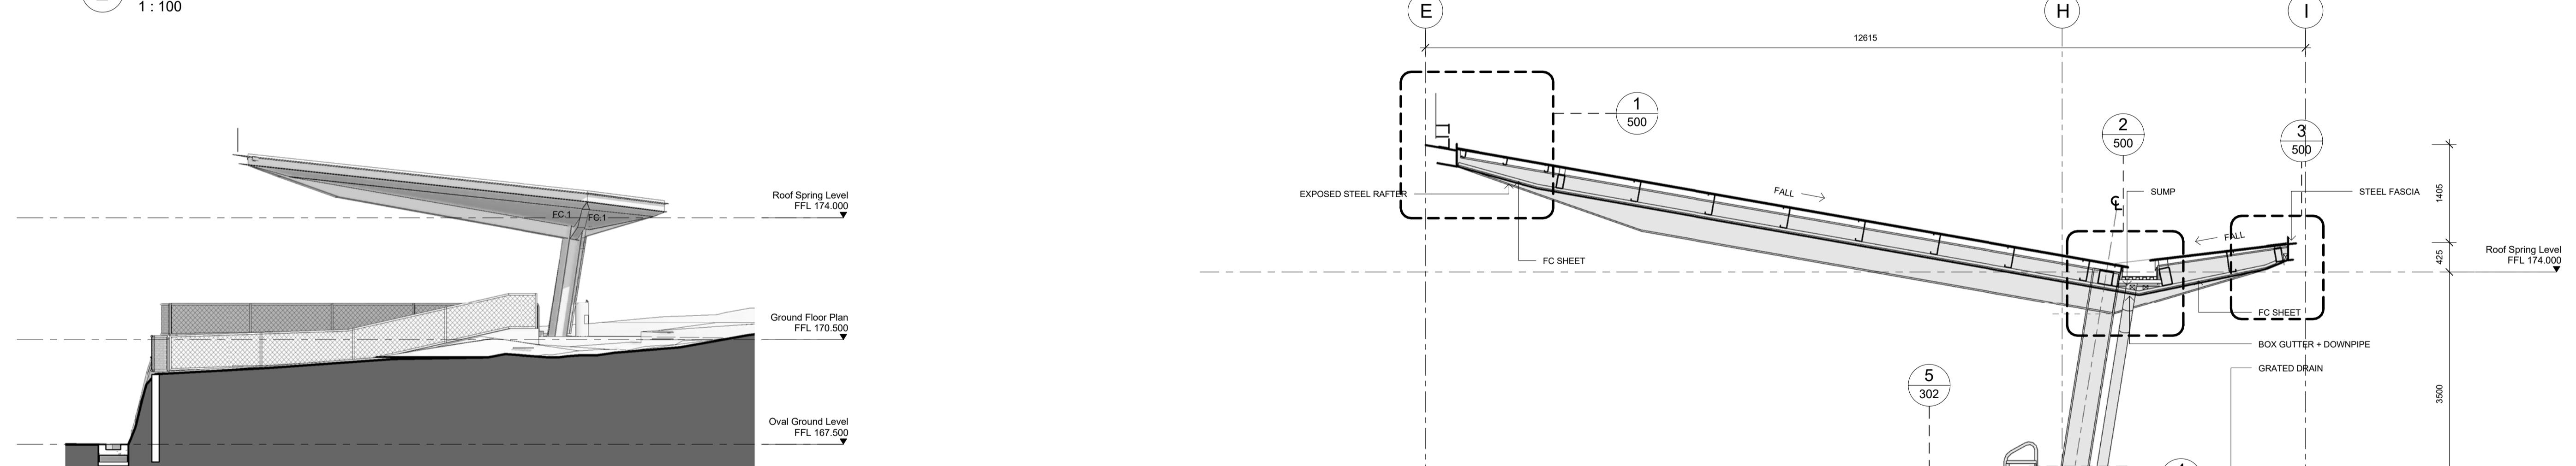

3 Side Elevation - Canopy 1 Covered Seating

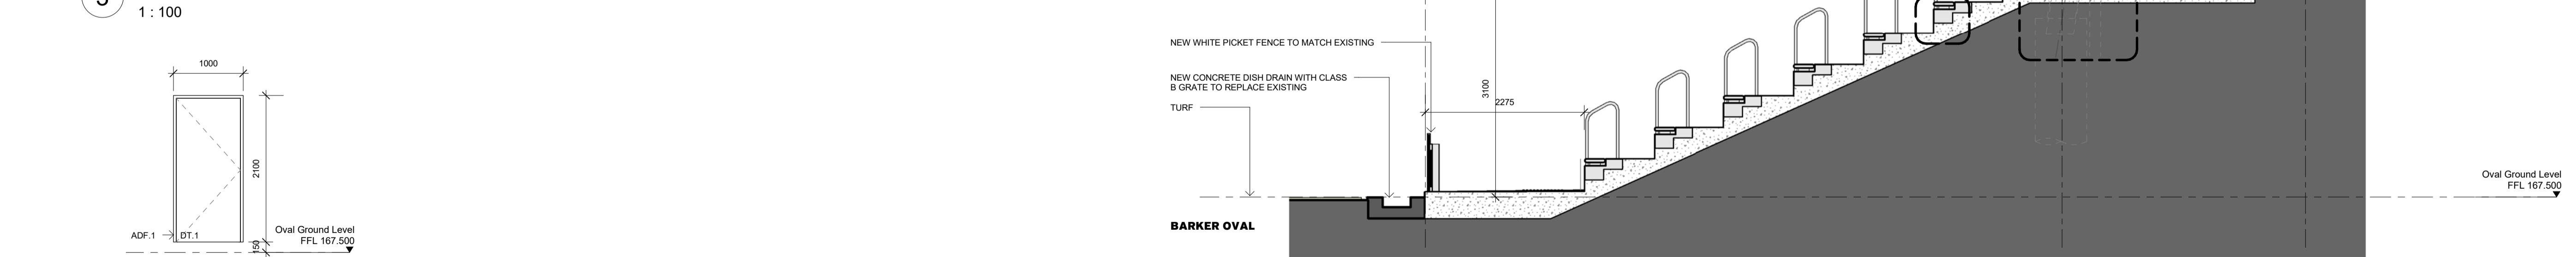

5 D05 Elevation



4 Section - Canopy 1 Covered Seating

Issue No. Date 31/08/16 Description TENDER ISSUE Chkd AT

TENDER ISSUE

Electrical Engineer
Ken Offord
601/80 George St, Hornsby, NSW
T: +61 2 9477 4300 F: 612 xxxx xxxx
E: ken@kroanda.com.au

Hydraulic Engineer
Sparks+Partners Consulting Engineers
Level 1, 91 George Street, Parramatta NSW
T: 0401 803 330 F: 612 xxxx xxxx
E: Leon@sparksandpartners.com.au

Project Manager
Barker College
91 Pacific Highway, Hornsby, NSW, 2077
T: 02 9647 8318 F: 612 xxxx xxxx
E: georgia_ringers@barker.nsw.edu.au

Drawing Title
Elevations & Section - Canopy 1


Project & Client
BARKER OVAL C.O.L.A & AMENITIES UPGRADE
at
91 Pacific Hwy, Hornsby, NSW, 2077
for
BARKER COLLEGE

Architect
NBRSArchitecture.
Sydney 612 9922 2344 Melbourne 613 8676 0427
nbrsarchitecture.com.au

Any form of replication of this drawing in full or in part without the written permission of NBRSA+PARTNERS Pty Ltd constitutes an infringement of the copyright
ABN 16 003 247 365 © 2016
Nominated Architects: Geoffrey Deane 3766; Andrew Duffin 5602; Garry Hodnett 5286

Date 31/08/2016 5:38:23 PM
Scale As indicated @ A1
0 1m 2m 3m 4m 5m 6m


Drawing Reference
15494-WD 300-A

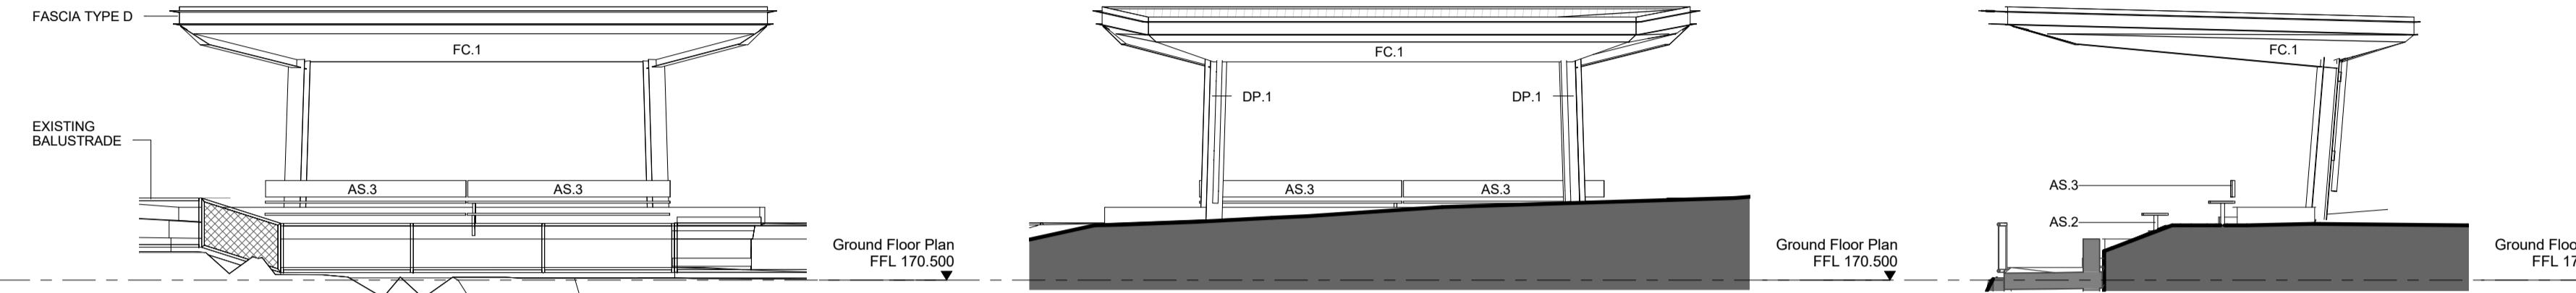


1 Typical Front Elevation - Canopy 2,3,4
1 : 100

2 Typical Back Elevation - Canopy 2,3,4
1 : 100


3 Typical Side Elevation - Canopy 2,3,4
1 : 100

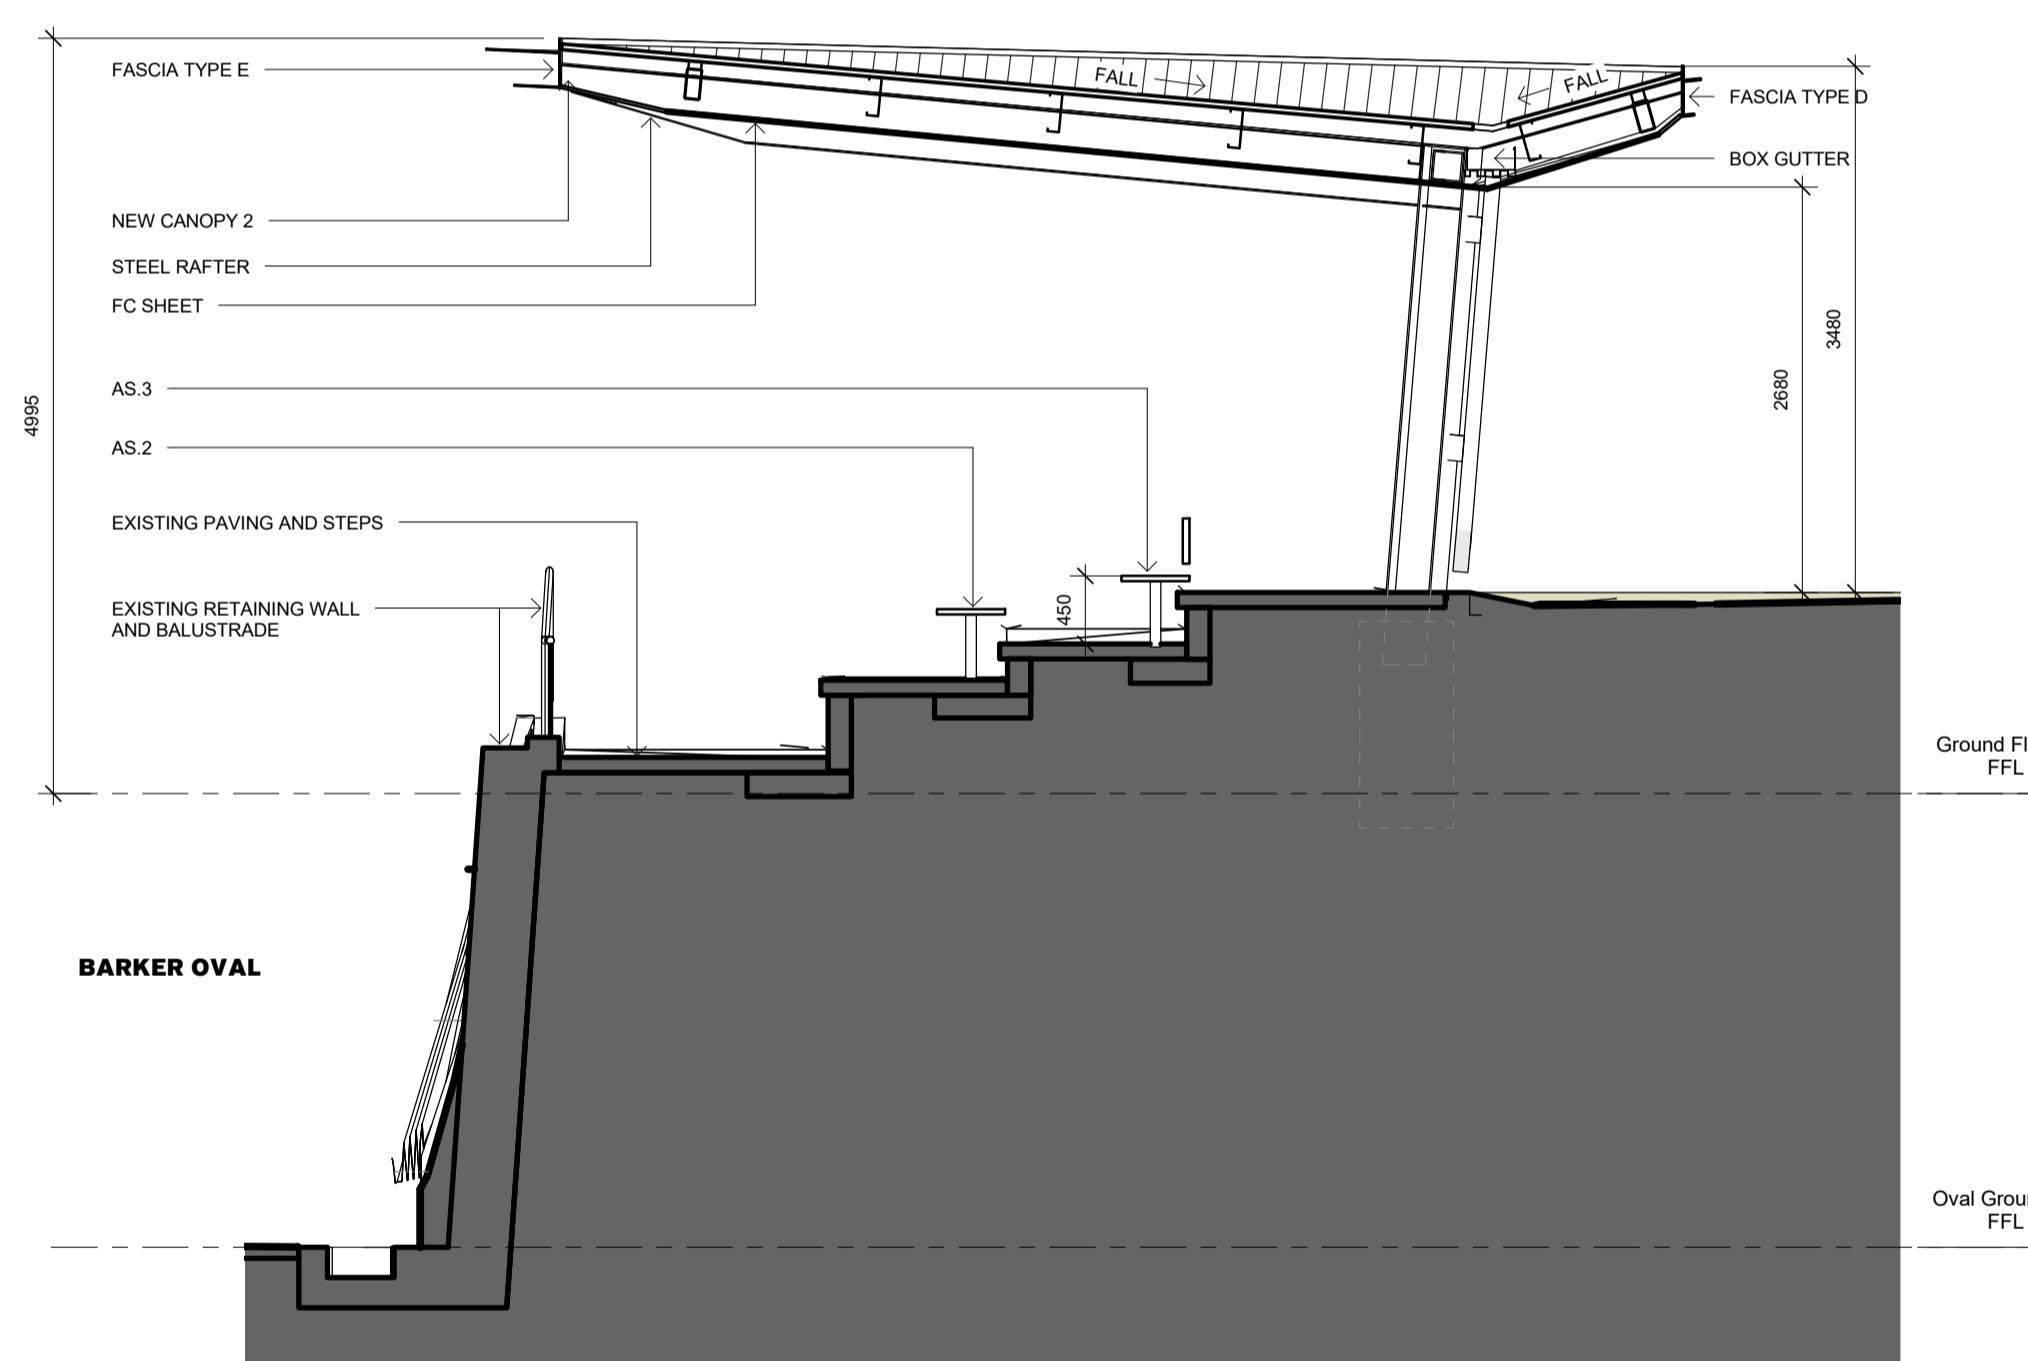


4 Canopy 2 Section (Canopy 3&4 Similar)
1 : 50

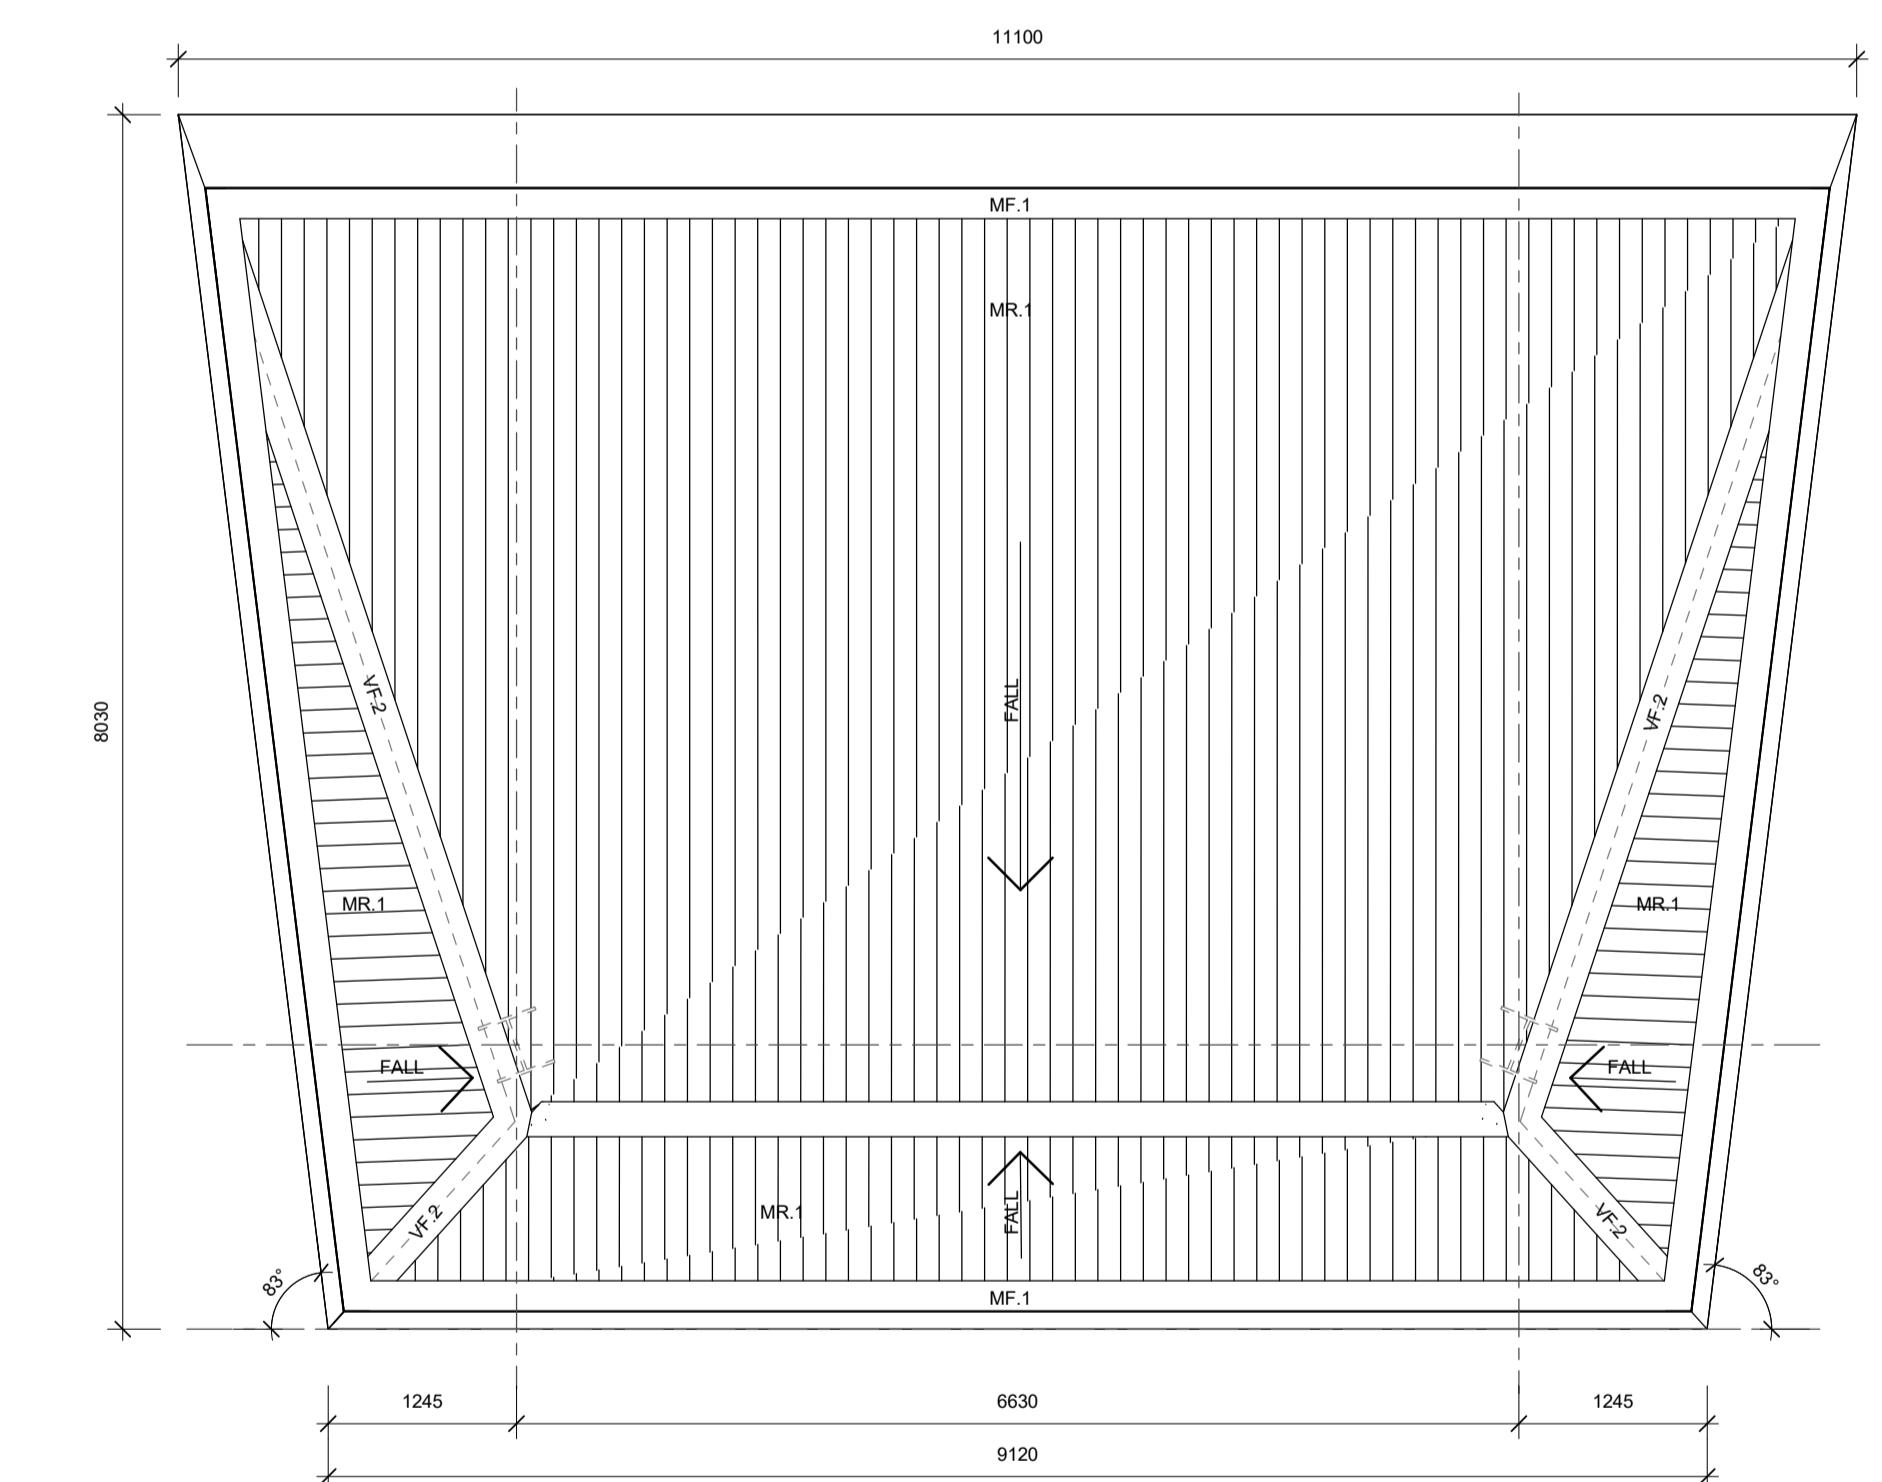


6 Typical Roof Plan - Canopy 2, 3 & 4
1 : 50

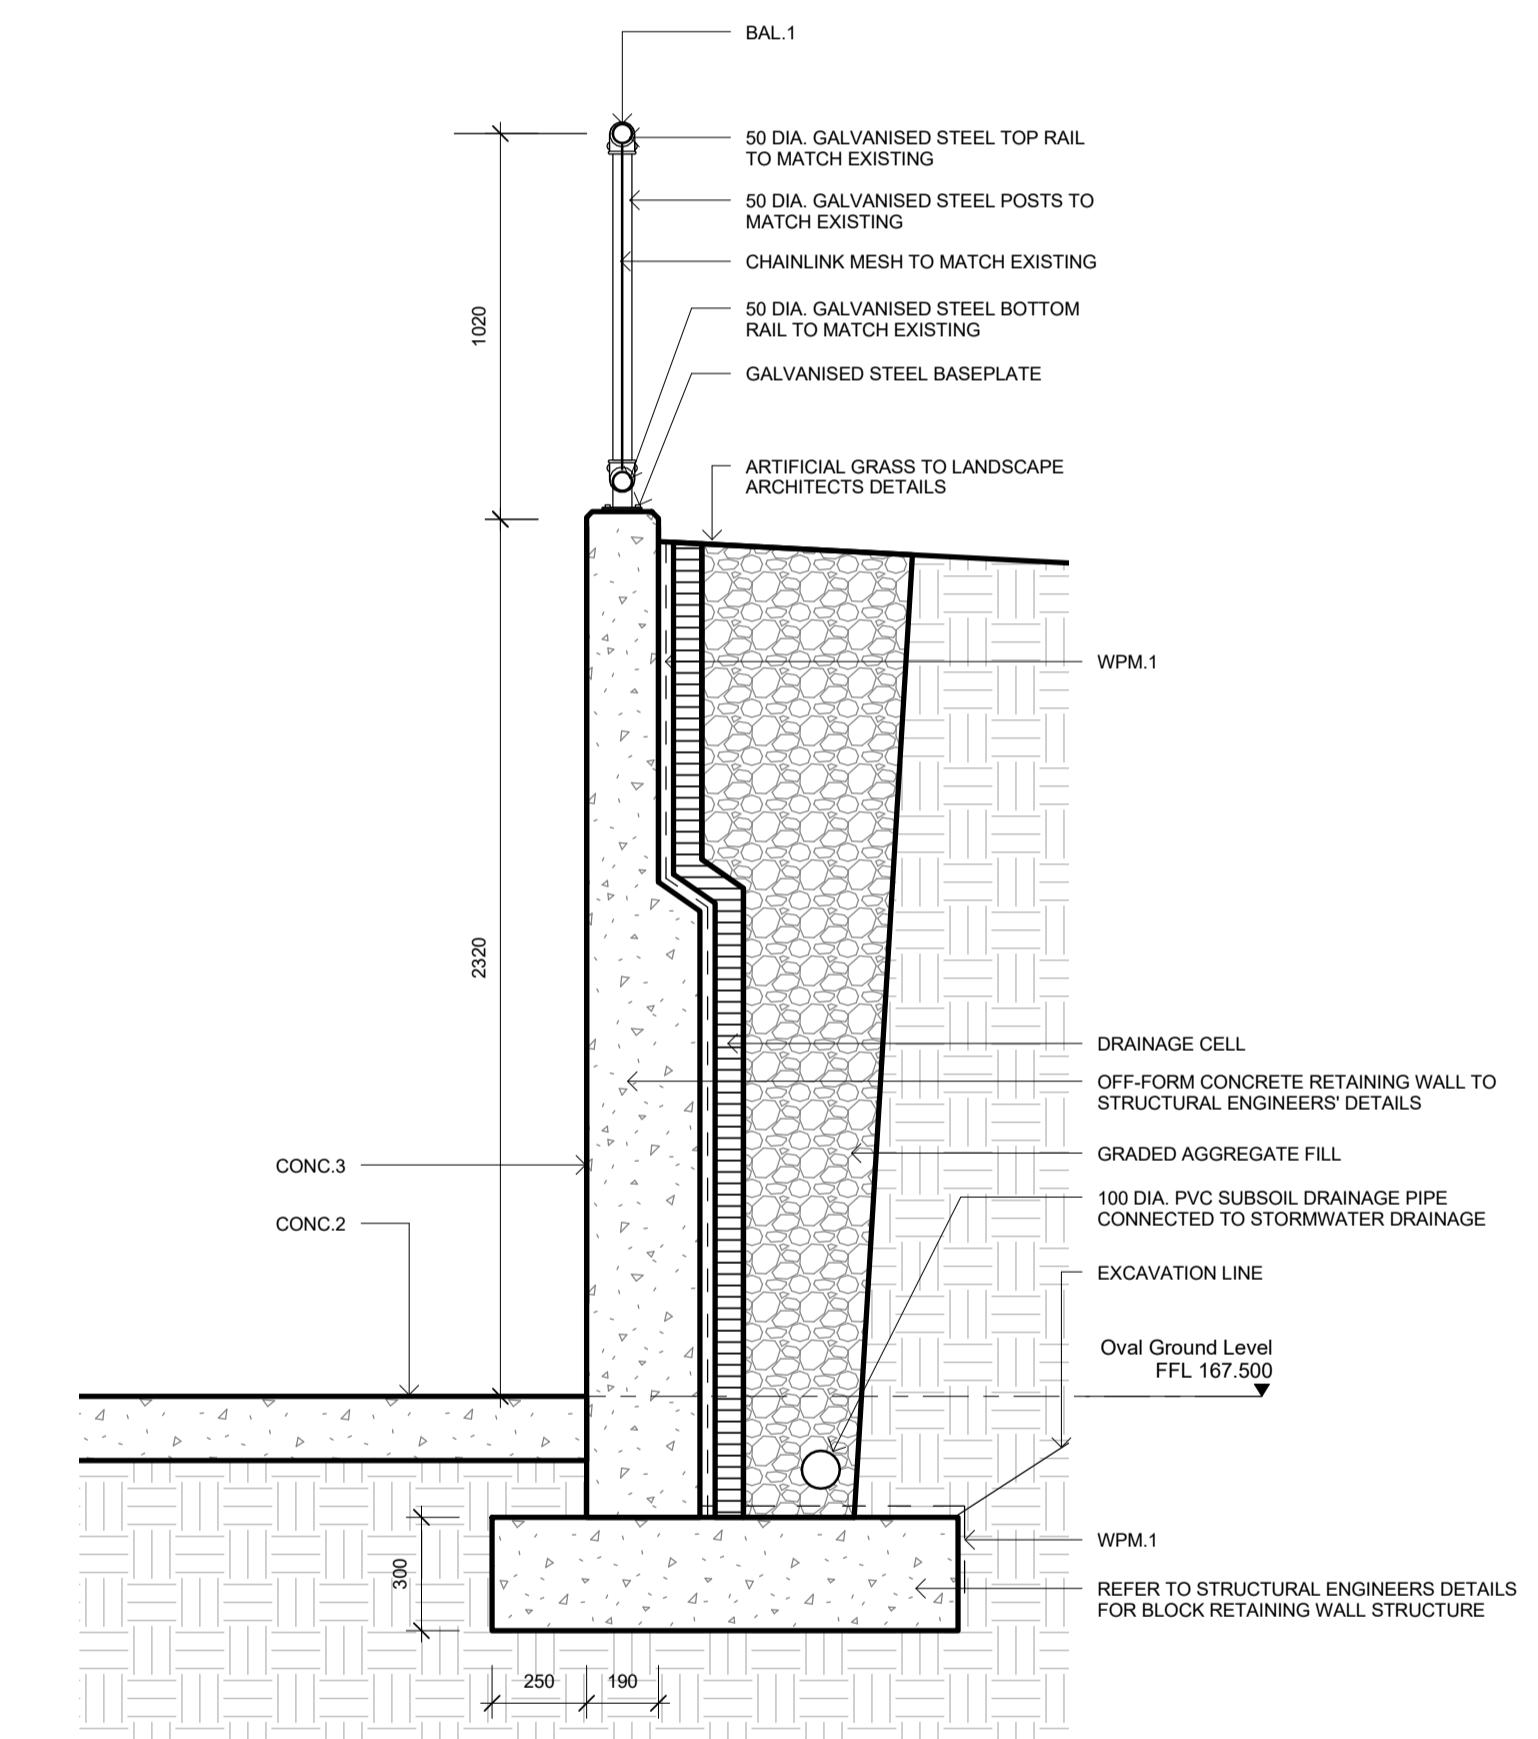


5 BAL2 & Typical Retaining Wall Detail
1 : 20

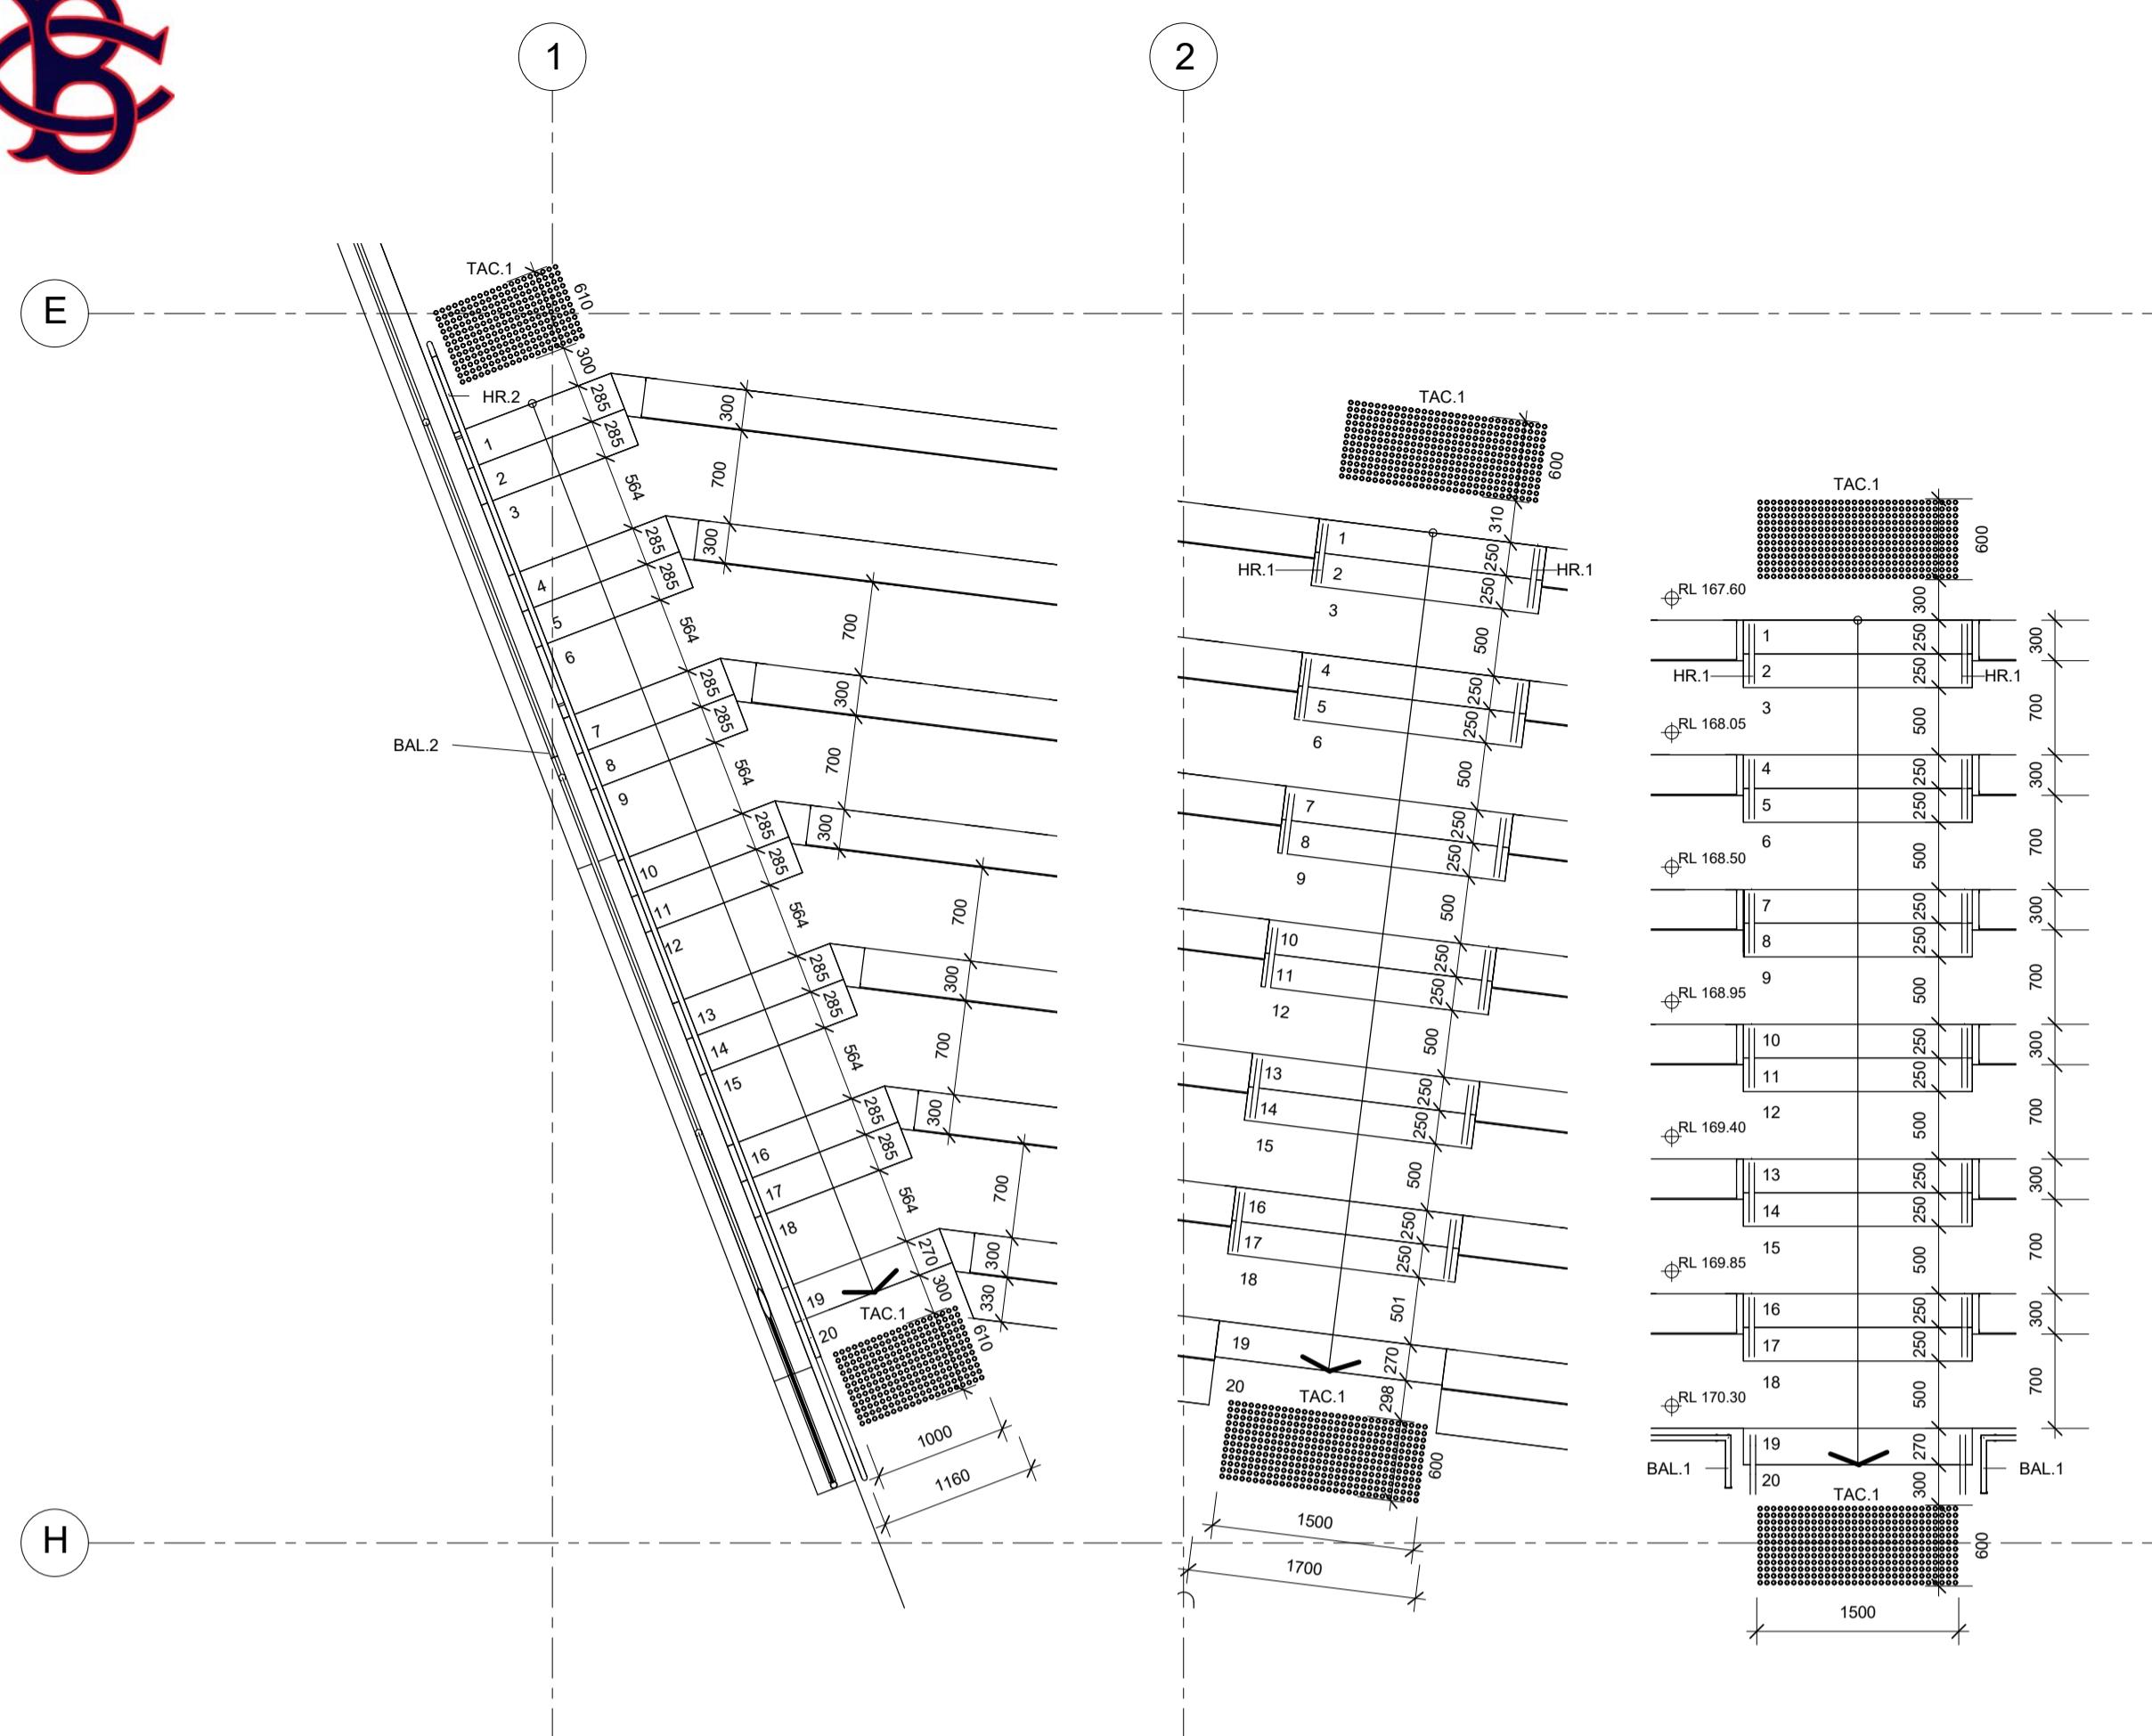


Stair Detail Plan - Canopy 1 Covered Seating

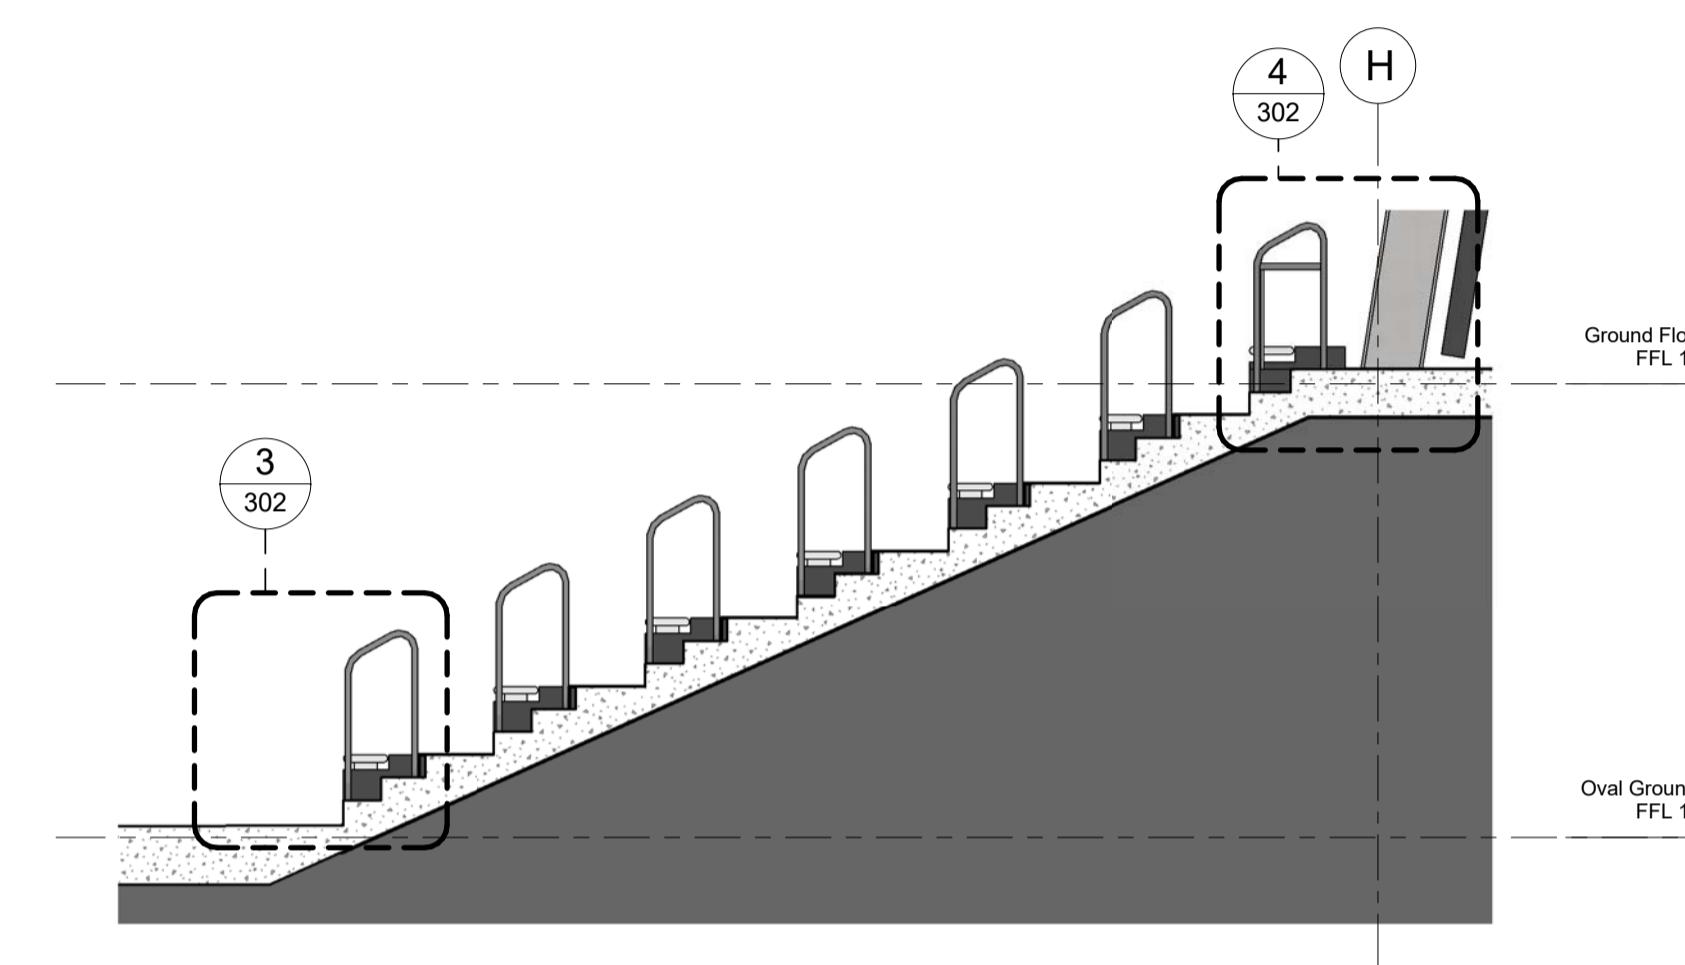


Stair 3 Typical Section - Canopy

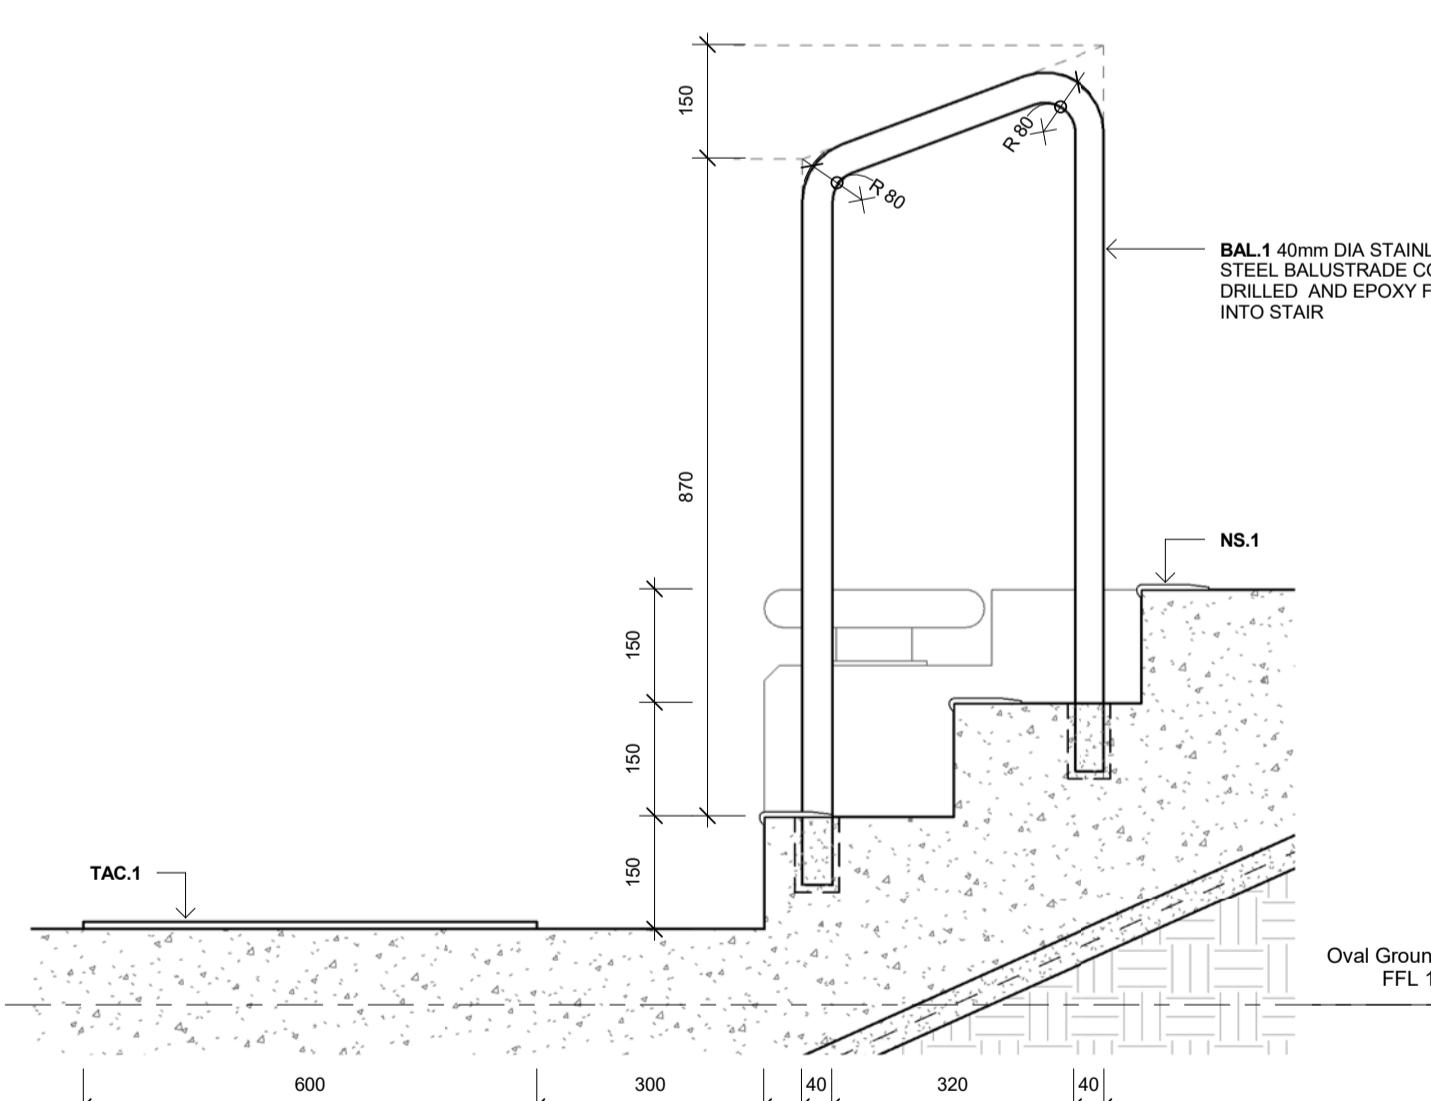

Typical Handrail Detail 1- Canopy 1

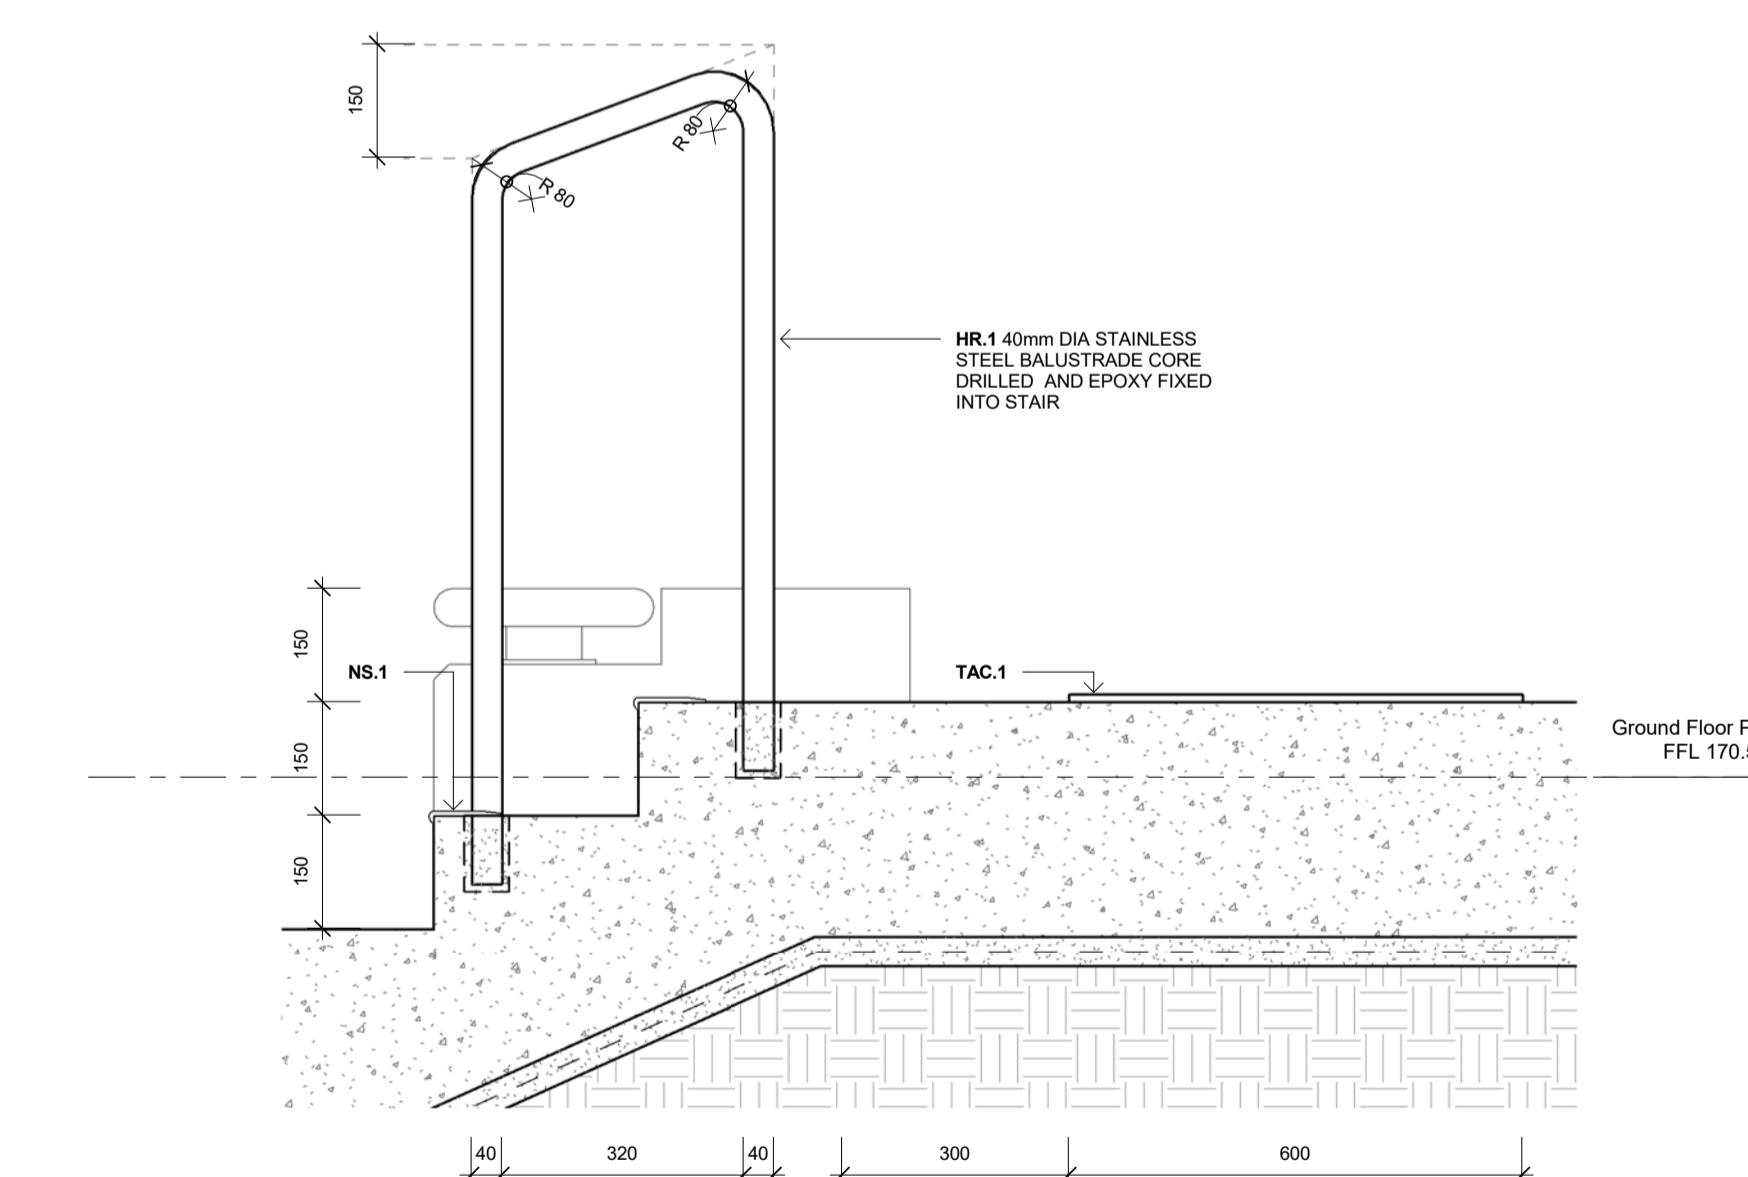

4 Typical Handrail Detail 2 - Canopy 1
1 : 10

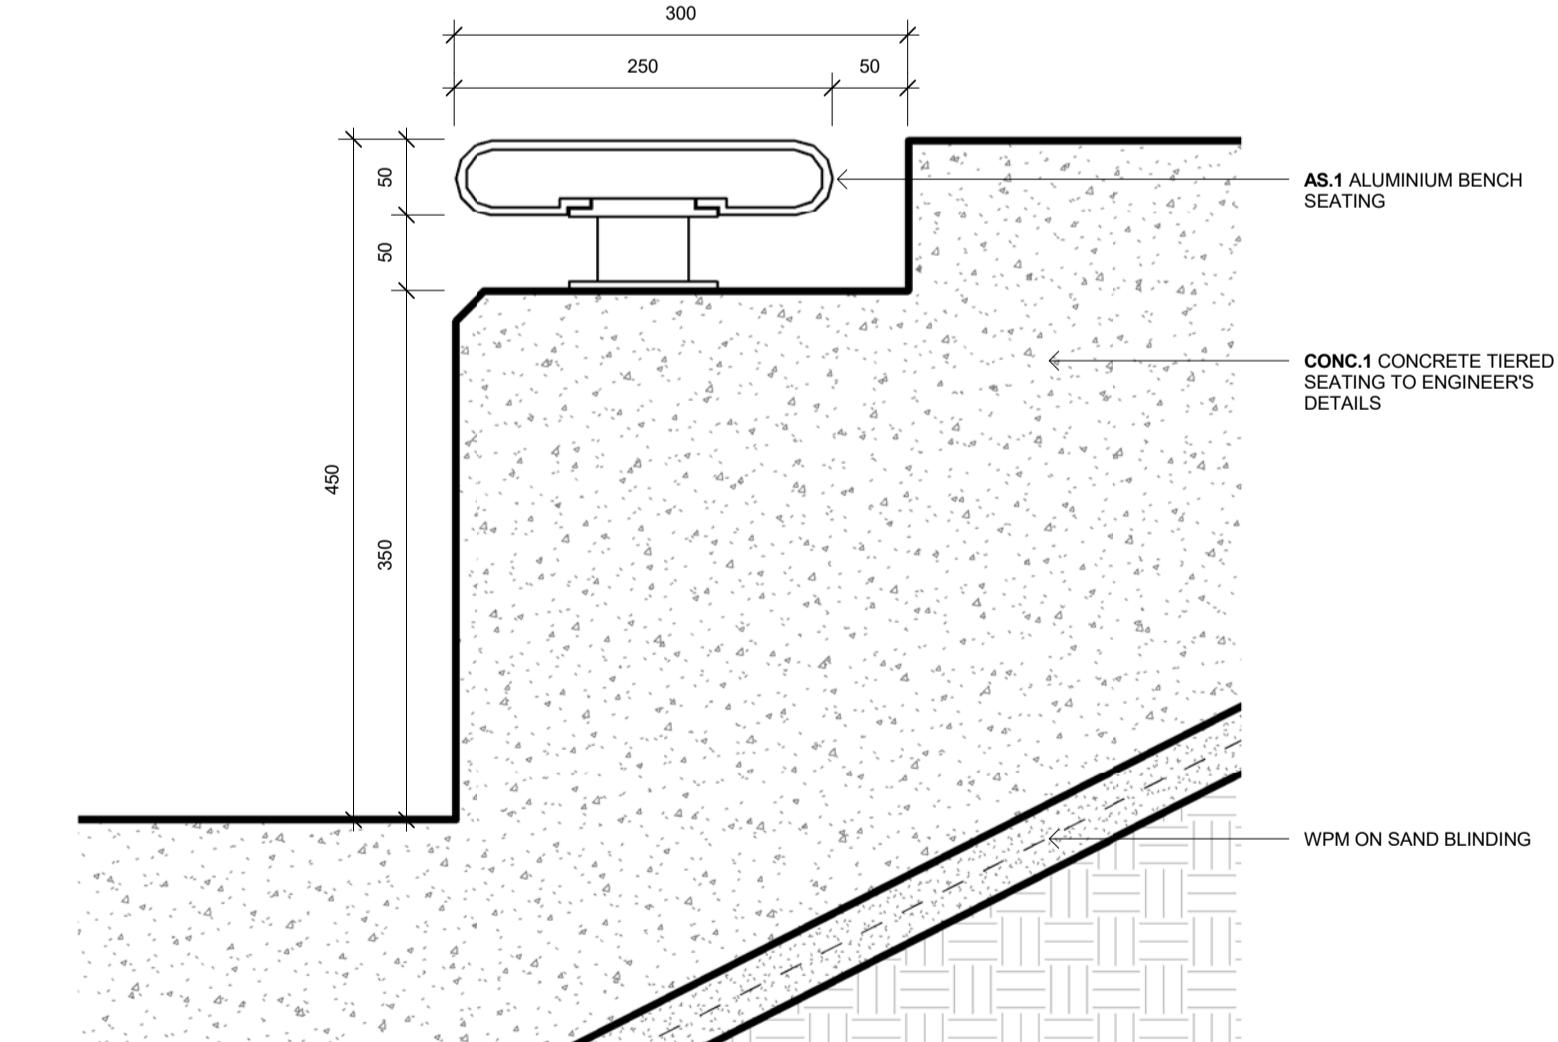

5
300
1 : 5

Typical Seating Detail - Canopy 1

Issue

No.	Date	Description
A	31/08/16	TENDER ISSUE

TENDER ISSUE

Electrical Engineer
Ken Offord
601/90 George St, Hornsby, NSW
T: + 61 2 9477 4300 **F:** 61 2 xxx
E: ken@kroanda.com.au

Hydraulic Engineer
Sparks+Partners Consulting Engineers
Level 1, 91 George Street, Parramatta NSW
T: 0401 803 330 **F:** 61 2 xxxx xxxx
E: Leon@sparksandpartners.com.au

Project Manager
Barker College
91 Pacific Highway, Hornsby, NSW, 2077
T: 02 9847 8318 **F:** 61 2 xxxx
E: georgina_rogers@barker.nsw.edu.au

Drawing Title

Stair & Handrail Detail

Project & Client

BARKER OVAL C.O.L.A & AMENITIES UPGRADE

at



91 Pacific Hwy, Hornsby, NSW, 2077

for

BARKER COLLEGE


Date 31/08/2016 5:38:32 PM
Scale As indicated @ A1

Drawing Reference
15494 - WD 302 - A

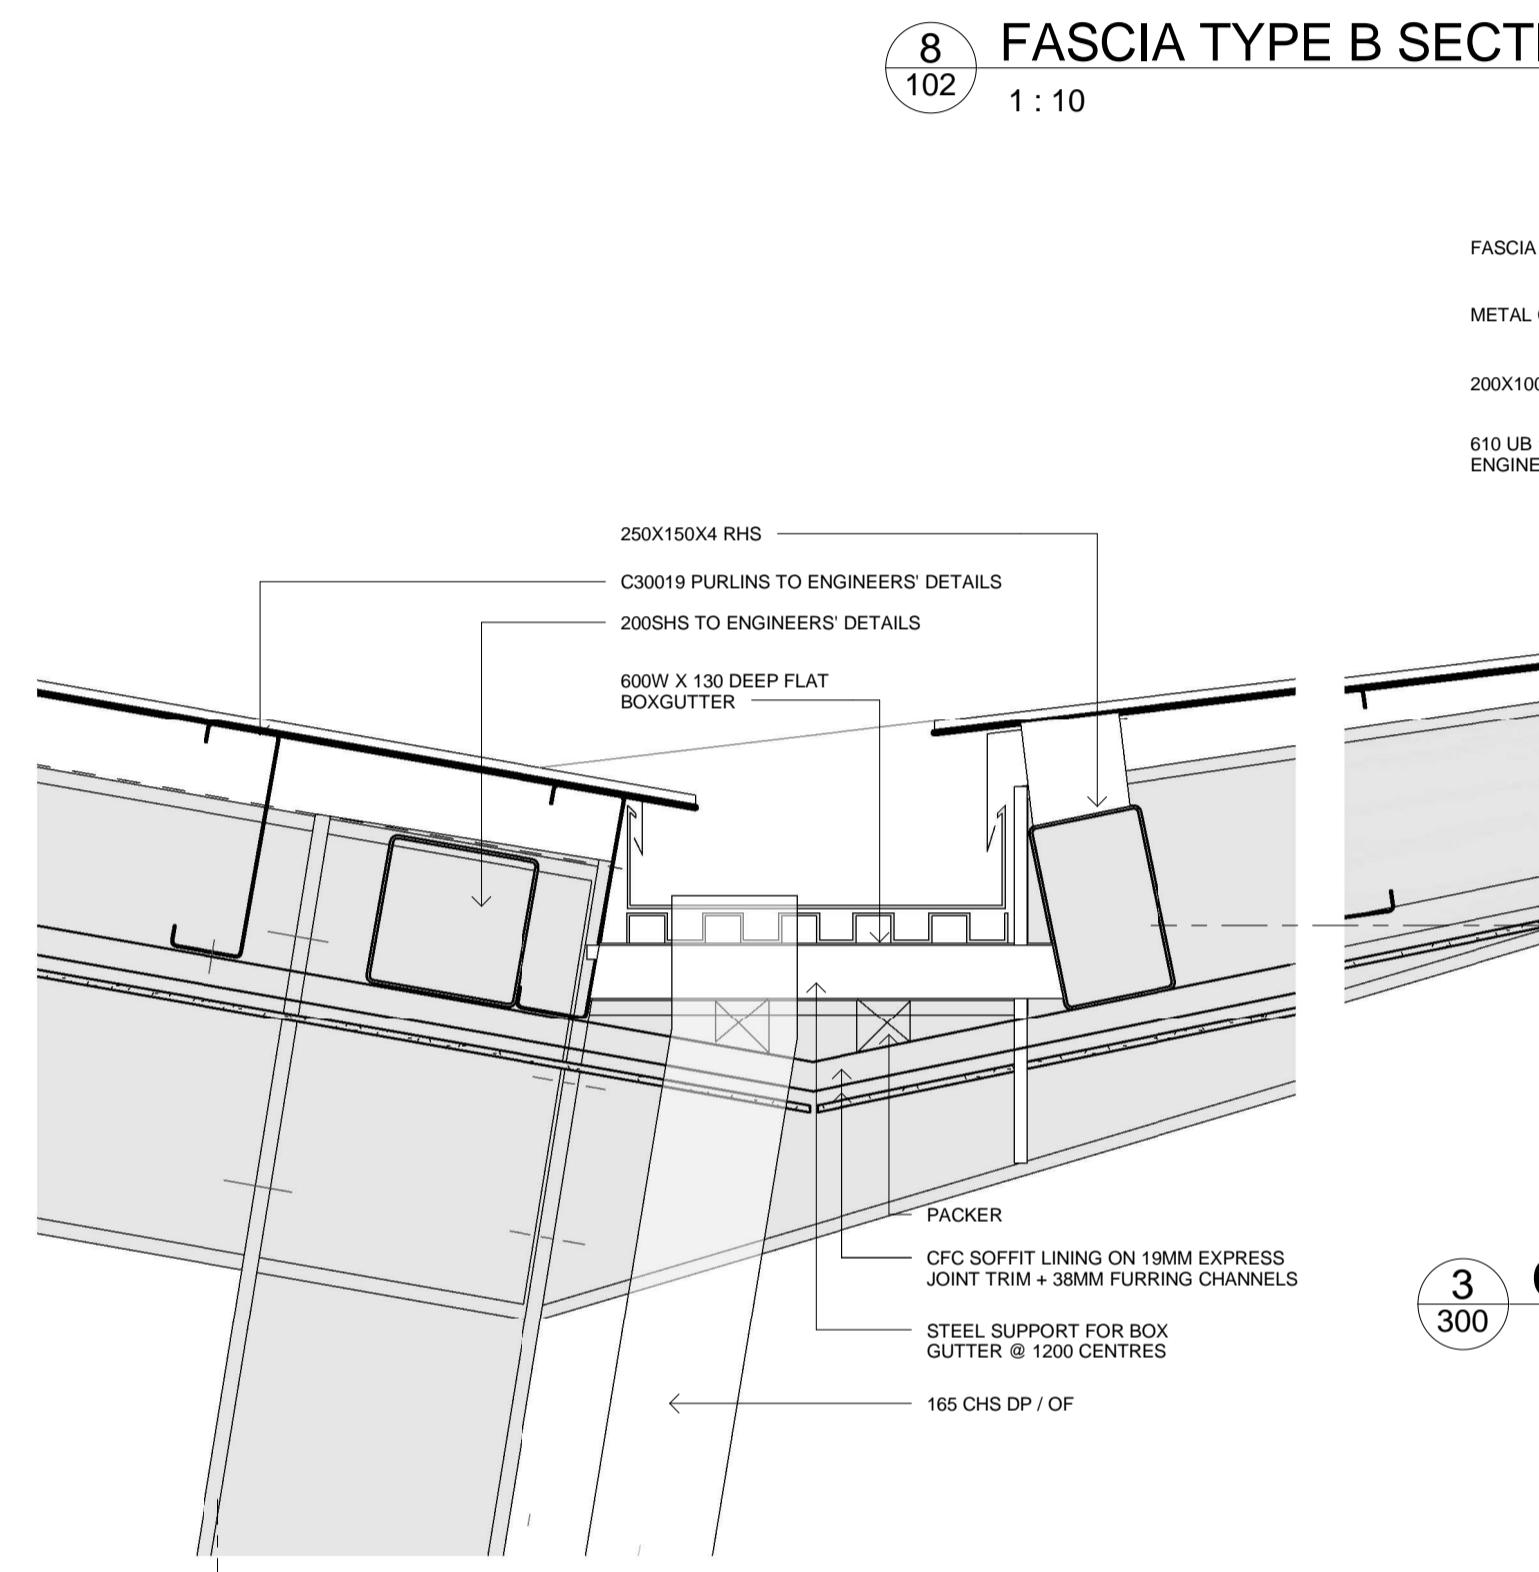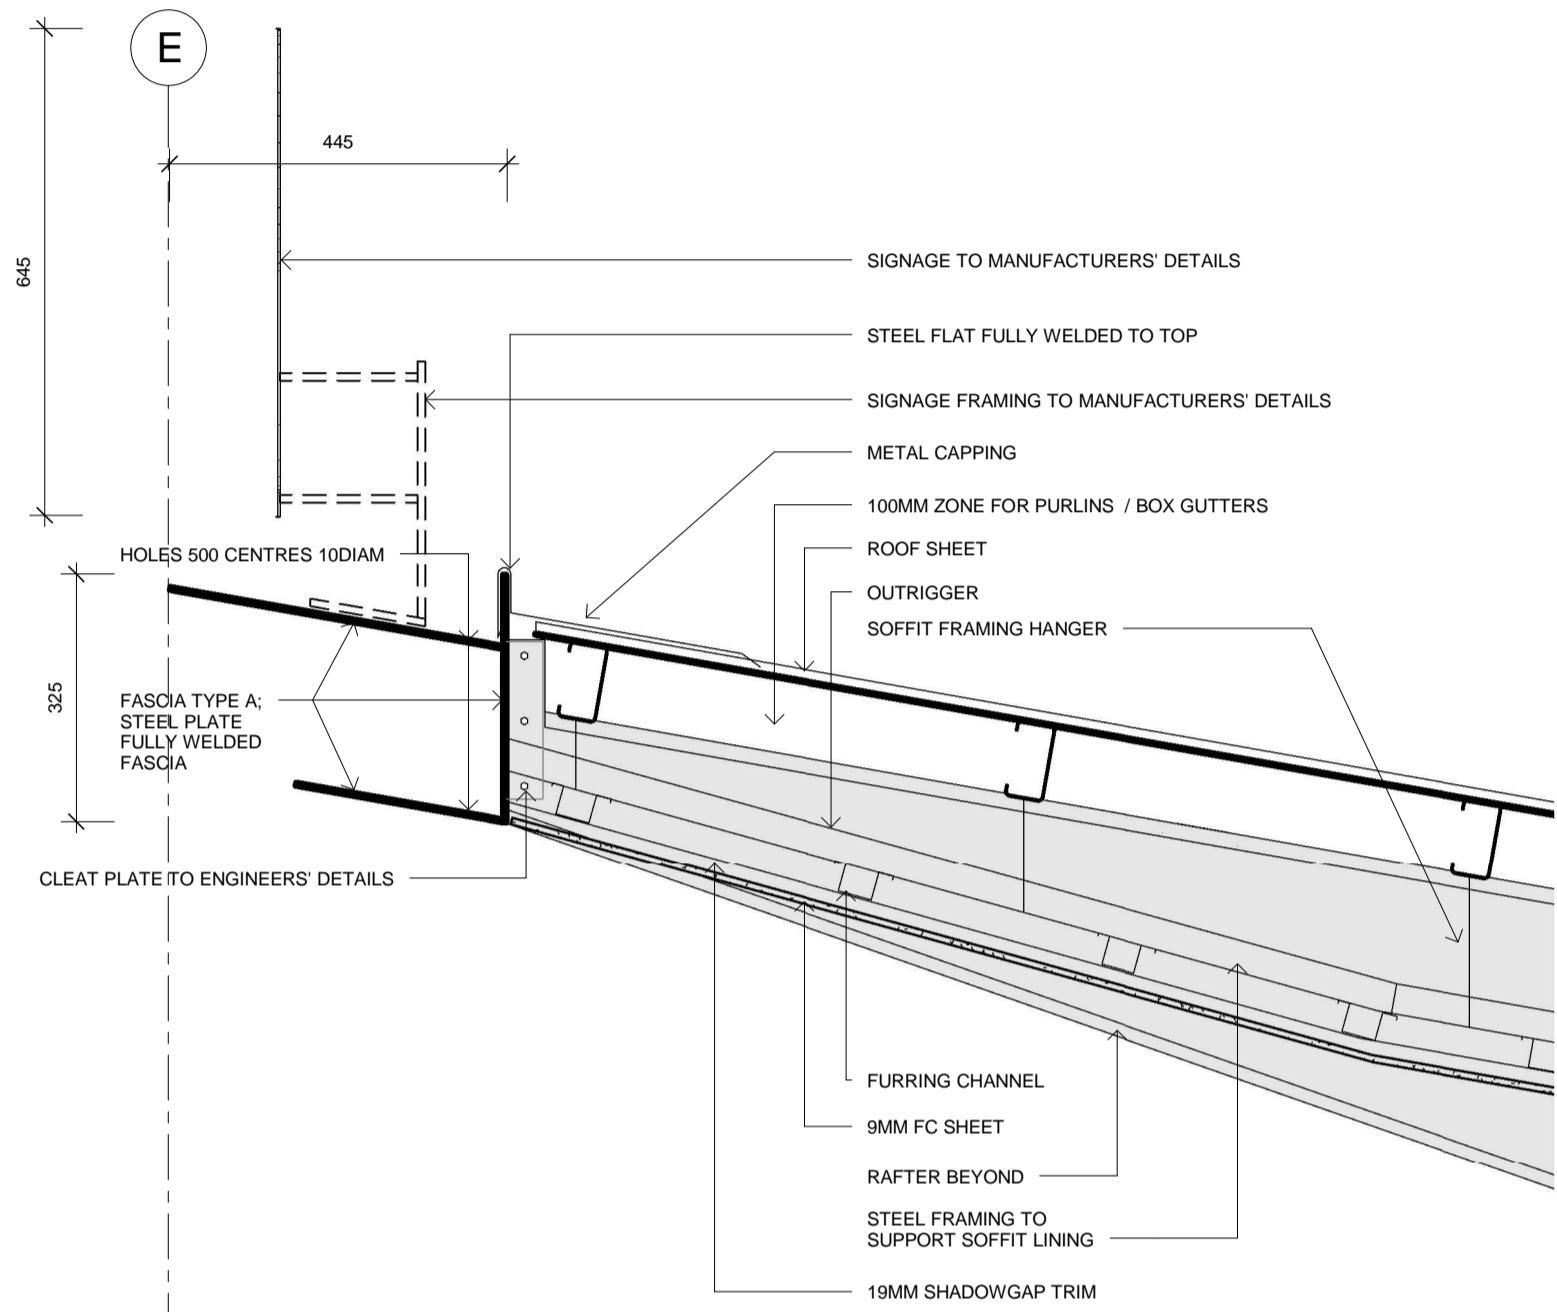

3
300 1 : 10

Canopy 1 Section Detail 3

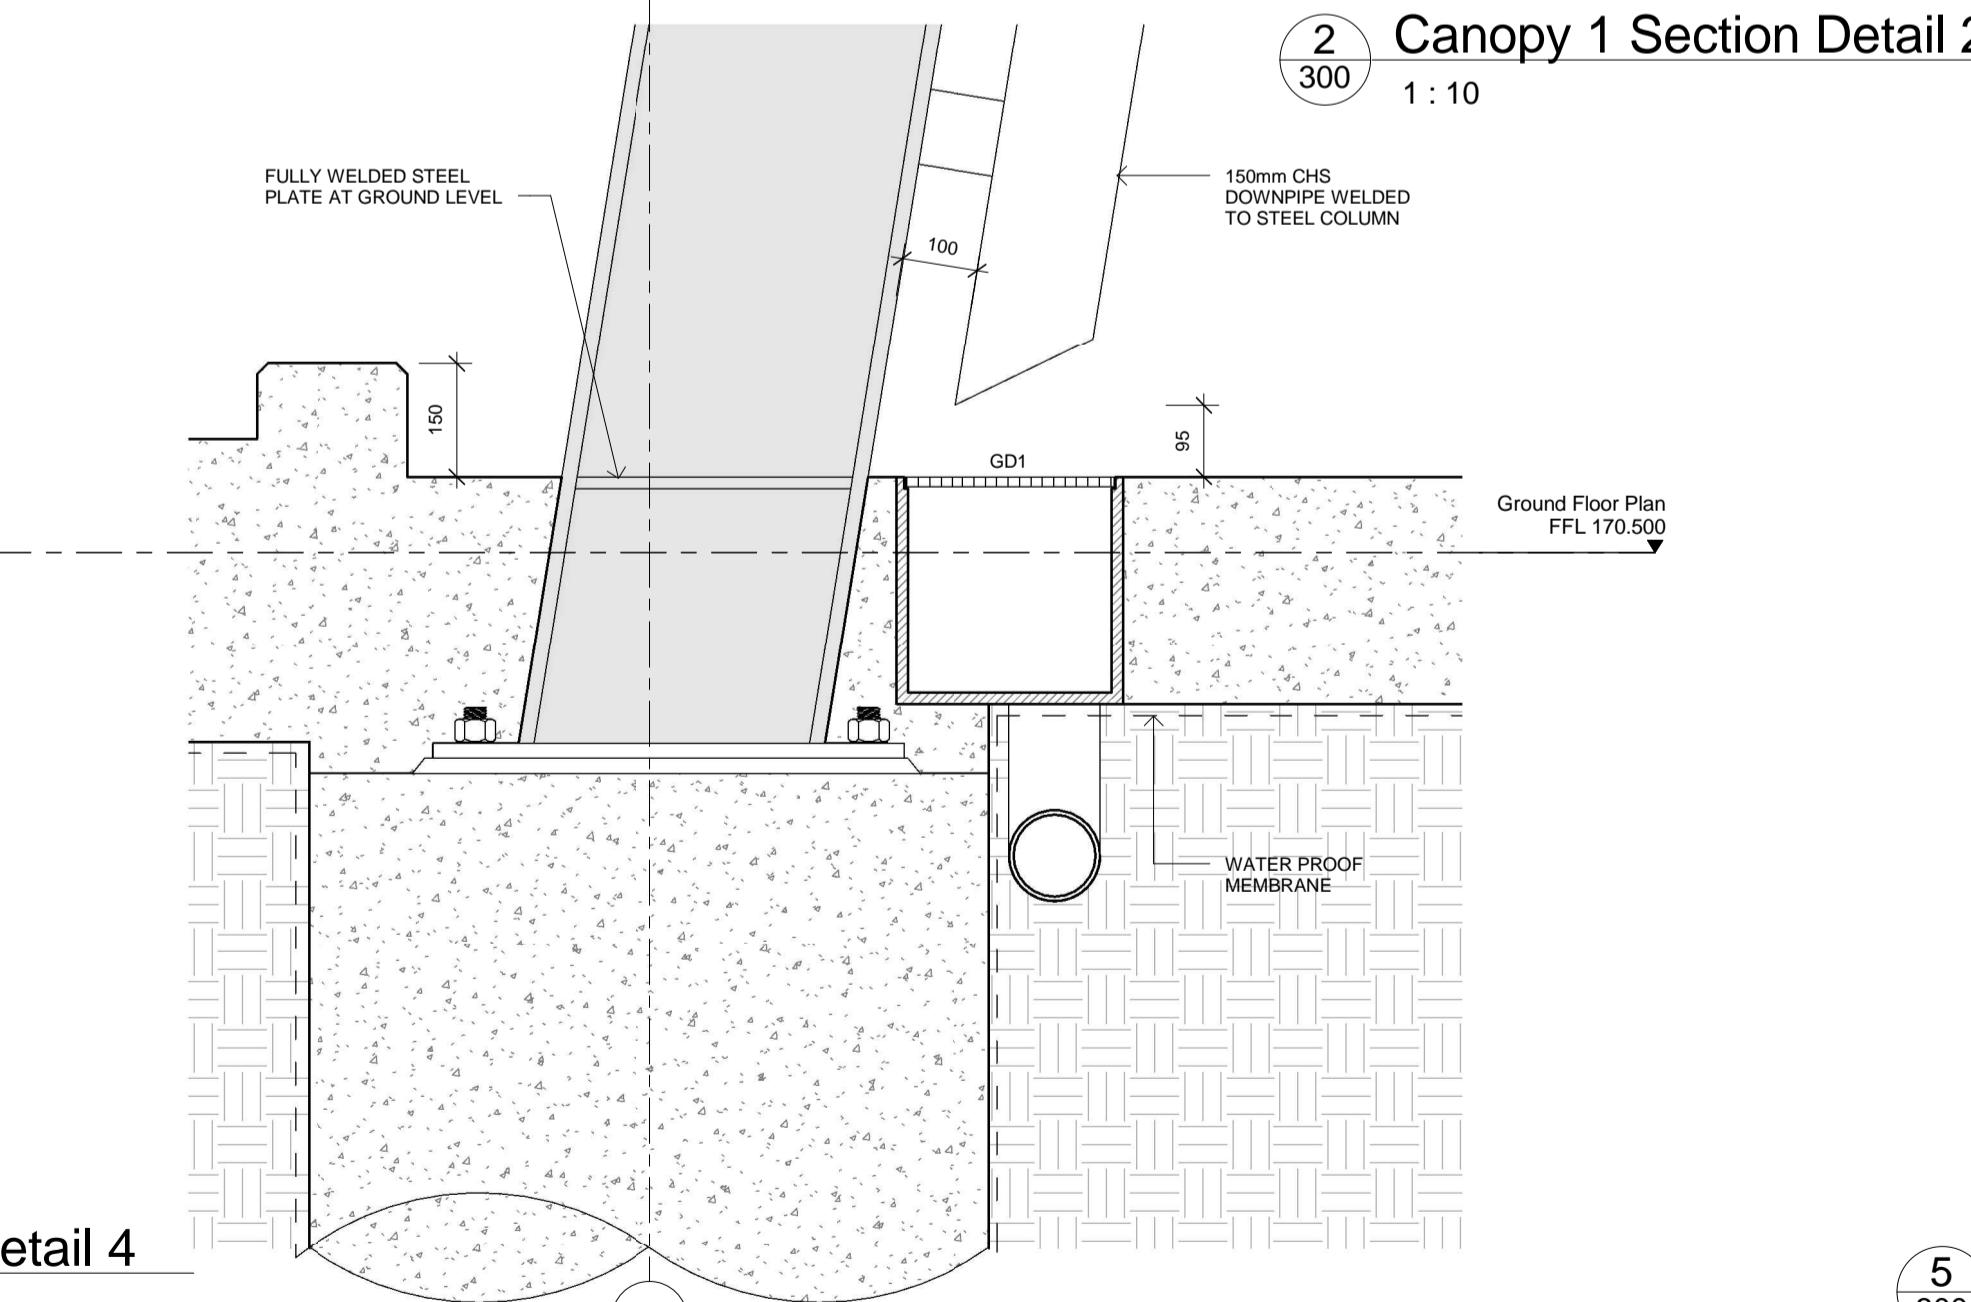

4
300 1 : 10

Canopy 1 Section Detail 4

TENDER ISSUE

Issue No. Date Description Chkd AT

A 31/08/16 TENDER ISSUE AT

Electrical Engineer
Ken Offord
601/90 George St, Hornsby, NSW
T: +61 2 9477 4300 F: 612 xxxx xxxx
E: ken@kroanda.com.au

Hydraulic Engineer
Sparks+Partners Consulting Engineers
Level 1, 91 George Street, Parramatta NSW
T: 0401 803 330 F: 612 xxxx xxxx
E: leon@sparksandpartners.com.au




Project Manager
Barker College
91 Pacific Highway, Hornsby, NSW, 2077
T: 02 9847 8318 F: 612 xxxx xxxx
E: georgia Rogers@barker.nsw.edu.au

Structural Engineer
Birzilis Associates
583 Darling Street Rozelle NSW 2039
T: 612 9555 7230 F: 612 xxxx xxxx
E: mgrogan@birzilisassociates.com

Drawing Title
Typical Canopy Details


Project & Client
BARKER OVAL C.O.L.A & AMENITIES UPGRADE
at
91 Pacific Hwy, Hornsby, NSW, 2077
for
BARKER COLLEGE

Architect
NBRSArchitecture.
Sydney 612 9922 2344 Melbourne 613 8676 0427
nbrsarchitecture.com.au
Any form of replication of this drawing in full or in part without the written permission of NBRSArchitecture Pty Ltd constitutes an infringement of the copyright ABN 16 002 247 505
© 2016 Nominated Architects: Geoffrey Deane 3766; Andrew Duffin 5602; Garry Hodnett 5286

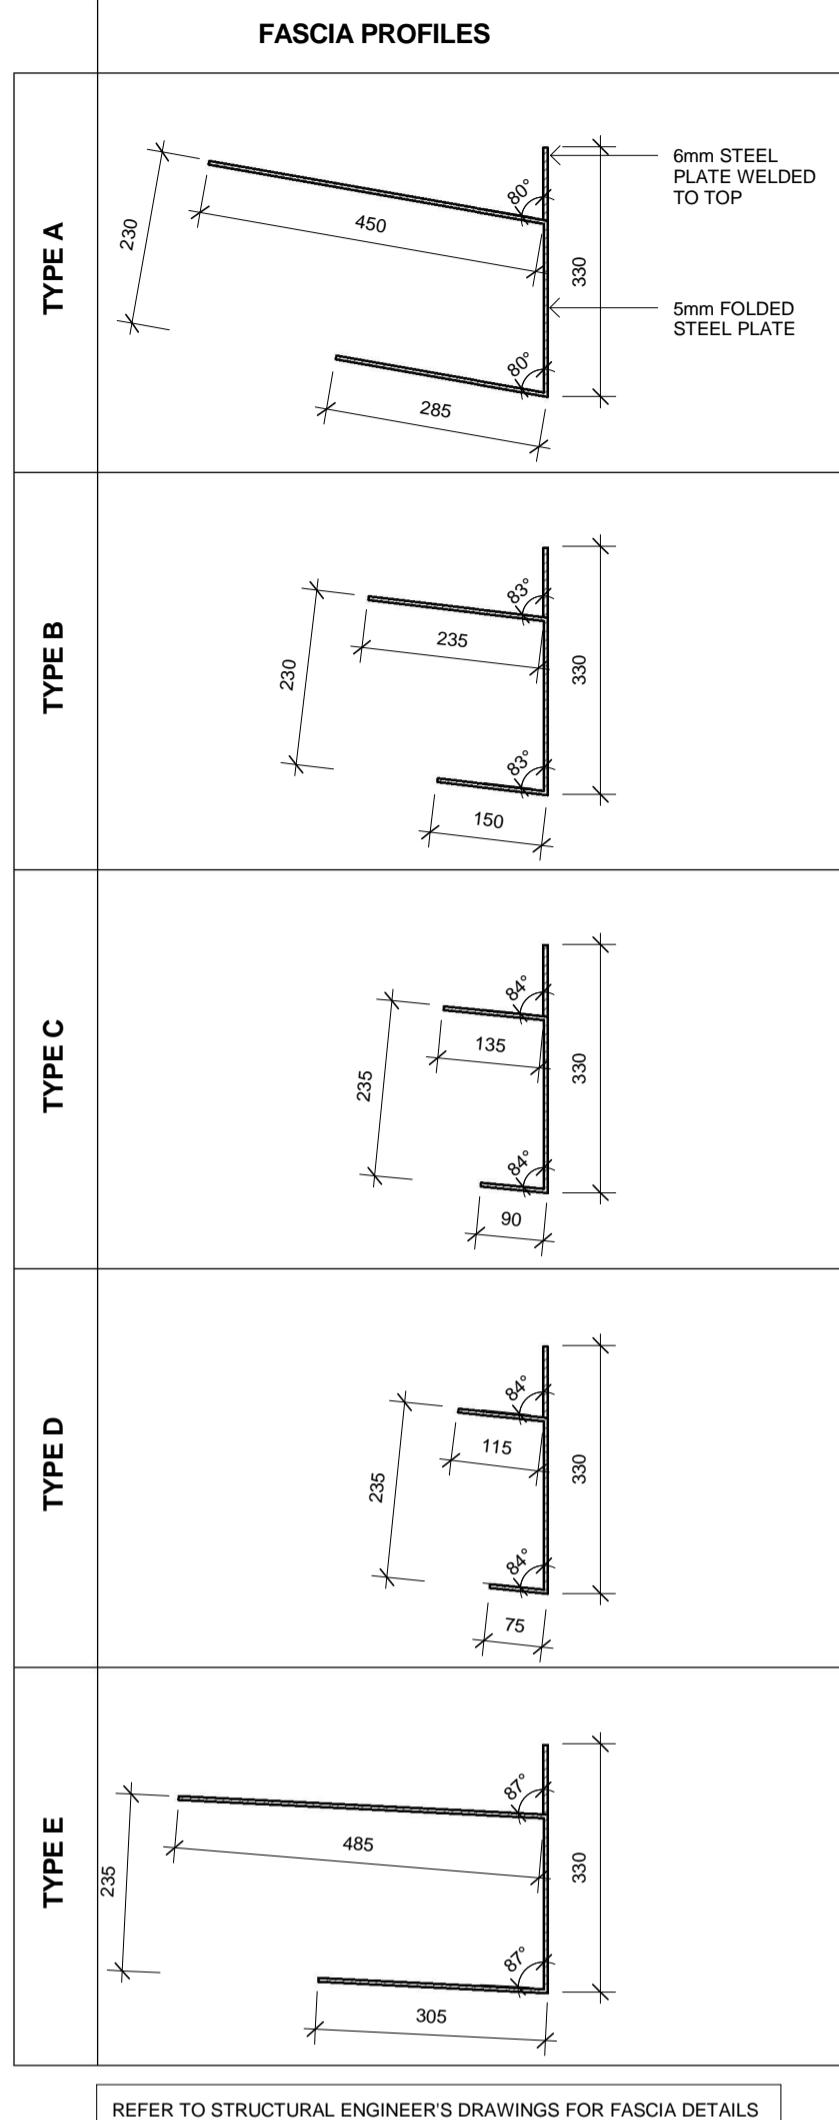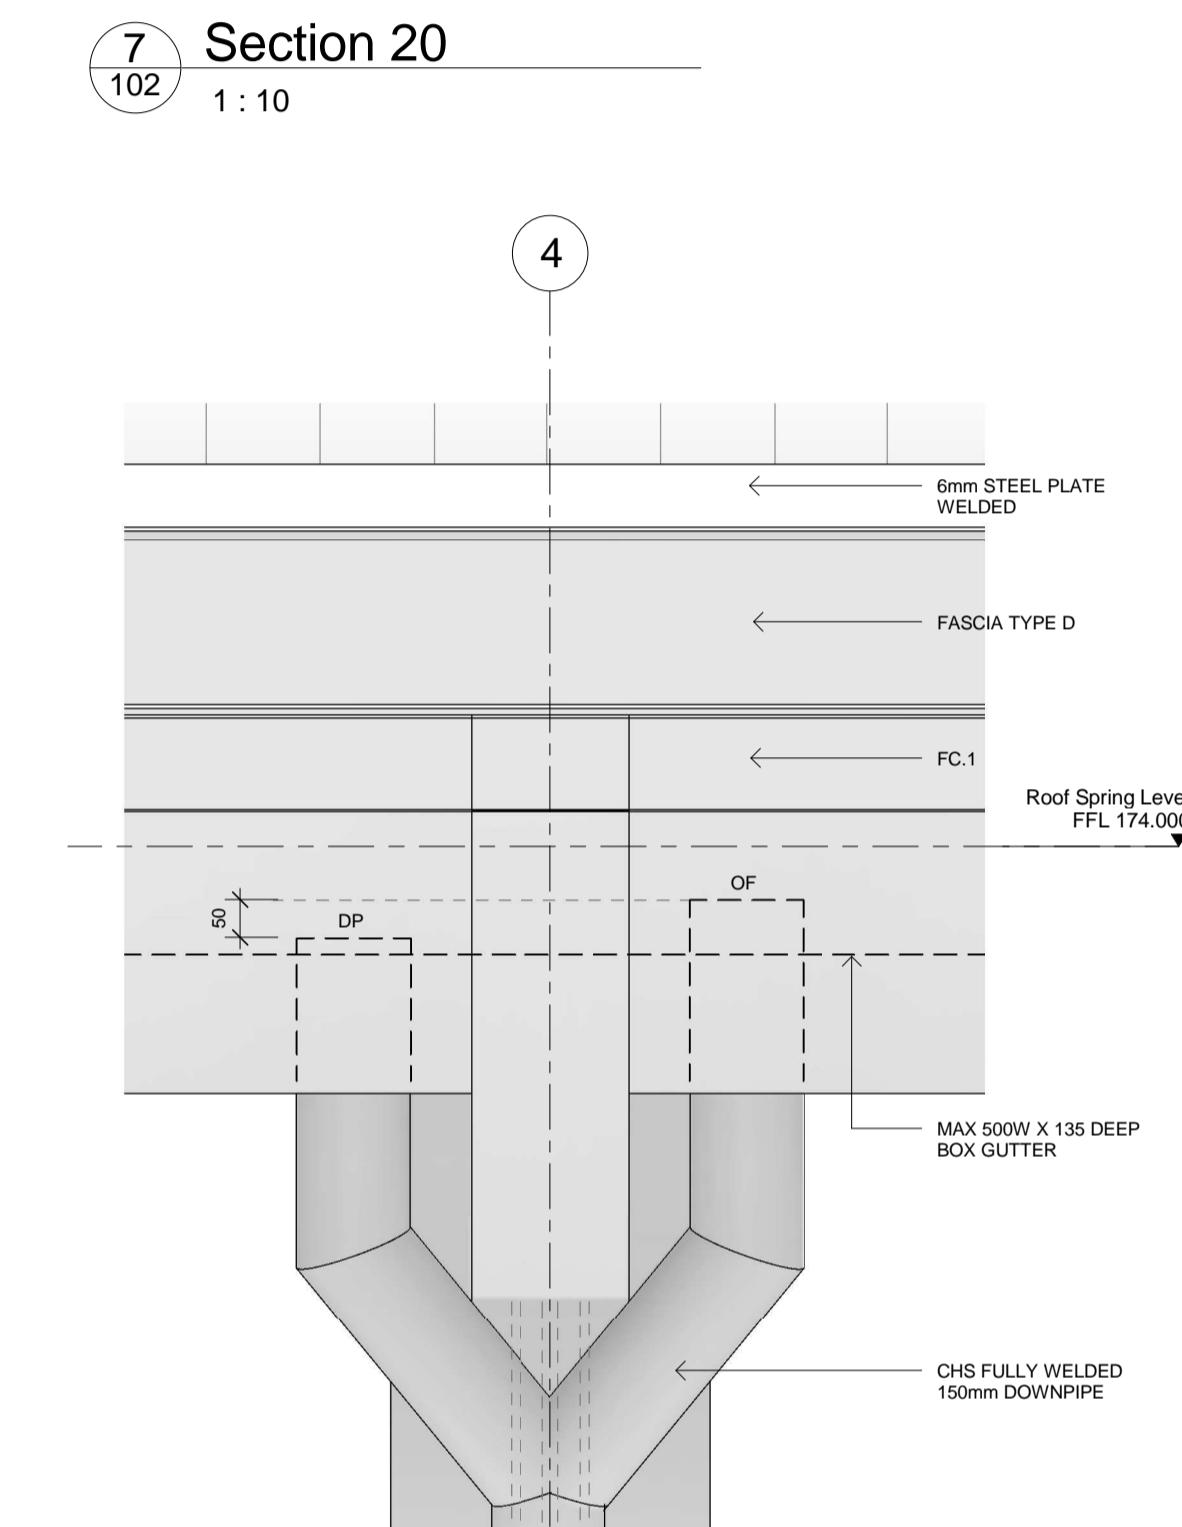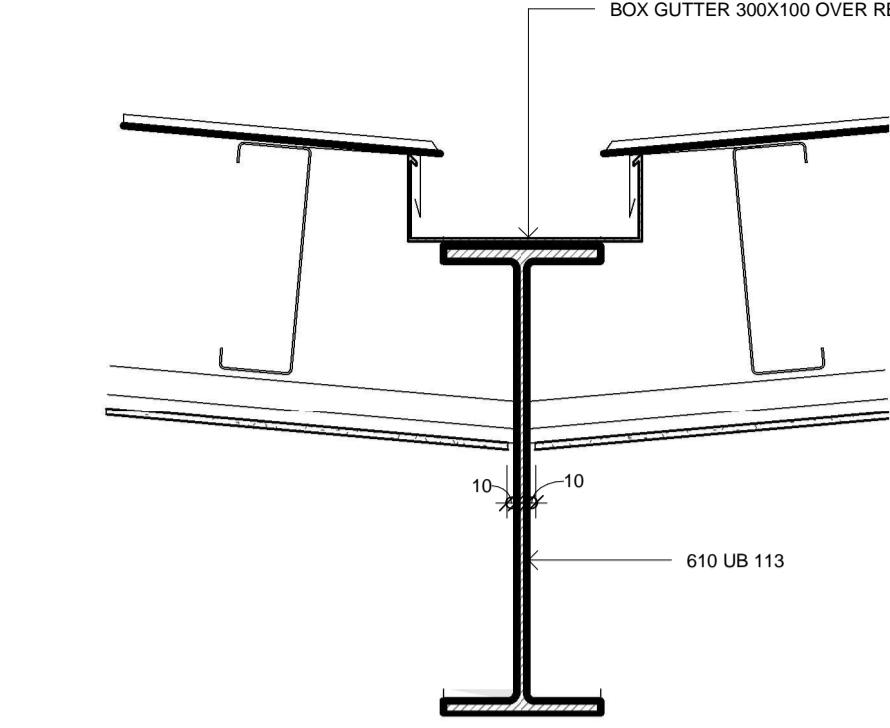

9
1 : 10


Fascia Types

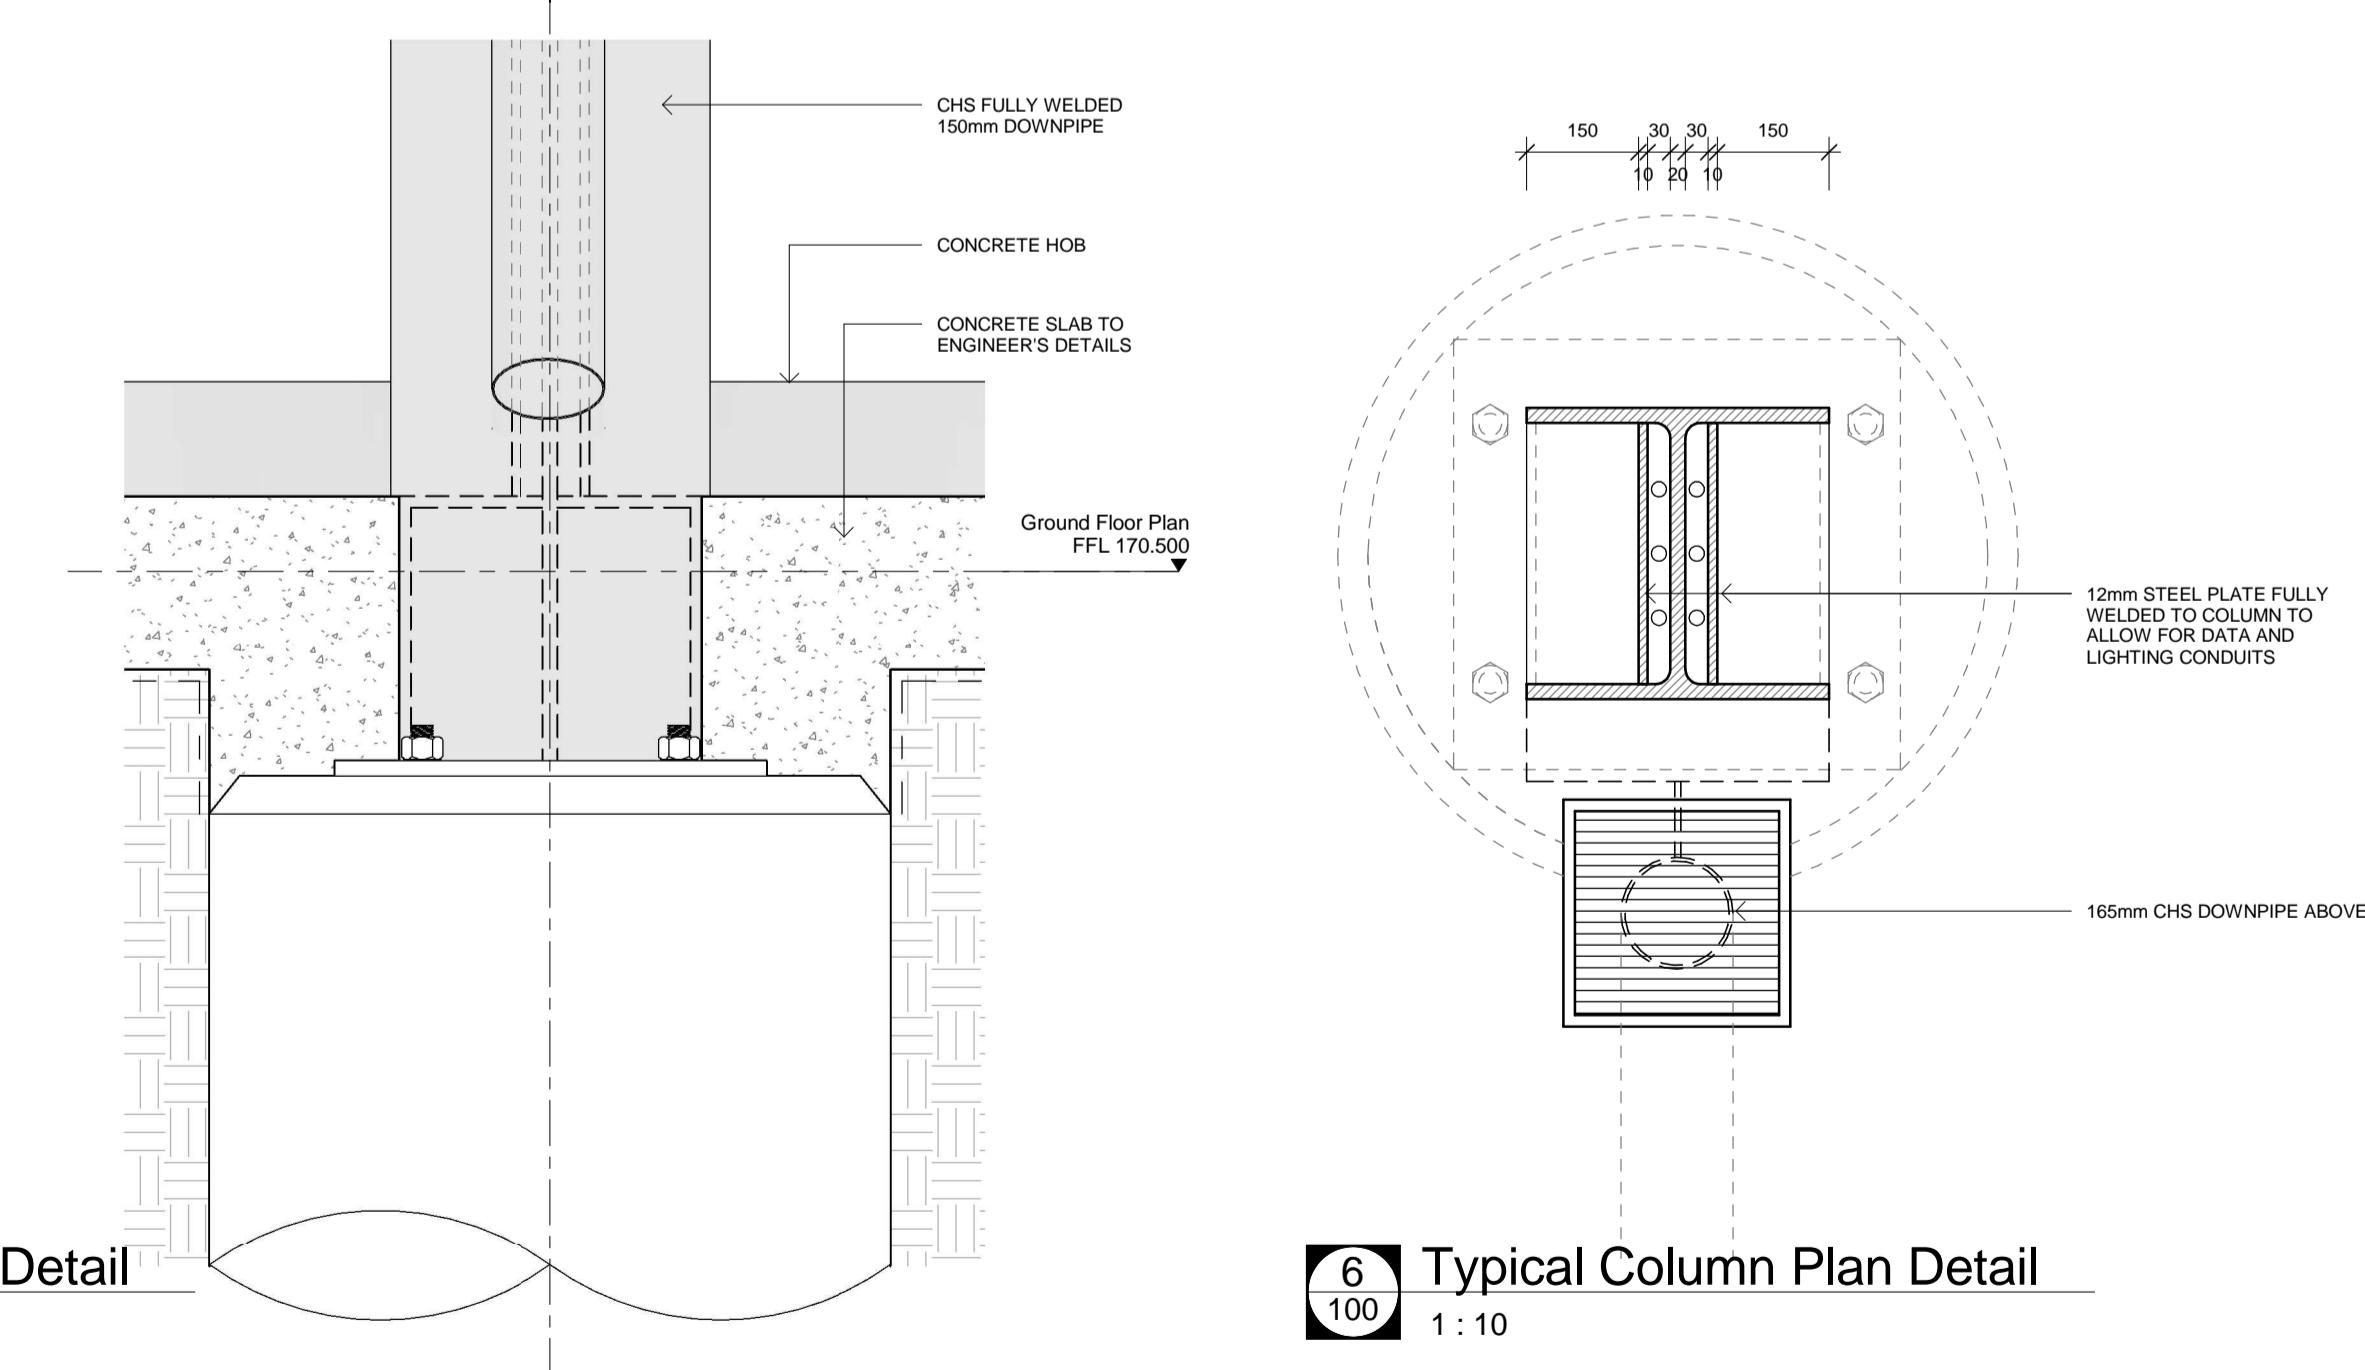


Date 31/08/2016 5:39:16 PM
Scale 1 : 10 @ A1
0 1m 2m 3m 4m 5m 6m

Drawing Reference

15494-WD 500 - A

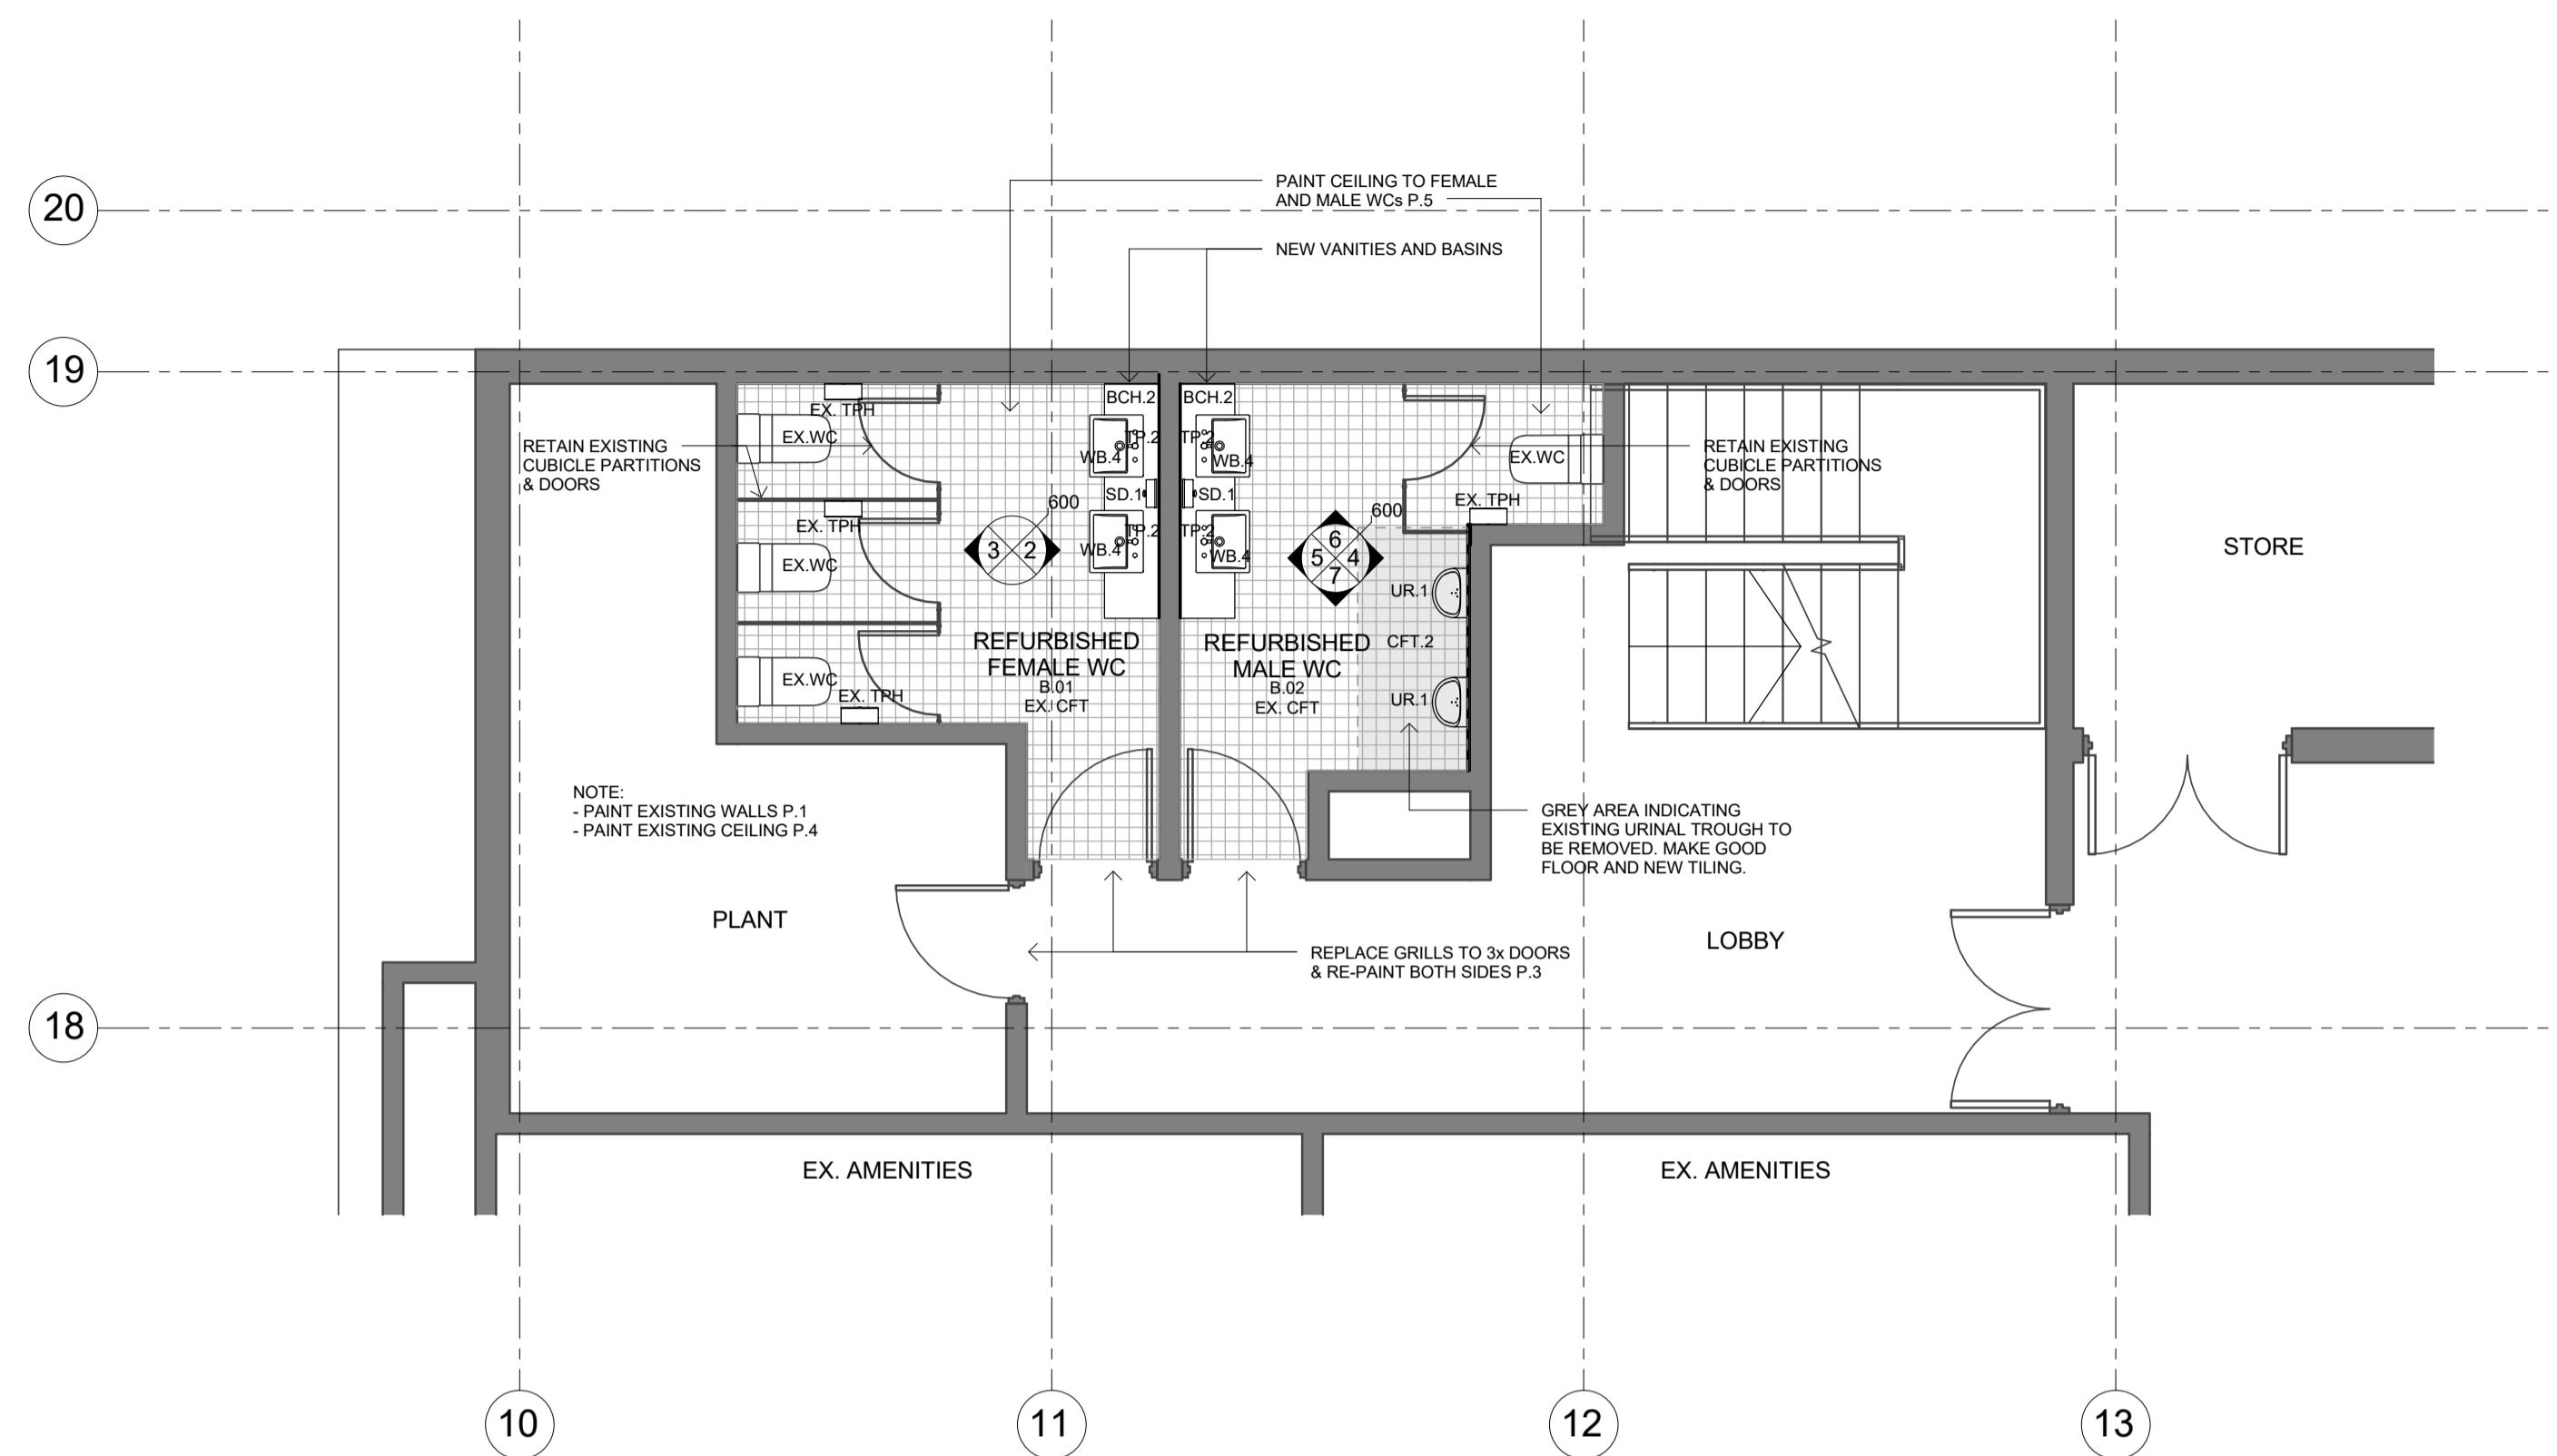

1 Lower Ground Plan - Marks Pavilion
1 : 50

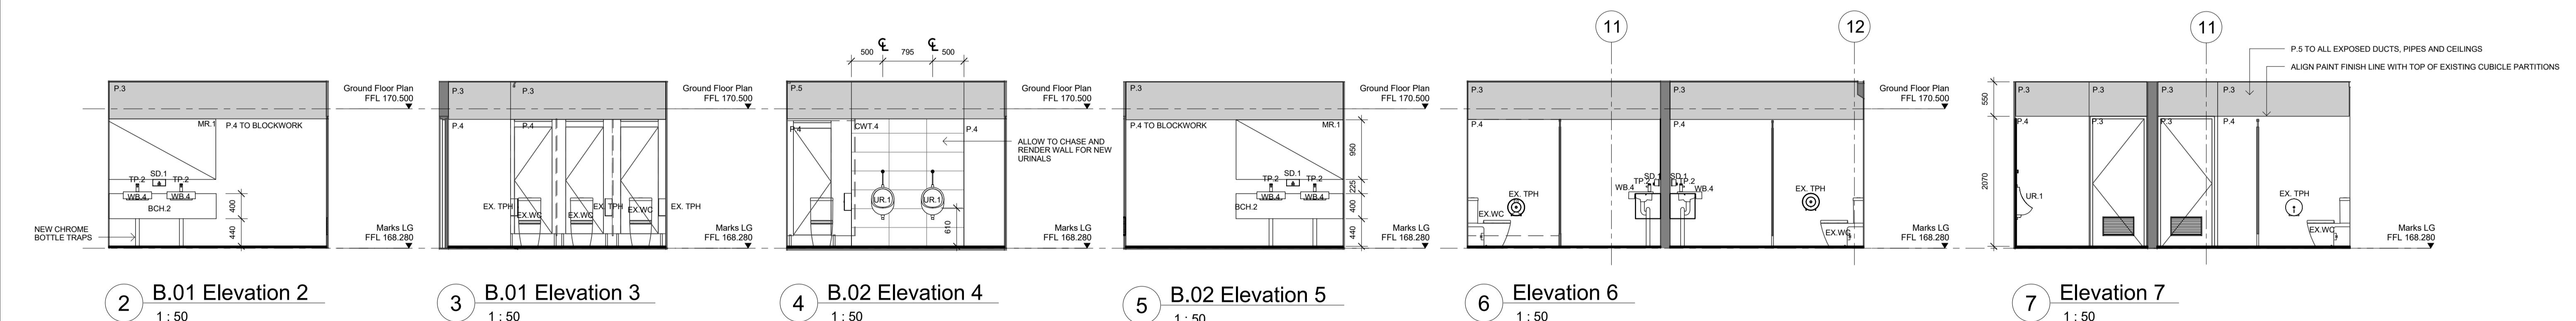

Issue No. Date Description Chkd AT

TENDER ISSUE

Electrical Engineer
Ken Offord
601/90 George St, Hornsby, NSW
T: 61 2 9447 4300 F: 61 2 xxxx xxxx
E: offord@bigpond.com

Hydraulic Engineer
Sparks + Partners
Level 1, 91 George Street, Parramatta, NSW
T: 0401 803 330 F: 61 2 9887 3898
E: Leon@sparksandpartners.com.au

Project Manager
Barker College
91 Pacific Highway, Hornsby, NSW, 2077
T: 61 2 9847 8318 F: 61 2 xxxx xxxx
E: georgina_rogers@barker.nsw.edu.au

Structural Engineer
Birzulis Associates
583 Darling Street, Rozelle, NSW, 2039
T: 61 2 9555 7230 F: 61 2 xxxx xxxx
E: mgrogan@birzulisassociates.com

Drawing Title
Lower Ground Plan - Marks Pavilion Amenities

Project & Client
BARKER COLLEGE AMENITIES UPGRADE
at
91 Pacific Hwy, Hornsby, NSW, 2077
for
BARKER COLLEGE

Architect
NBRSArchitecture.
Sydney Melbourne
61 2 9922 2344 61 3 8676 0427
nbrsarchitecture.com.au


Any form of replication of this drawing in full or in part without the written permission of NBRSA+PARTNERS Pty Ltd constitutes an infringement of the copyright
ABN 16 002 247 365 © 2016
Nominated Architects: Geoffrey Deane 3766; Andrew Duffin 5602; Garry Hodnett 5286

Date 31/08/2016 5:20:39 PM
Scale 1 : 50 @ A1
0 1m 2m 3m 4m 5m 6m
Drawing Reference
15494-WD 600-A1




1 Phipps Field Demolition Plan

1 : 50

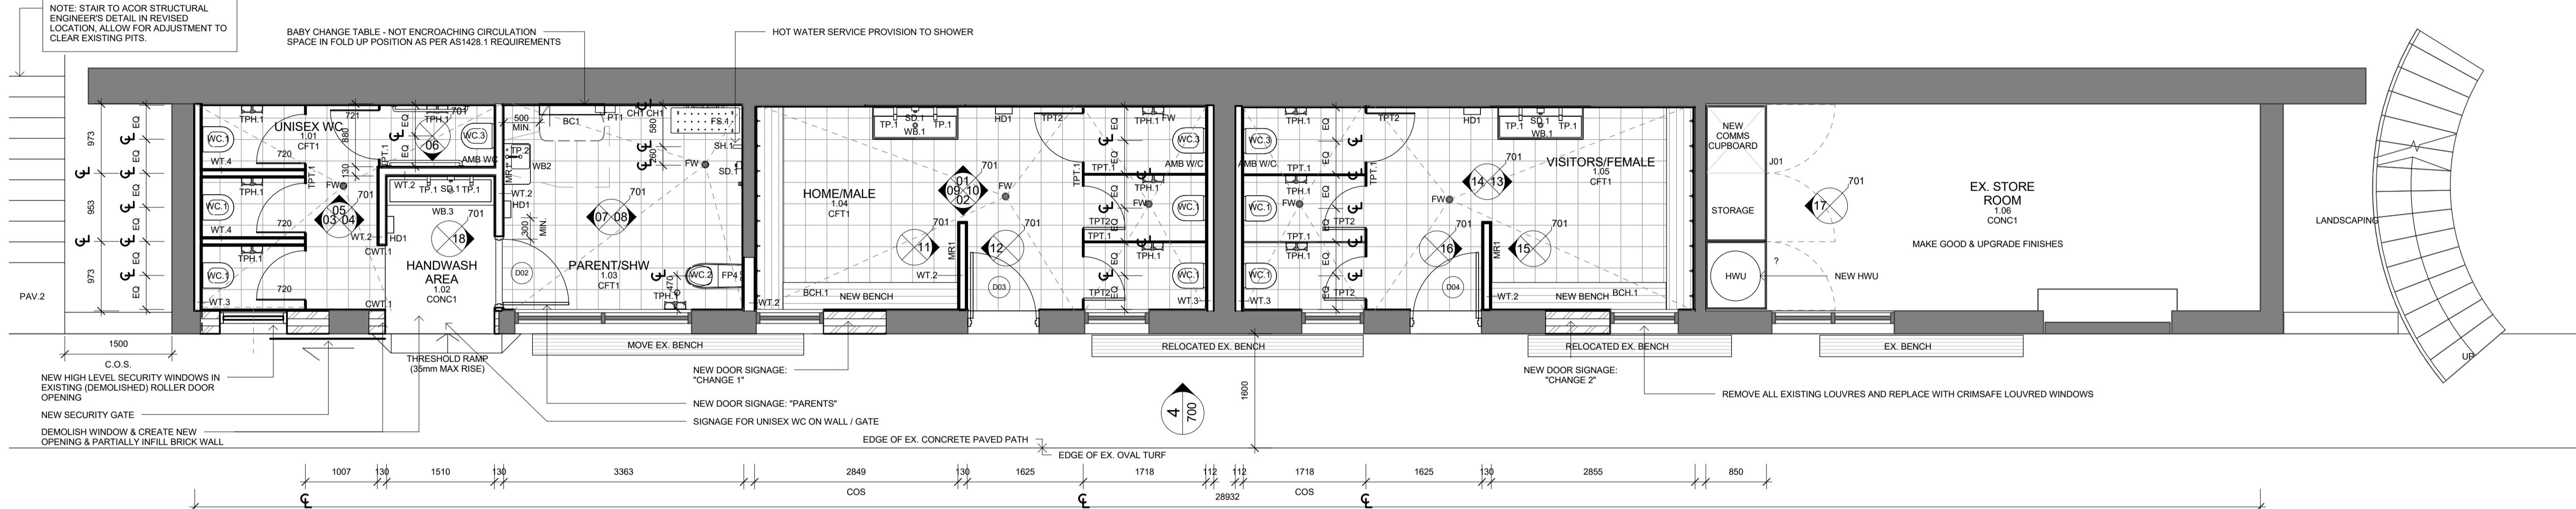


2 Phipps Field Proposed Floor Plan

1 : 50

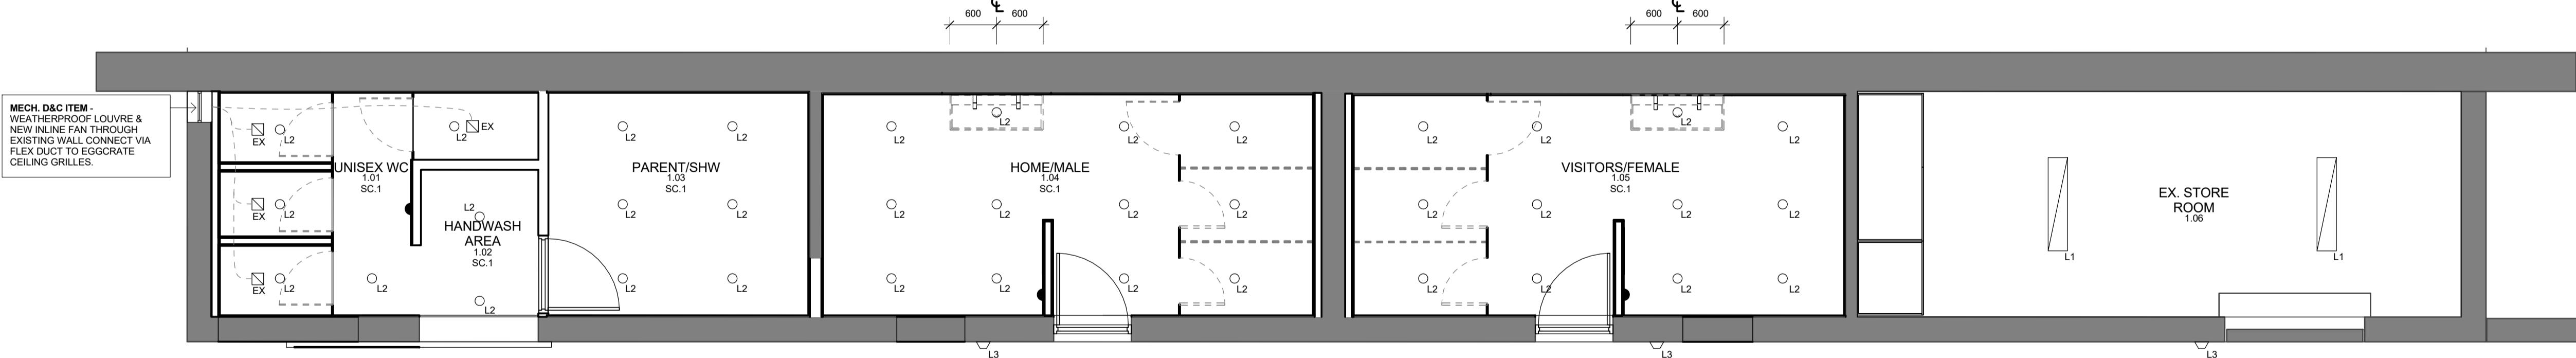

3 Phipps Field Amenities RCP

1 : 50

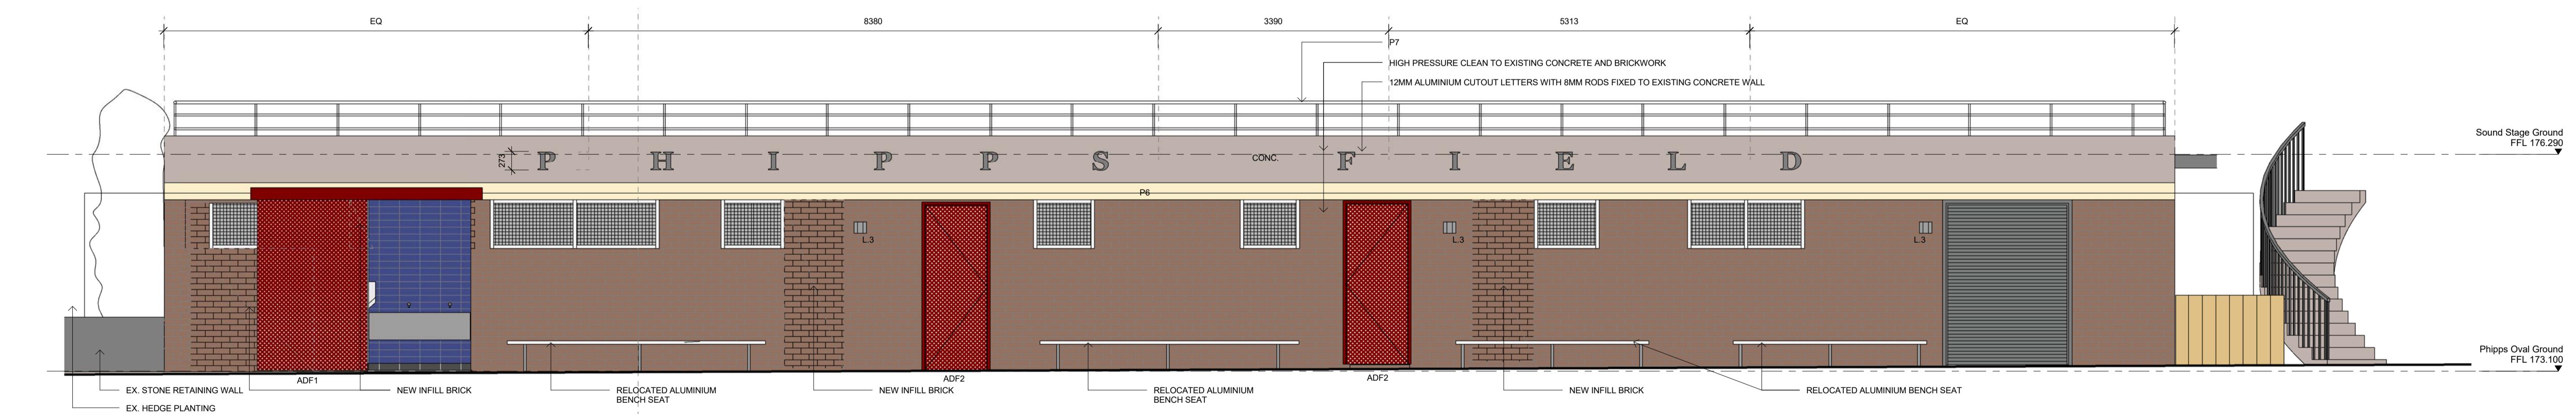

4 South Elevation

1 : 50

Issue No.	Date	Description	Chkd AT
A	31/08/2016	TENDER ISSUE	

TENDER ISSUE

Electrical Engineer
Ken Offord
60/90 George St, Hornsby, NSW
T: 61 2 8447 4300 F: 61 2 xxxx xxxx
E: offord@bigpond.com

Hydraulic Engineer
Sparks + Partners
Level 1, 91 George Street, Parramatta, NSW
T: 0401 803 330 F: 61 2 9881 3898
E: Leon@sparksandpartners.com.au





Project Manager
Barker College
91 Pacific Highway, Hornsby, NSW, 2077
T: 61 2 9847 8318 F: 61 2 xxxx xxxx
E: georgia_regoes@barker.nsw.edu.au

Drawing Title
Existing & Proposed - Phipps Field Amenities


Project & Client
BARKER COLLEGE AMENITIES UPGRADE
at
91 Pacific Hwy, Hornsby, NSW, 2077
for
BARKER COLLEGE

Architect
NBRSArchitecture.
Sydney 61 2 9922 2344 Melbourne 61 3 8676 0427
nbrsarchitecture.com.au
Any form of replication of this drawing in full or in part without the written permission of NBRSA+PARTNERS Pty Ltd constitutes an infringement of the copyright
ABN 16 003 247 365 © 2016
Nominated Architects: Geoffrey Deane 3766; Andrew Duffin 5602; Garry Hodnett 5286


Date 31/08/2016 5:20:44 PM
Scale 1 : 50 @ A1
0 1m 2m 3m 4m 5m 6m
Drawing Reference 15494-WD 700 -A
15494-WD 700 -A

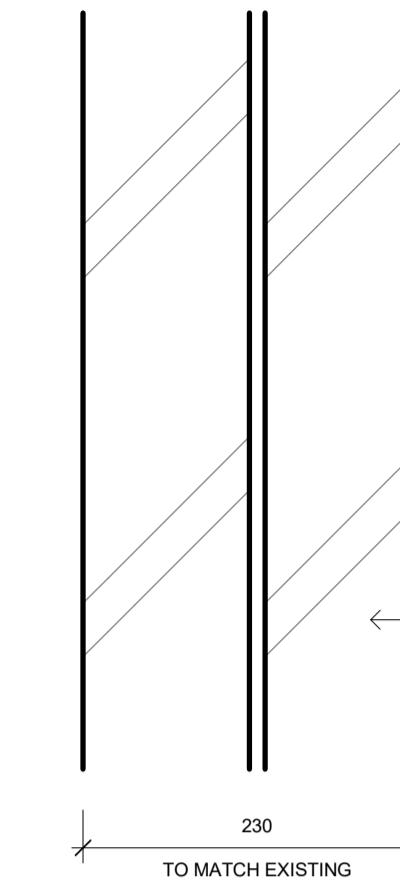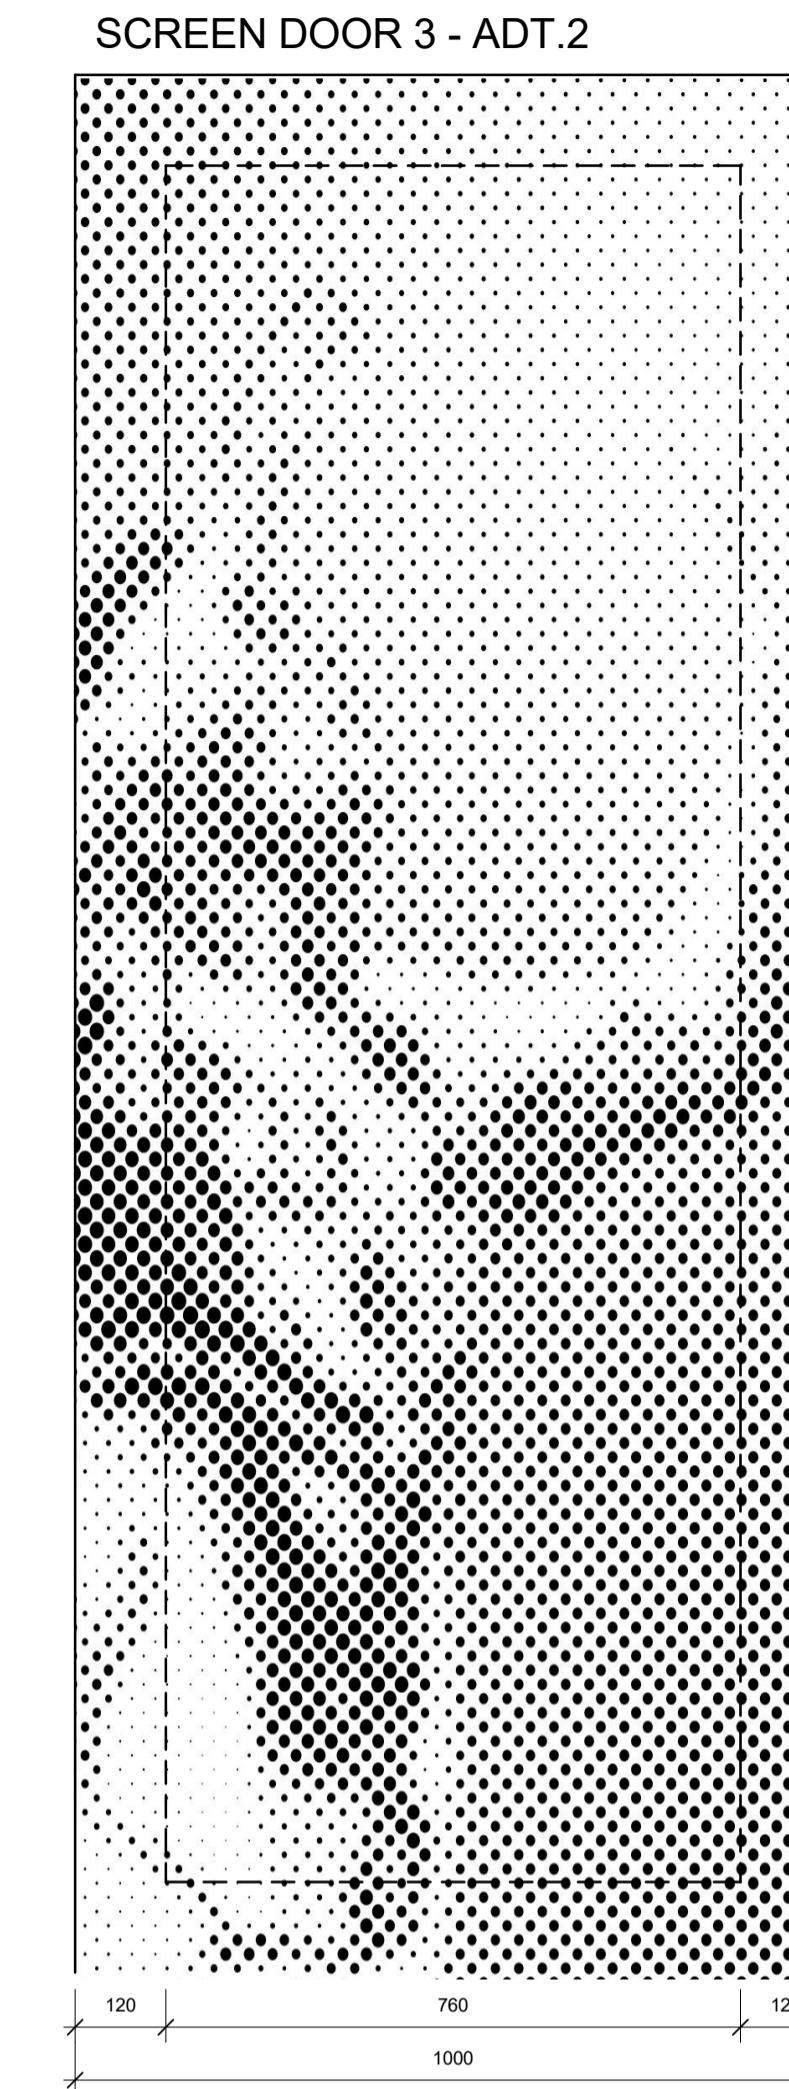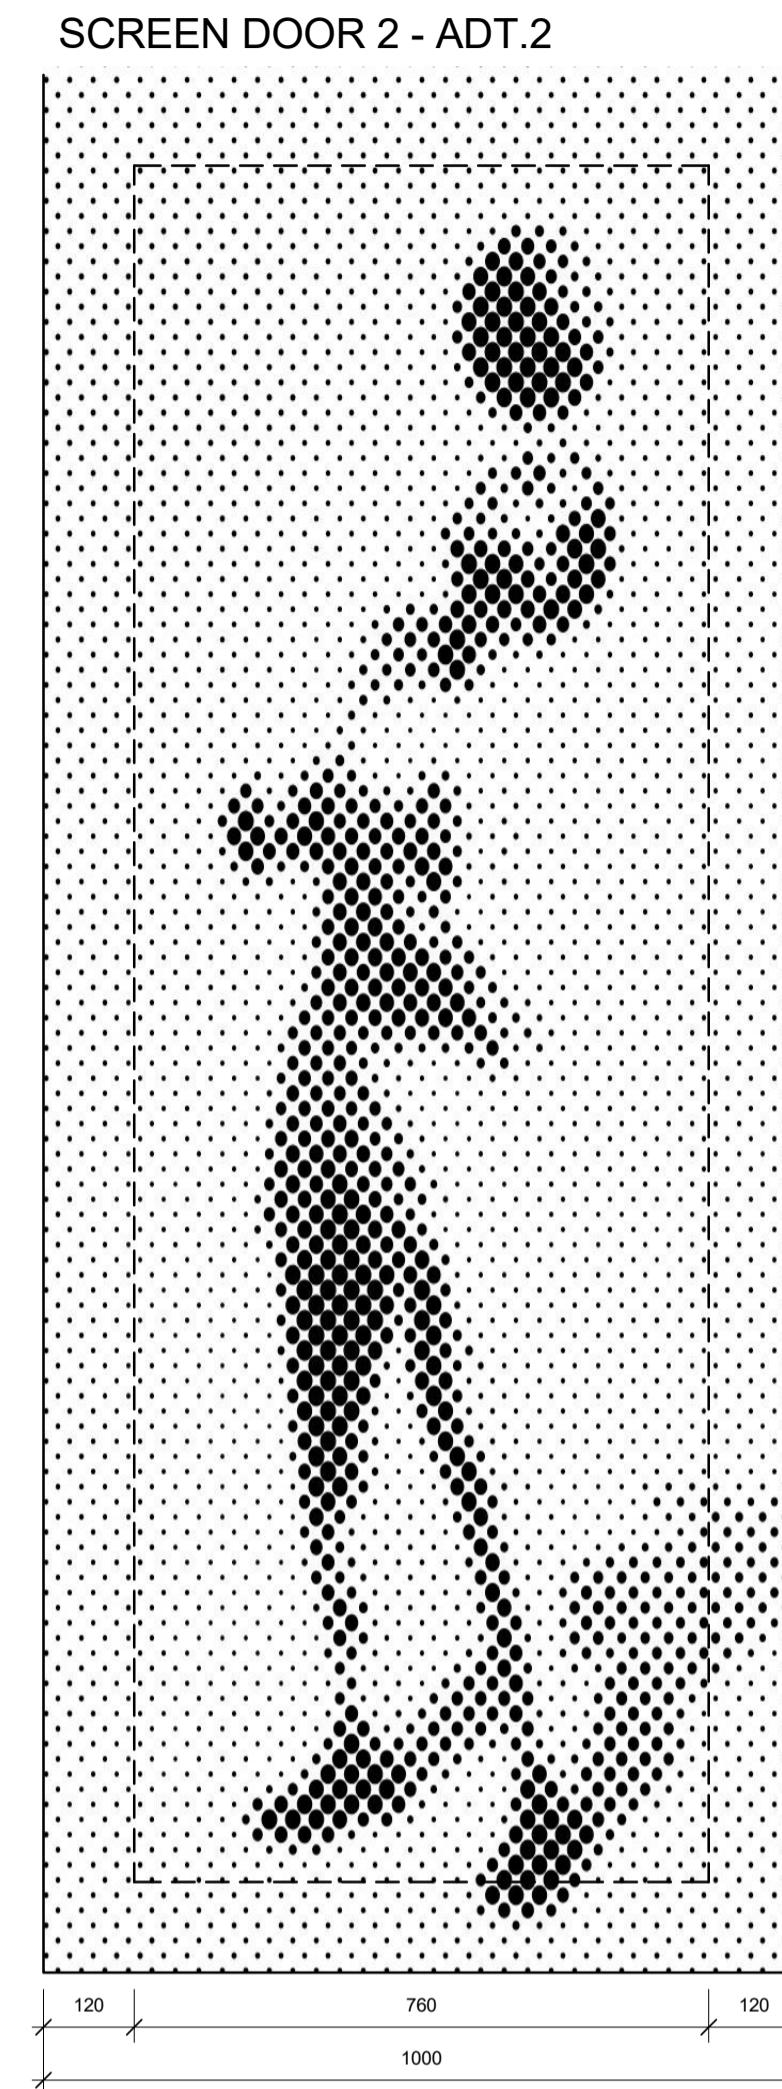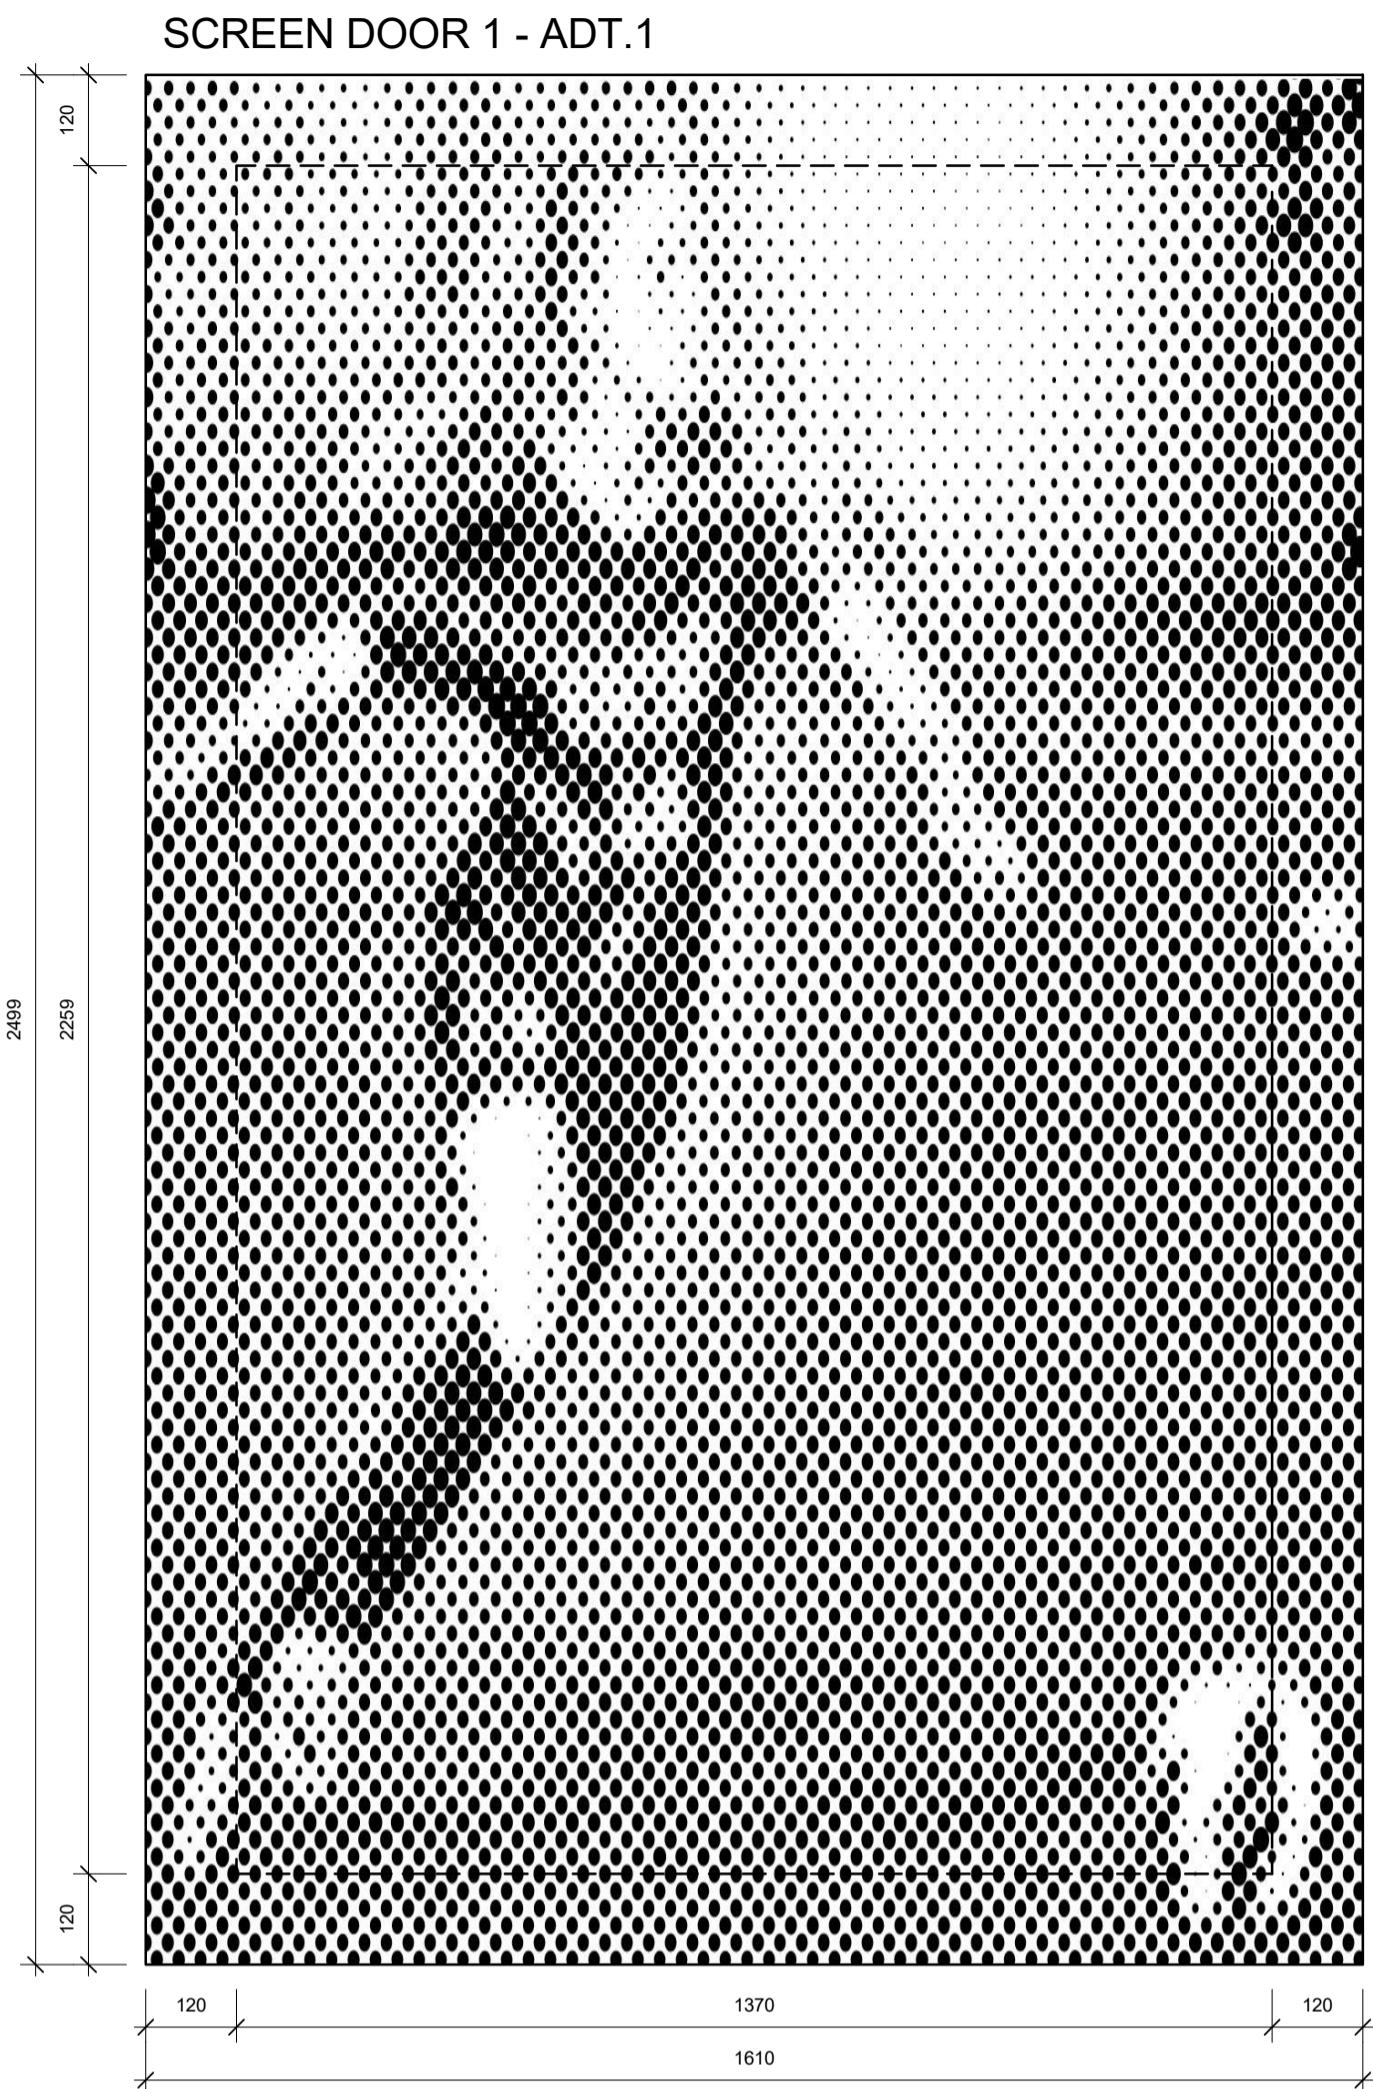


1 WT1
1 : 5

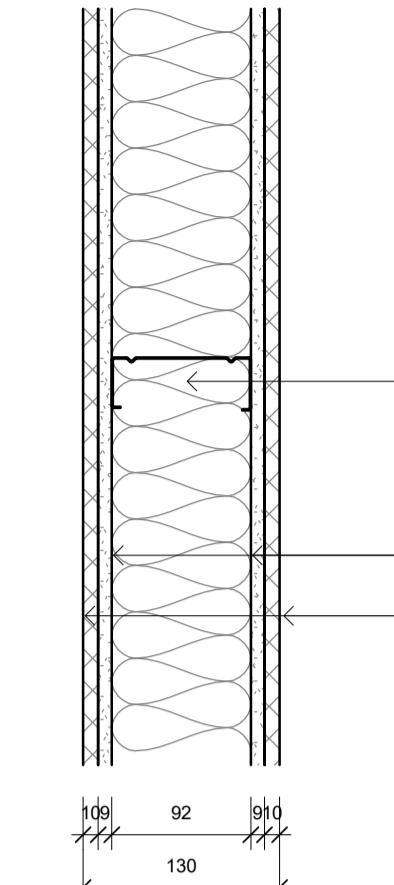


2 WT2
1 : 5

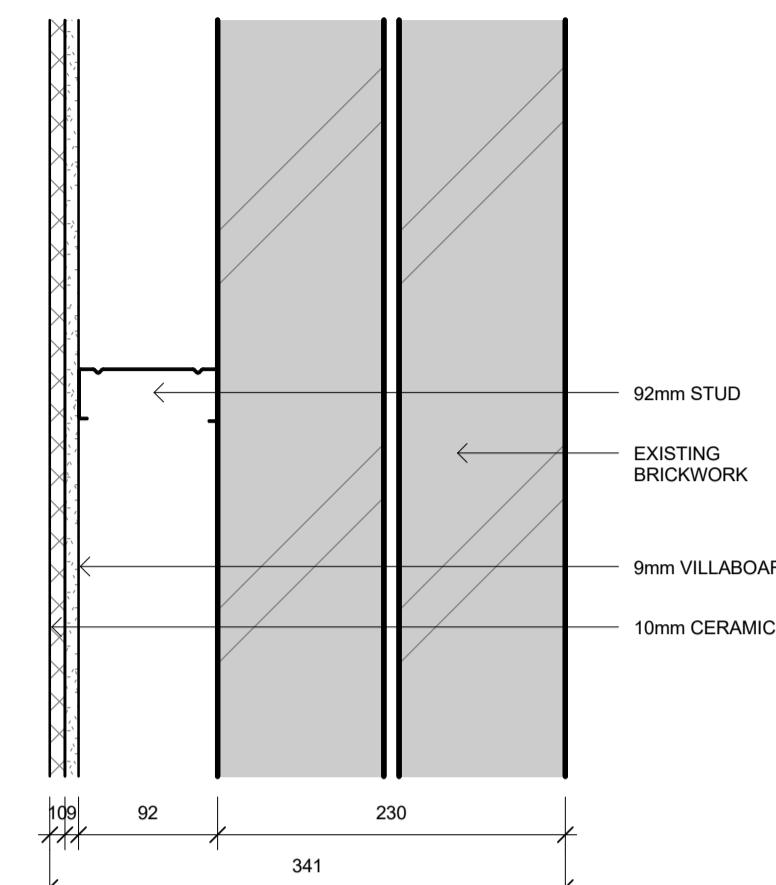


3 WT3
1 : 5

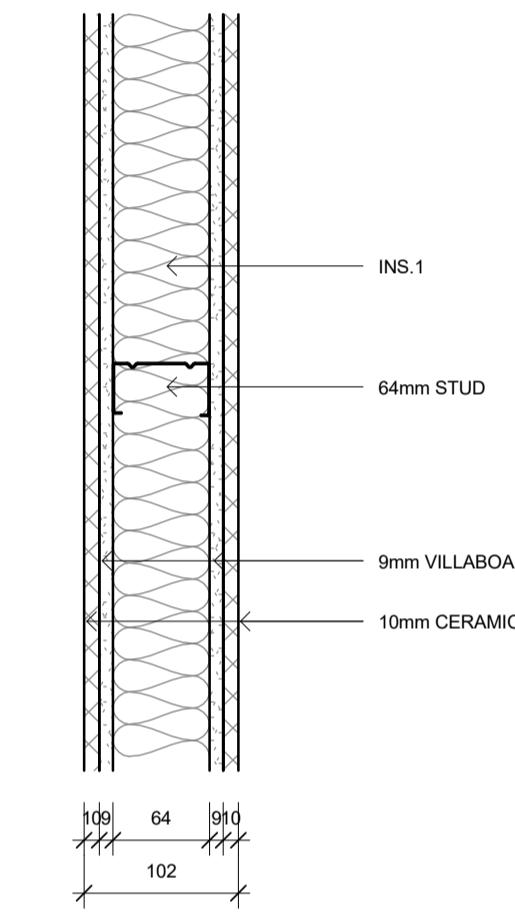



4 WT4
1 : 5

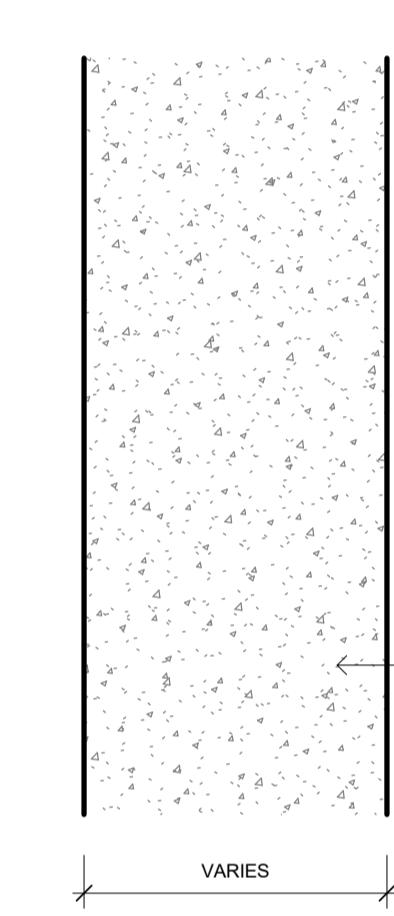

5 WT5
1 : 5

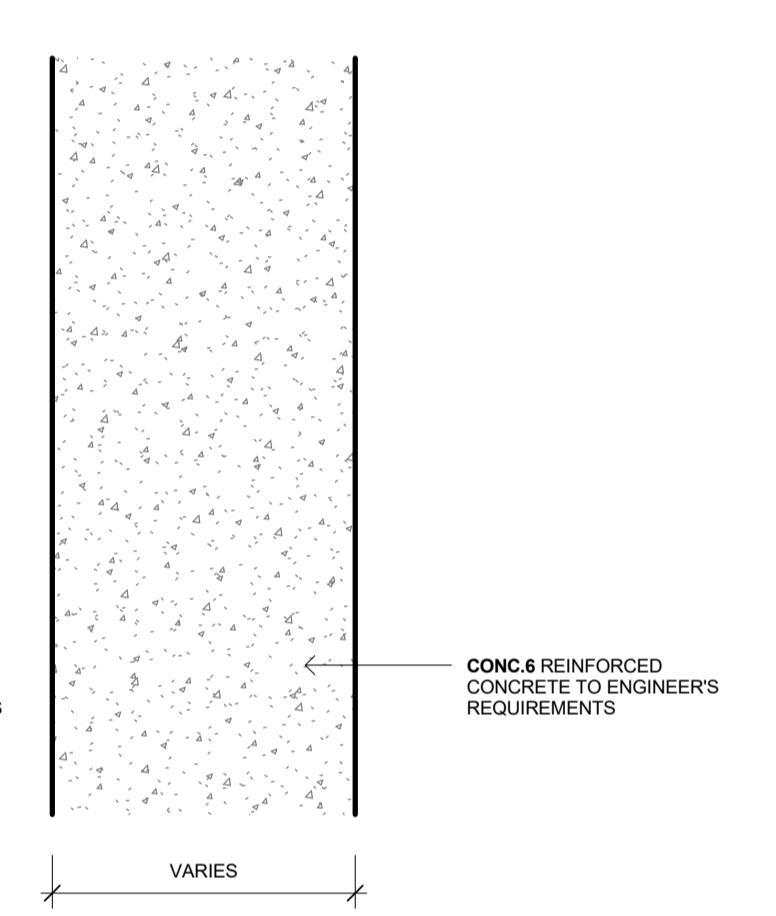

6 WT6
1 : 5

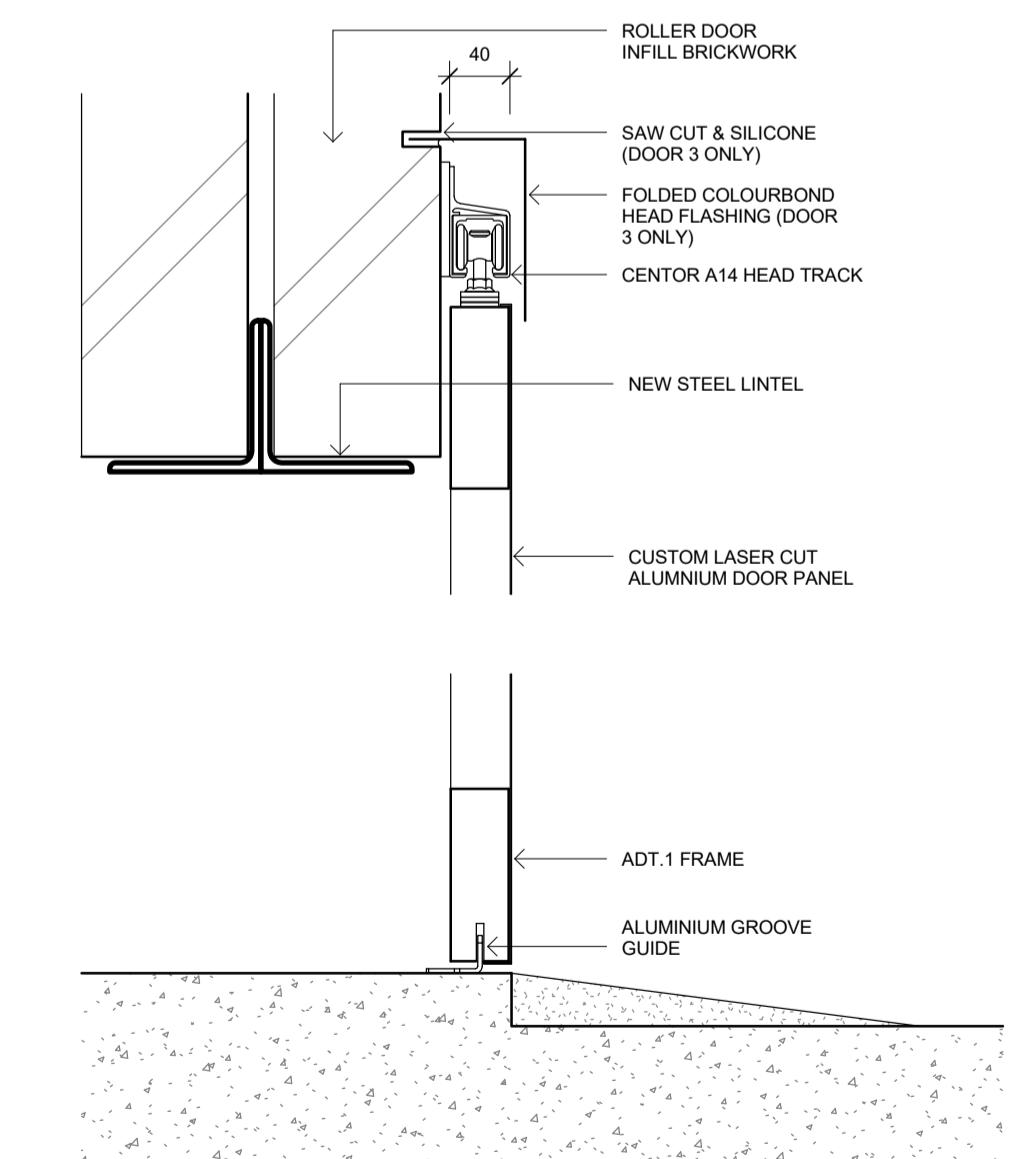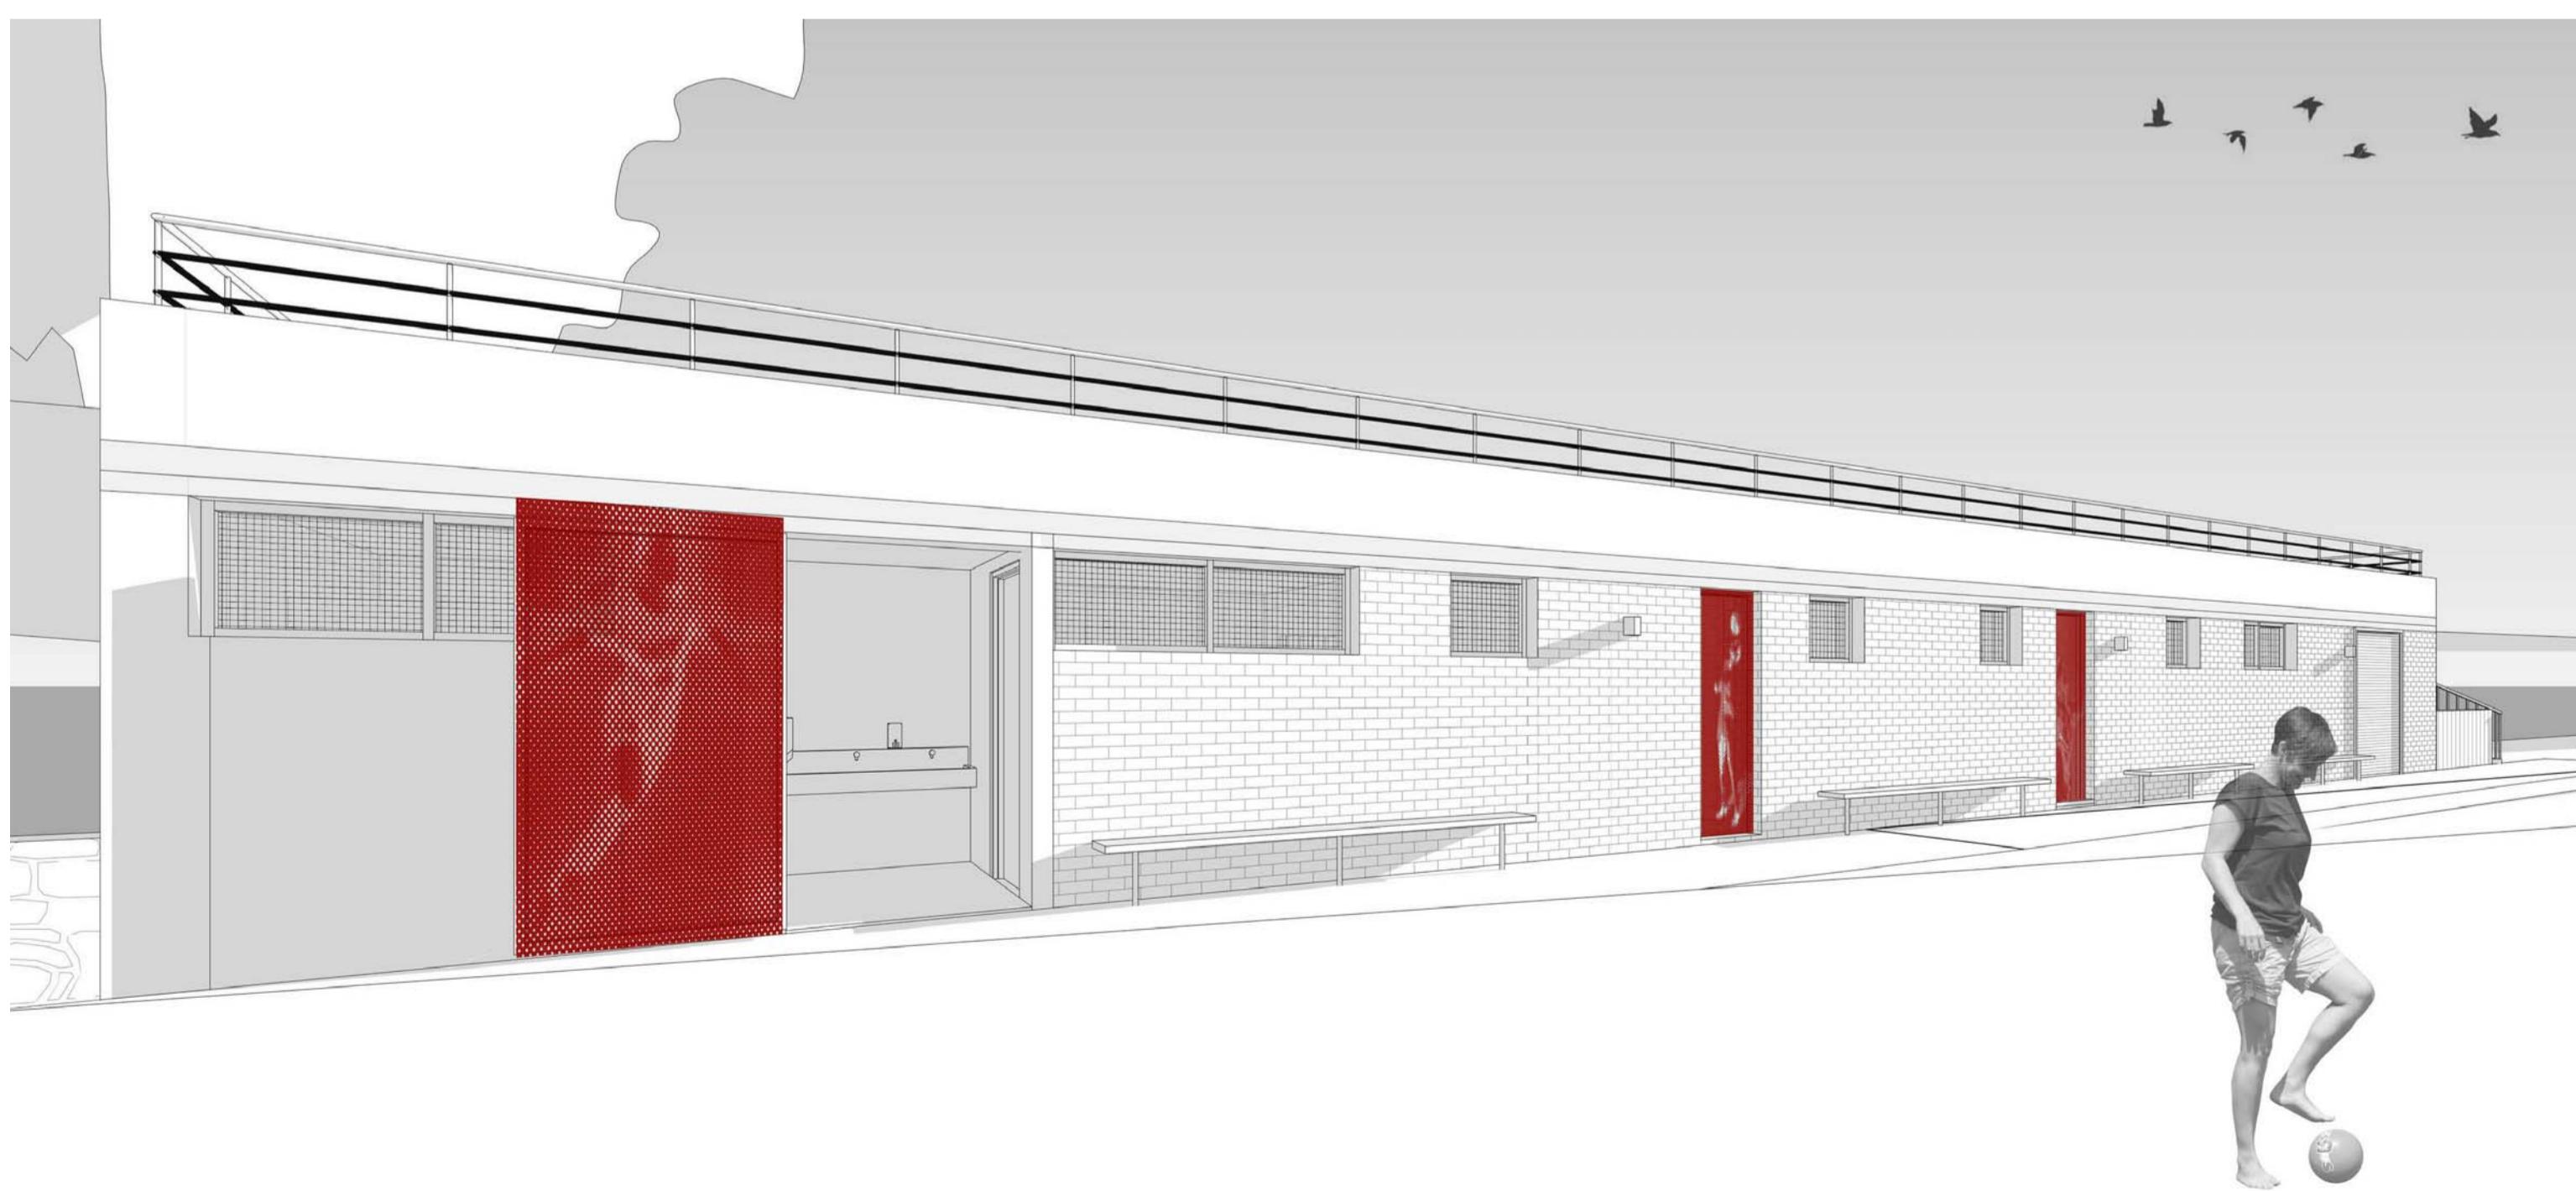

7 Door 1 Detail Section
1 : 5

Issue No. Date Description Chkd AT
A 31/08/2016 TENDER ISSUE

TENDER ISSUE

Electrical Engineer
Ken Offord
601/90 George St, Hornsby, NSW
T: 61 2 9447 4300 F: 61 2 xxxx xxxx
E: offord@bigpond.com

Hydraulic Engineer
Sparks + Partners
Level 1, 91 George Street, Parramatta, NSW
T: 0401 803 330 F: 61 2 9881 3898
E: Leon@sparksandpartners.com.au

Project Manager
Barker College
91 Pacific Highway, Hornsby, NSW, 2077
T: 61 2 9847 8318 F: 61 2 xxxx xxxx
E: georgina_rogers@barker.nsw.edu.au

Drawing Title
Wall Types & Screen Concept - Phipps Field Amenities

Project & Client
BARKER COLLEGE AMENITIES UPGRADE
at 91 Pacific Hwy, Hornsby, NSW, 2077
for BARKER COLLEGE

Architect
NBRSArchitecture.
Sydney Melbourne
61 2 9922 2344 61 3 8676 0427
nbsarchitecture.com.au
Any form of replication of this drawing in full or in part without the written permission of NBRSA+PARTNERS Pty Ltd constitutes an infringement of the copyright
ABN 16 002 247 365 © 2016
Nominated Architects: Geoffrey Deane 3766; Andrew Duffin 5602; Garry Hodnett 5286

Date 31/08/2016 5:20:52 PM
Scale As indicated @ A1

Drawing Reference
15494-WD 702 -A